



MATERIAL:-MS
QTY:- 02 NOS

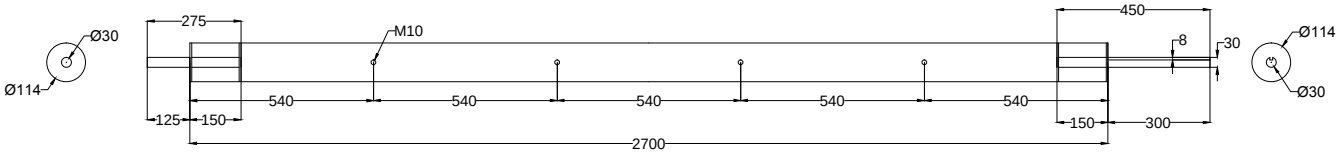

MATERIAL:-MS
QTY:- 01 NOS

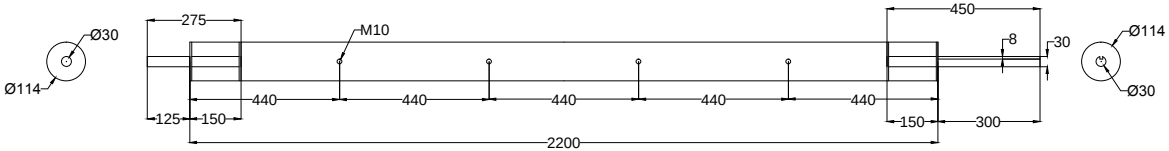

MATERIAL:-MS
QTY:- 02 NOS

DIMENSION :		
CLEAR WIDTH	CLEAR HEIGHT	QUANTITY

MATERIAL :

THICKNESS :

NIHVA TECHNOLOGIES PVT. LTD.
NIHVA TECHNOLOGIES PVT. LTD. PUNE
Email:- info@nihva.com
Website:- www.nihva.com

TITLE:

MS SHAFT

CLIENT'S APPROVAL :

CLIENT - DHOOT BUILDERS

PROJECT -

SITE LOCATION -

DWG. NO. : NIHVA/17-18/MFG/0039

SCALE: NTS	WT:	SHEET:1 OF 1
DRAWN BY: SURAJ		DATE: 07-11-2017
CHECK BY: OMKAR		DATE: 07-11-2017
APPD BY : SHEKHAR		DATE: 07-11-2017

If any queries contact : projects@nihva.com

NOTE: ALL DIMENSIONS ARE IN mm

THIS DRAWING & DESIGNING IS THE PROPERTY OF NIHVA TECHNOLOGIES. NOT TO BE SOLD OR COPIED TO ANY OTHER CONCERN.