
PRELIMINARY SKETCH
PROPOSED TOILET AT TERRACE

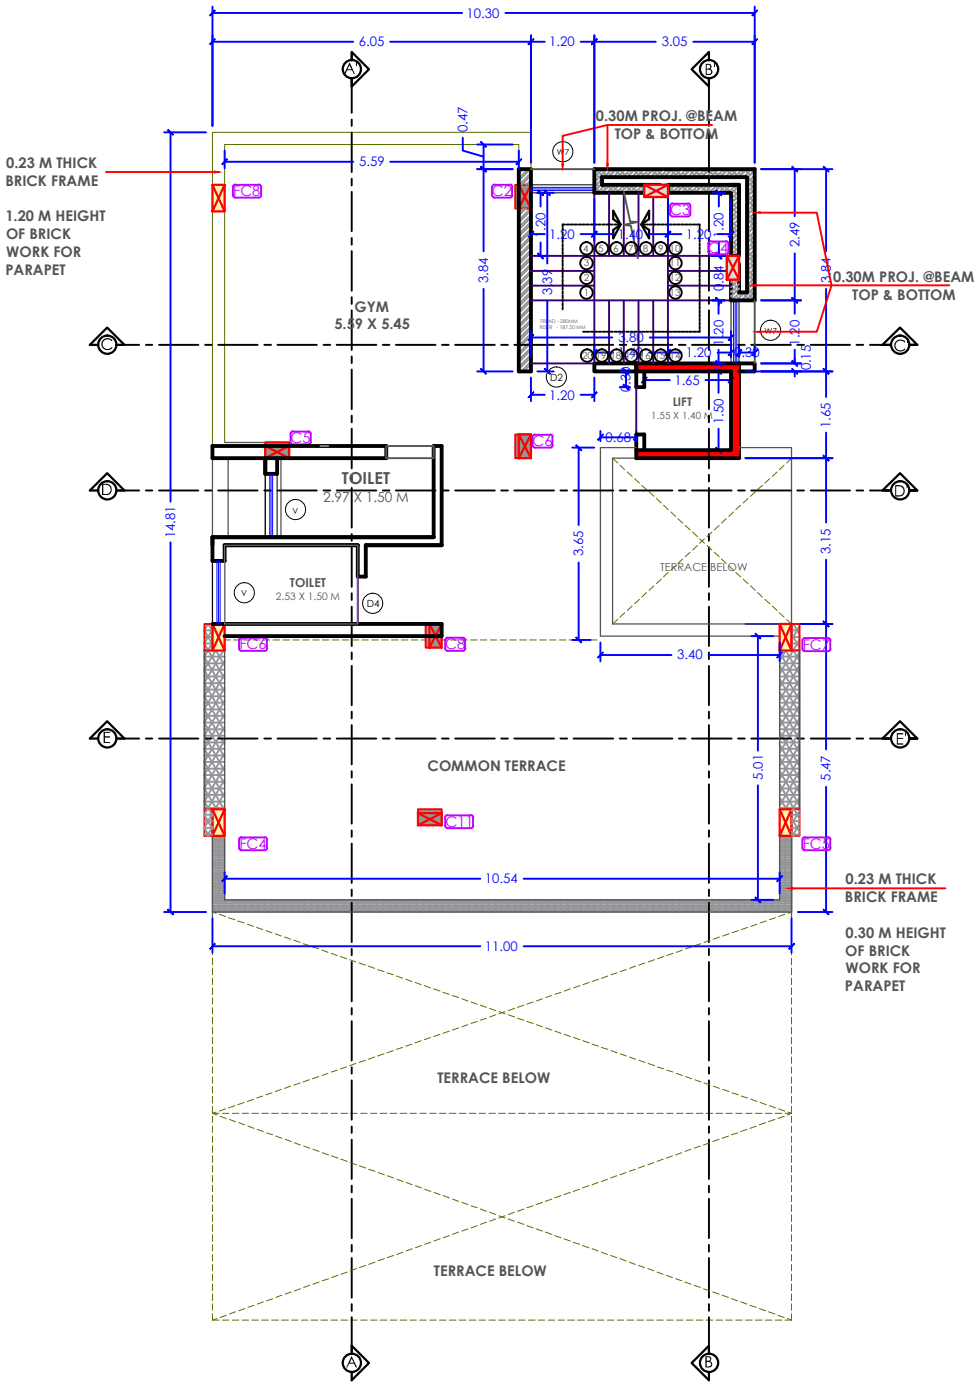

TERRACE FLOOR PLAN
(SCALE 1:100)

NO	NAME	SIZE	NO	NAME	SIZE	SILL
1.	D1	1.50 X 2.65 M	1.	W1	3.40 X 1.60 M	1.20 M
2.	D2	1.20 X 2.40 M	2.	W2	3.07 X 2.05 M	0.60 M
3.	D3	1.00 X 2.40 M	3.	W3	2.00 X 2.20 M	0.60 M
4.	D4	0.90 X 2.40 M	4.	W4	2.00 X 2.05 M	0.60 M
5.	SD	3.60 X 2.80 M	5.	W5	1.20 X 1.90 M	0.90 M
6.	SD1	2.85 X 2.80 M	6.	W6	1.20 X 1.60 M	1.20 M
7.	OP	0.90 X 2.40 M	7.	W7	1.20 X 2.40 M	0.30 M
8.	OP 1	1.87 X 2.40 M	8.	W8	1.15 X 1.60 M	1.20 M
			9.	W9	0.90 X 2.05 M	0.60 M
			10.	W10	0.90 X 2.20 M	0.60 M
			11.	W11	0.75 X 2.20 M	0.60 M
			12.	V	1.20 X 1.60 M	1.20 M
			13.	V1	0.75 X 1.20 M	1.20 M
			14.	V2	0.60 X 1.20 M	1.20 M

NOTE : THIS DRAWING IS THE SOLE PROPERTY OF THE ARCHITECT. IT MUST NOT BE COPIED OR REPRODUCED IN ANYWAY OR MADE ACCESSIBLE TO THIRD PARTY WITHOUT THE WRITTEN APPROVAL OF THE OWNER.

GENERAL NOTES :

1. ALL THE DIMENSIONS ARE IN MM UNLESS AND UNTIL MENTIONED OTHERWISE
2. DIMENSIONS ARE TO BE READ ONLY AND NOT TO BE SCALED.
3. THE LEVELS MENTIONED ARE FINISHED FLOOR LEVELS UNLESS STATED.
4. THE ARCHITECTURAL WORKING DRAWING MUST BE CO-ORDINATED WITH RELEVANT DRAWINGS FROM OTHER CONSULTANTS.
5. THE CONTRACTOR SHALL BE KNOWLEDGEABLE OF ALL SITE CONDITIONS AND SHALL NOTIFY THE ARCHITECT OF ANY CONDITIONS REQUIRING MODIFICATION BEFORE PROCEEDING WITH THE WORK.
6. THE CONTRACTOR SHALL VERIFY IN THE FIELD ALL DIMENSIONS AND ELEVATIONS BEFORE PROCEEDING WITH THE WORK. THE ARCHITECT SHALL BE NOTIFIED OF ANY DISCREPANCIES BEFORE PROCEEDING WITH THE WORK
7. THE CONTRACTOR SHALL COORDINATE ALL FLOOR AND WALL OPENINGS AND PENETRATIONS REQUIRED BY VARIOUS TRADES WITH STRUCTURAL AND ARCHITECTURAL. THE ARCHITECT SHALL BE NOTIFIED OF ANY DISCREPANCIES OR CONFLICTS BEFORE PROCEEDING WITH THE WORK.
8. ALL WORK SHALL CONFORM TO ALL APPLICABLE CODES AND SHALL BE THE BEST PRACTICE OF EACH TRADE.

SPECIFICATIONS :

LEGENDS :

BRICKWALL

- 0.380M THICK
- 0.230M THICK
- 0.220M THICK
- 0.200M THICK
- 0.150M THICK

- 0.30 M HEIGHT
- 1.20 M HEIGHT

OPENING SCHEDULE

	NAME	SIZE	SPECIFICATION
01.			
02.			
03.			
04.			
05.			
06.			
07.			
08.			

NO.	DATE	REVISION ISSUED TO

PROJECT :

CLIENT :

PURPOSE OF RELEASE :

DWG TITLE :

FLOOR : FIRST / SECOND

BUILDING BLOCK : A/B/C

DEALT BY :

CHECKED BY :

ISSUED DATE :

ARCHITECT:
AR.GAURAV SALUNKE
REGD. NO.: CA/92/14809

CONTACT:
GAURAV : 07226222200

MAIL ID:
ssamskara.arch@gmail.com