

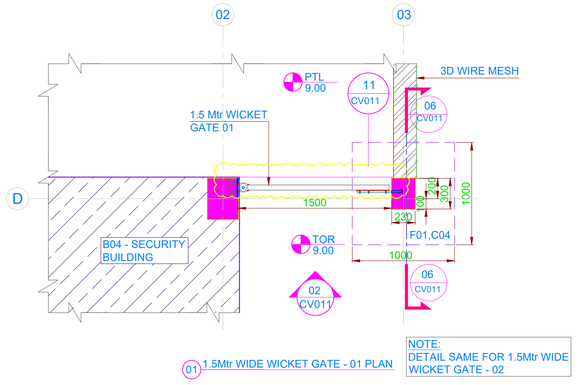


01 1.5Mtr WIDE WICKET GATE - 01 PLAN


NOTE:
DETAIL SAME FOR 1.5Mtr WIDE WICKET GATE - 02

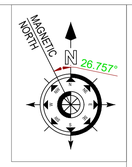

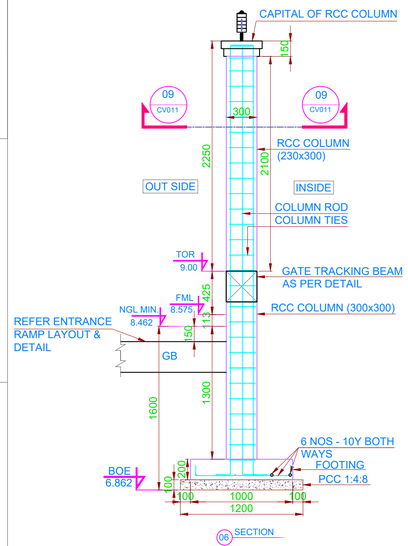

06 SECTION


TYPICAL REINFORCEMENT DETAIL FOR
1.5 Mtr WIDE WICKET GATE COLUMN

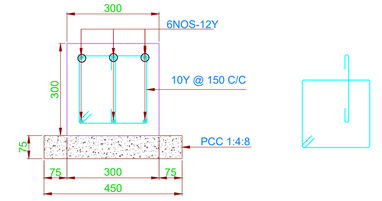

07 SECTION
SCALE 1:10

08 TIES PROFILE
SCALE 1:10


TYPICAL REINFORCEMENT DETAIL FOR GATE
TRACKING BEAM (300 x 300)

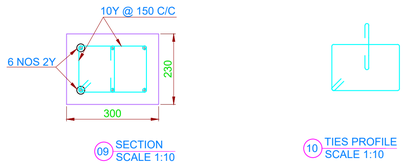


09 SECTION
SCALE 1:10


10 TIES PROFILE
SCALE 1:10

TYPICAL REINFORCEMENT DETAIL FOR
RCC COLUMN (230x300)

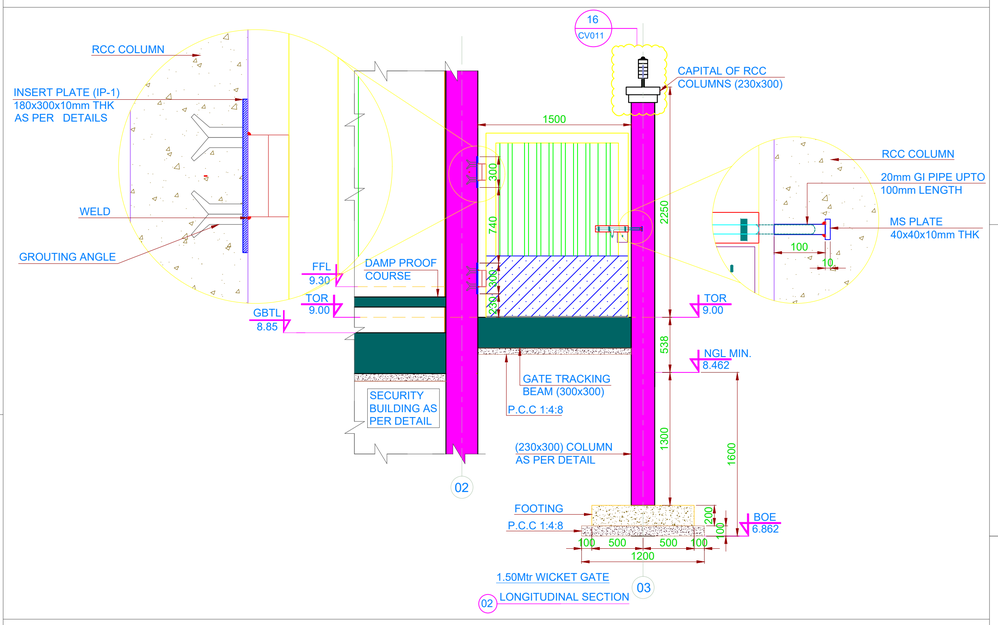


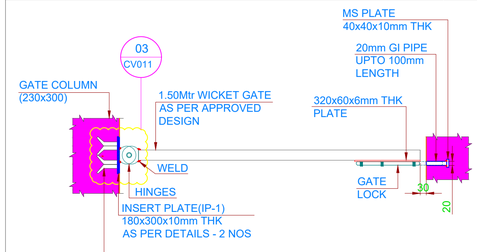


11 1.50Mtr WICKET GATE DETAIL
SCALE 1:15

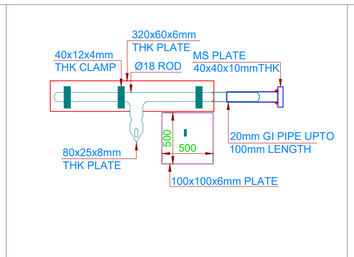


12 GATE LOCK FOR 1.50 Mtr WICKET GATE
SCALE 1:6

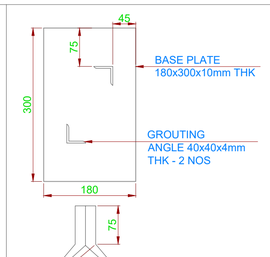


13 INSERT PLATE(IP-1) DETAIL
SCALE 1:6

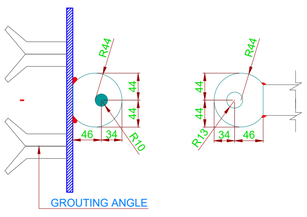

03 HINGES PLAN

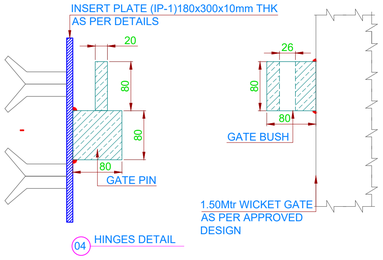

04 HINGES DETAIL

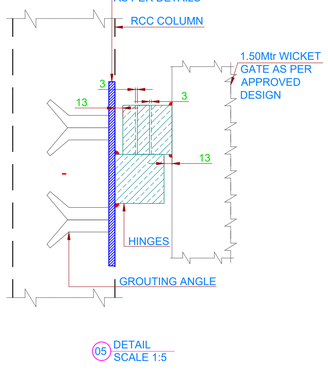


05 DETAIL
SCALE 1:5


HINGE FIXING DETAIL FOR 1.50Mtr WICKET GATE

HATCHES	
	RCC
	PCC
	COMPACTED EARTH
	NATURAL SOIL
	150 THK BLOCK WORK
	200THK BLOCK WORK


LEGEND	
GTB	GATE TRACKING BEAM
GTBTL	GATE TRACKING BEAM TOP LEVEL
GBTL	GRADE BEAM TOP LEVEL
GB	GRADE BEAM
TOR	TOP OF ROAD
FML	FORMATION LEVEL
NGL MIN.	NATURAL GROUND LEVEL MINIMUM

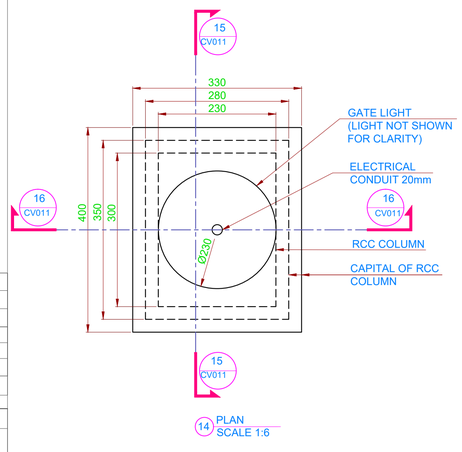

14 PLAN
SCALE 1:6

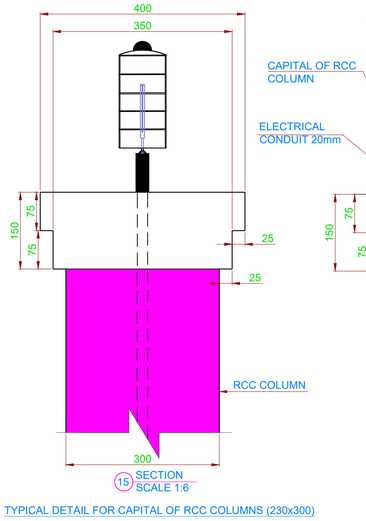

15 SECTION
SCALE 1:6

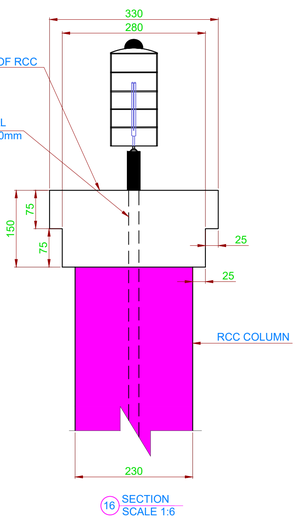

16 SECTION
SCALE 1:6

TYPICAL DETAIL FOR CAPITAL OF RCC COLUMNS (230x300)

IMPORTANT NOTE :
VENDOR SHOP DRAWING AND TECHNICAL DATA SHEET TO BE SUBMITTED FOR APPROVAL.

NOTE:
READ THIS DRAWING IN CONJUNCTION WITH BOUNDARY WALL LAYOUT, BOUNDARY WALL DETAIL, BOUNDARY WALL ELEVATION DRAWINGS.

GENERAL NOTES

1. ALL DIMENSIONS ARE IN 'mm'.
2. ALL LEVELS ARE IN 'Mtrs'.
3. GRADE OF CONCRETE - M25
4. Y= HIGH YIELD STRENGTH REINFORCEMENT STEEL FE500D TMT BARS

KEY PLAN

Date	Purpose of Issue	Version
23.01.2024	GOOD FOR CONSTRUCTION	R0

Milestones

GOOD FOR CONSTRUCTION

VER	DSN	Date	DRW	Date	CHK	Date	APR	Date
R0	VR	23.01.24	FV	23.01.24	MV	23.01.24	DC	23.01.24

CLIENT

ROCKMAN INDUSTRIES LTD,
9th FLOOR, UNIT 3&4, EMAAR CAPITAL TOWER - 2
SECTOR - 26, SIKANDERPUR GHOSI, M G ROAD,
GURUGRAM – 122002. HARYANA, INDIA

PROJECT NAME	PROJECT CODE
M/S. ROCKMAN INDUSTRIES CHENNAI PVT.LTD, NO:6/2, CHELLAPERUMPULIMEDU, CHOLAVARAM POST,CHEYYAR TALUK,THIRUVANNAMALAI DISTRICT-631701.	357

ARCHITECTS & CONSULTANTS

BESTEN Engineers & Consultants India Pvt. Ltd.
F-2, LAKSHMI APARTMENTS,
NO. 95, PERIYAR PATHAI,CHOOLAIMEDU (WEST),
CHENNAI - 600 094.
PH : 044 - 23611595. email : contact@besten.in, www.besten.in

Project Component :	Scale at A1
SITE	1 : 30

DRAWING NO.	Sheet No
SI 107 CV 011	01 / 01

Drawing Title :	Revision No
1.50 Mtr WICKET GATE DETAIL	GF R 0

Graphic Scale :

0 1 2 3 4 5 6 7 8 9 10

This drawing and its contents is the property of Besten Engineers & Consultants India Private Limited and is covered under intellectual property rights. This drawing must not be copied, electronically transmitted, or passed on to any third person/firm/ party in part or in full, nor be made use by such persons/ firm/ parties without our authorisation in writing. This drawing is to be returned after the purpose of issue is fulfilled.