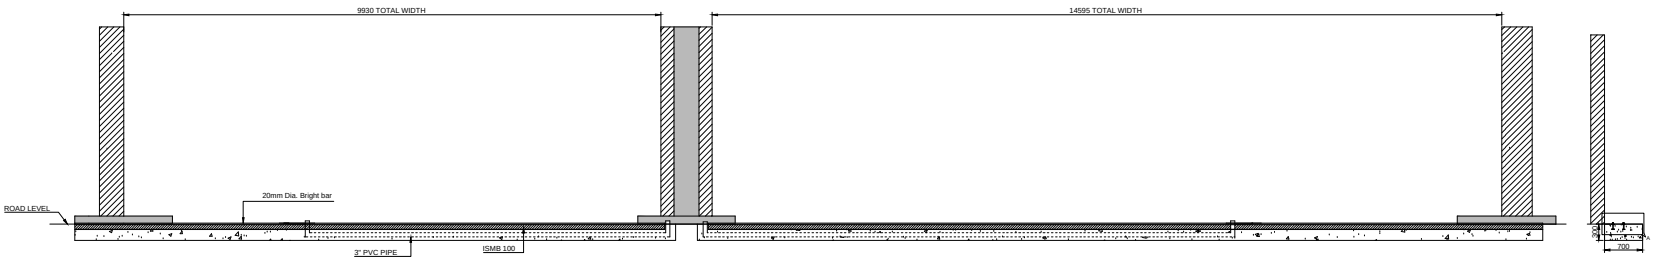

OUTSIDE ELEVATION

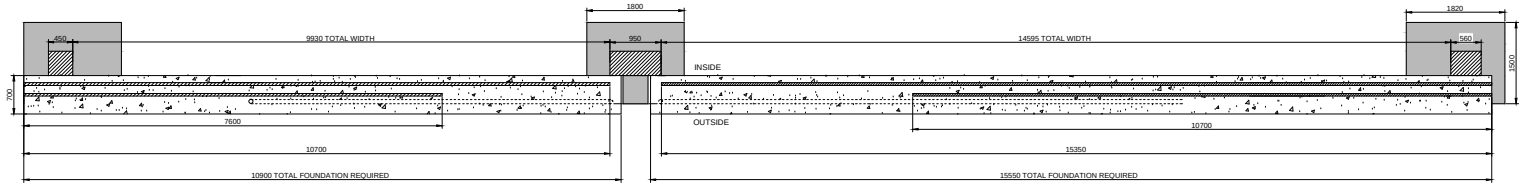

PLAN

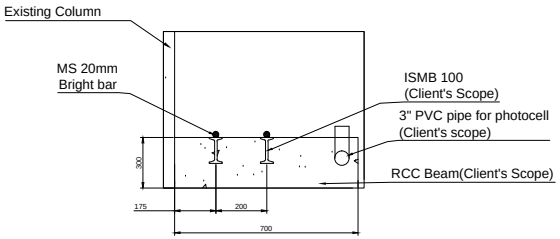

Detailed View of A

REV NO	DATE	DESCRIPTION
REV -0	12/02/18	INITIAL DRAWING
REV -1	20/02/18	GATE SIZES HAVE CHANGED

DIMENSION :

CLEAR WIDTH	CLEAR HEIGHT	QUANTITY
9500 mm	3000 mm	1 NOS.
6400 mm	3000 mm	1 NOS.

MATERIAL : MS

THICKNESS :

NOTE: ALL REQUIRED CIVIL WORK WILL BE IN CLIENT'S SCOPE.
ONE COAT RED OXIDE PRIMER WILL BE GIVEN TO THE STRUCTURE OF GATE.
TWO COATS OF FINAL APPROVED RAL SHADE WILL BE GIVEN TO THE CLIENT.
ISMB 100 WILL BE CLIENTS SCOPE.

NIHVA
NIHVA TECHNOLOGIES PVT. LTD.
NIHVA TECHNOLOGY PVT. LTD. PUNE
Email:- info@nihva.com
Website:- www.nihva.com

TITLE:

FOUNDATION TWO LEAF TELESCOPIC SLIDING GATE 9.5X3m & 6.4x3m

CLIENT'S APPROVAL :

CLIENT - WILO MATHER & PLATT PUMPS PVT. LTD.

PROJECT -

SITE LOCATION - AKURDI

DWG. NO. : NIHVA/17-18/0362/R01 | REV- 1

SCALE: NTS | WT: | SHEET:1 OF 1

DRAWN BY: OMKAR | DATE: 12-02-2018

CHECK : SHEKHAR | DATE: 12-02-2018

APPROVED : SHEKHAR | DATE: 12-02-2018

If any queries contact : design@nihva.com

NOTE: ALL DIMENSION ARE IN mm

THIS DRAWING & DESIGNING IS THE PROPERTY OF NIHVA TECHNOLOGIES. NOT BE SOLD OR COPY TO ANY OTHER CONCERN.