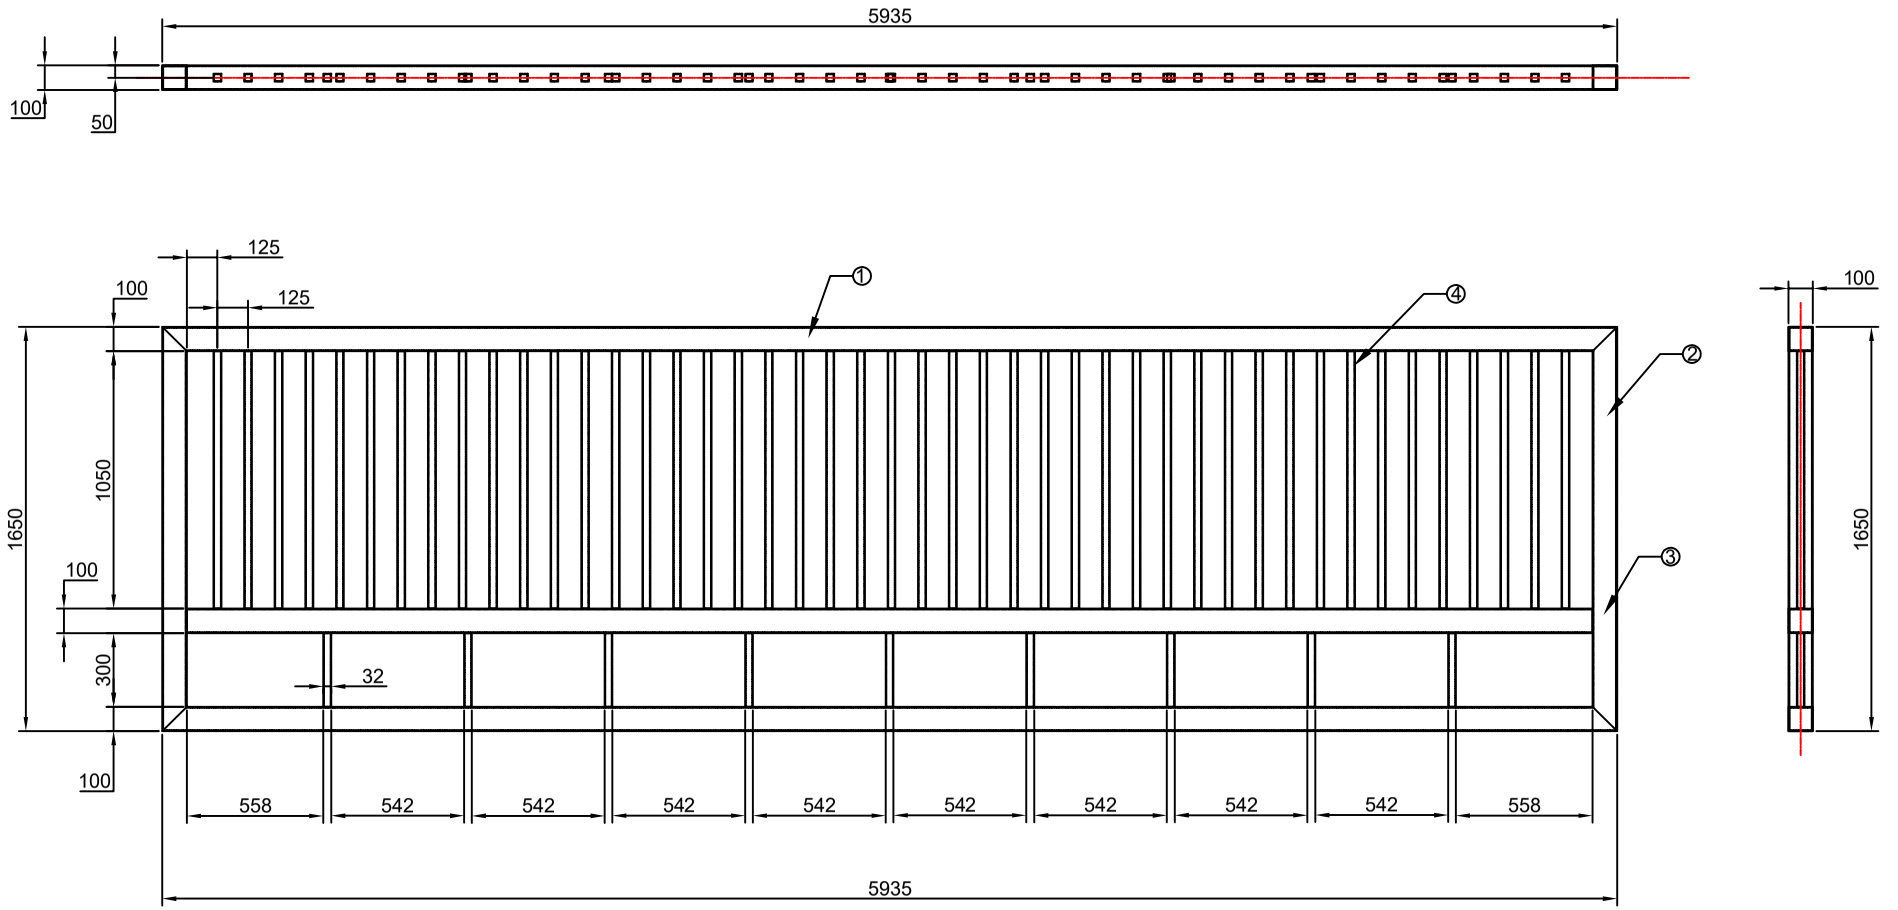


BOM			
SL NO.	DESCRIPTION	SPECIFICATION	QTY
1	MS SQ. TUBE	100X100X4X5935L	2NOS
2	MS SQ. TUBE	100X100X4X1650L	2NOS
3	MS SQ. TUBE	100X100X4X5735L	1NOS
4	MS SQ. TUBE	32X32X2.6X1050L	45NOS
5	MS SQ. TUBE	32X32X2.6X300L	9NOS
6	CLADDING1	As per drawing NIHVA/21-22/VDR/025	2NOS
7	CLADDING2	As per drawing NIHVA/21-22/VDR/025	8NOS

This drawing & design is the property of NIHVA TECHNOLOGIES. Not to be sold or copied to any other concern.

TITLE:- Single Leaf for tel.sliding gate

	NAME	DATE	SIGN
DRAWN	SUJATA	04/02/2022	
CHECK	G.PATIL	04/02/2022	
APPRD.	A.K	04/02/2022	

If any queries contact : design@nihva.com

ALL DIMENSION ARE IN mm

NIHVA
NIHVA TECHNOLOGIES PVT. LTD.

NIHVA TECHNOLOGIES PVT. LTD. PUNE
Tel : 020 66304033
Email:- info@nihva.com
Website:- www.nihva.com

CLIENT -

LOCATION -

PRODUCT - SWING GATE | QTY- 03

DWG NO:-NIHVA/21-22/MFG/021 | REV- 0

SCALE: NTS | SCALE:-- 1:1 | SHEET: 01 OF 01

Rev No.	Revision	Date	Revised By