STRUCTURAL DETAILS

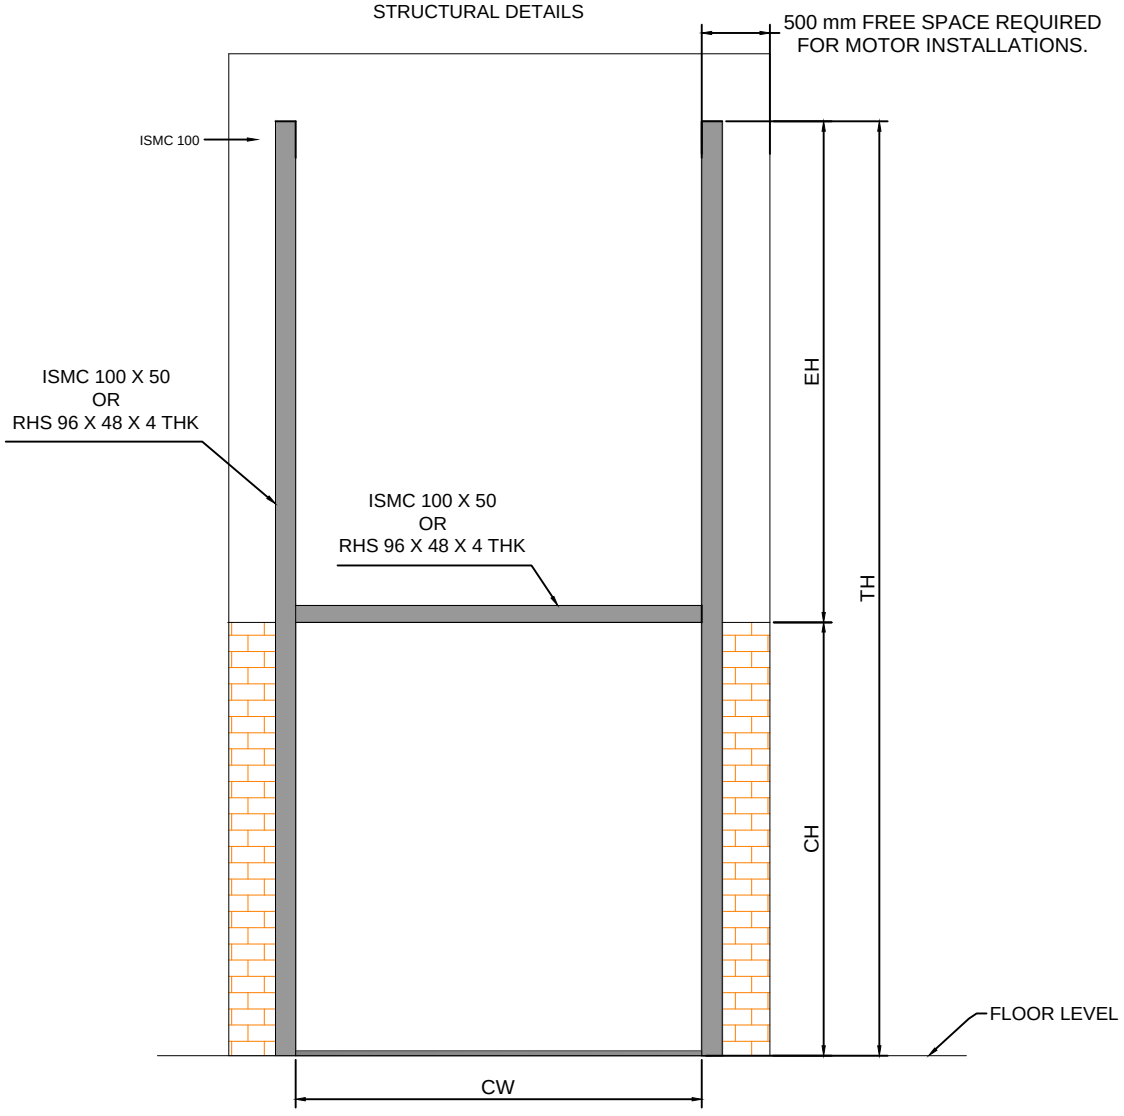

INSIDE ELEVATION

SR NO	CLEAR WIDTH CW	CLEAR HEIGHT CH	QTY	TH	EH
1	3000mm	4000mm	3	8400	4400
2	5000mm	4000mm	1	8400	4400
3	6500mm	4000mm	1	8400	4400

NOTE- M.S STRUCTURE FOR SECTIONAL DOOR WILL BE IN CLIENTS SCOPE.

This drawing & design is the property of NIHVA TECHNOLOGIES. Not to be sold or copied to any other concern.

TITLE: STRUCTURE FOR SECTIONAL DOOR

	NAME	SIGN	DATE
DRAWN	P.A		04.01.19
CHECK	G.J		04.01.19
REV.			
APPROVAL			

If any queries contact : projects@nihva.com

ALL DIMENSION ARE IN mm

NIHVA TECHNOLOGIES PVT. LTD. PUNE
Tel : 020 66304033
Email:- info@nihva.com
Website:- www.nihva.com

CLIENT - SCON

PROJECT - INNOVATEC INDIA PVT. LTD.

SITE LOCATION - SANAND

DWG. NO. : NIHVA/19-20/0188

SCALE: NTS | WT: | SHEET: 01 OF 01