



SLIDING DIRECTION

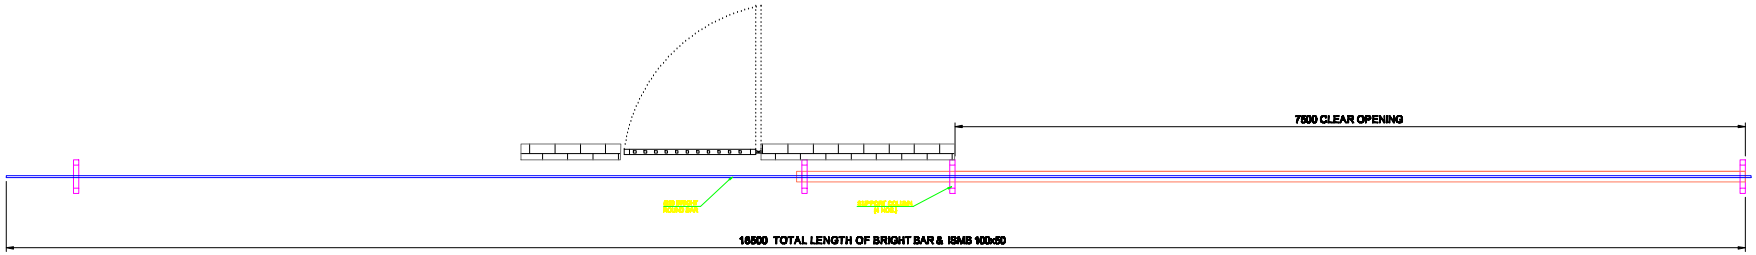

INSIDE VIEW

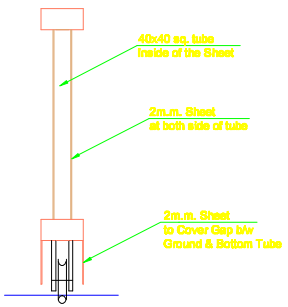

Clear Opening size - 7500X1800mm
Total length of gate - 9000 1800mm
Wicket gate size - 200X1800mm , Qty - 2 nos.
Saftey Photo cell - 1 pair.
No. Of Column - 4 nos.
Factory paint finish - Red oxide primer coat
NOTE :- Supply of 'c' channel for vertical support of wicket gate in NIHVA scope
*Excavation and civil work for grouting of 'c' channel & I beam will be in client scope.

TITLE

MOTORIZED SLIDING GATE

CLIENT APPROVAL

This drawing & designing is the property of NIHVA TECHNOLOGIES. Not be sold or copy to any other concern.

ALL DIMENSION ARE IN mm

	SIGN	DATE
DRAWN	ABHIJIT	14/04/15
CHECK	ANIL	14/04/15
REV.	01	
APPRD.		
MFG		
Ref. No.		

NIHVA
NIHVA TECHNOLOGIES PVT. LTD.

NIHVA TECHNOLOGY PVT. LTD. PUNE
Tel : 020 66304033
Email:- info@nihva.com
Website:- www.nihva.com

CLIENT - PMP DRIVE SYSTEM
PROJECT - PMP DRIVE SYSTEM
SITE - CHAKAN
DWG. NO. - - - - - - -
SCALE: 01 | WT: | SHEET: 01 OF 02
If any queries contact : projects@nihva.com