

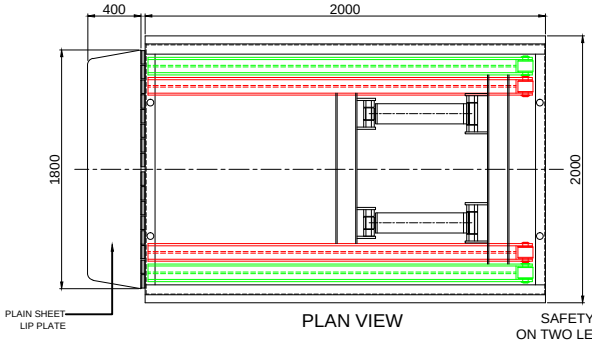



PLAN VIEW

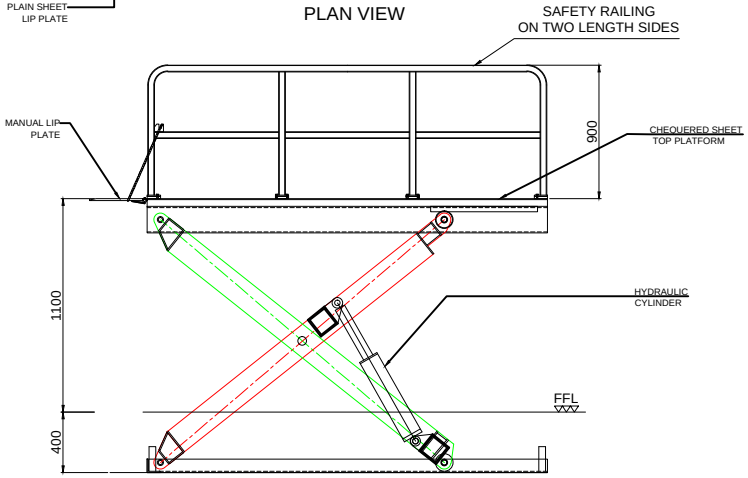


FRONT VIEW - OPEN POSITION OF SCISSOR LIFT

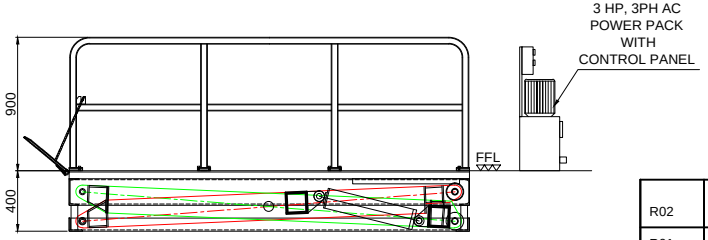

FRONT VIEW - SHUT POSITION OF SCISSOR LIFT

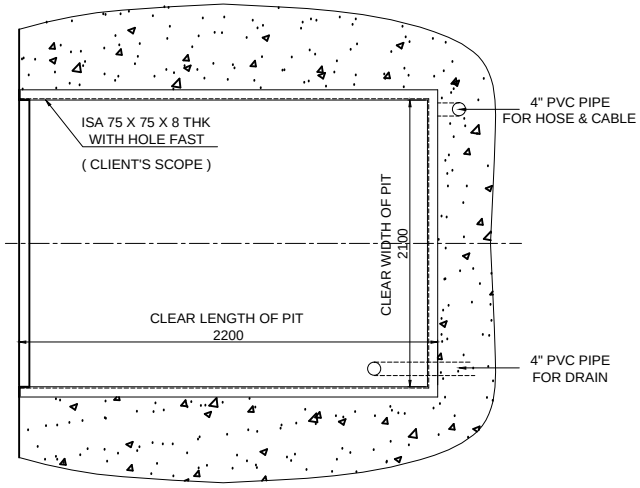

TOP VIEW OF PIT

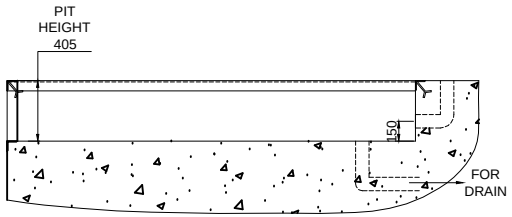

FRONT VIEW OF PIT

NOTES-

1. REQUIRED DUCT , PIT & ALL CIVIL WORK IS IN CLIENT SCOPE .
2. PIT SURFACE SHOULD BE PLAIN & TAKE UNIFORM DISTRIBUTED LOAD OF 4000 KG.
3. GOLDEN YELLOW PAINT IS NIHVA STANDARD RAL SHADE , IF ANY OTHER PLEASE INFORM .

TOLERANCE - ±10mm

PAINT - RAL 1004 GOLDEN YELLOW

CAPACITY	3 TON
PLATFORM SIZE	2000 (L) X 2000(W)
POWER PACK	3 HP, 3 PH
SHUT HEIGHT	400 MM
LIFT HEIGHT FROM FFL	1100 MM
TOTAL HEIGHT FROM PIT BOTTOM	1500 MM

REV NO	DRAWN	DATE	REMARK
R02	SMS	30.3.2021	LIFT HEIGHT CHANGED AS PER SITE REQUIREMENT
R01	SMS	13.3.2021	PIT DETAILS CHANGED CAPACITY CHANGED TO 3 TON

This drawing & designing is the property of NIHVA TECHNOLOGIES. Not be sold or copy to any other concern.

TITLE PIT MOUNTED ELECTRO-HYDRAULIC SCISSOR LIFT

NIHVA TECHNOLOGIES PVT. LTD.
NIHVA TECHNOLOGY PVT. LTD. PUNE
Tel : 020 66304033
Email:- info@nihva.com
Website:- www.nihva.com

	SIGN	DATE
DRAWN	SIDDHESHWAR	25.1.2021
CHECK	SIDDHESHWAR	25.1.2021
REV.		
APPROVAL		

CLIENT - TOPBAND INDIA PVT LTD
PROJECT - TOPBAND INDIA PVT LTD
SITE - PUNE
DWG. NO. : NIHVA/20-21/0142/R02
If any queries contact : nihvacare@nihva.com
SCALE: NTS | WT: | SHEET: 01 OF 01
ALL DIMENSION ARE IN mm