





SECTION 1 THROUGH ROOF
SCALE-1:200

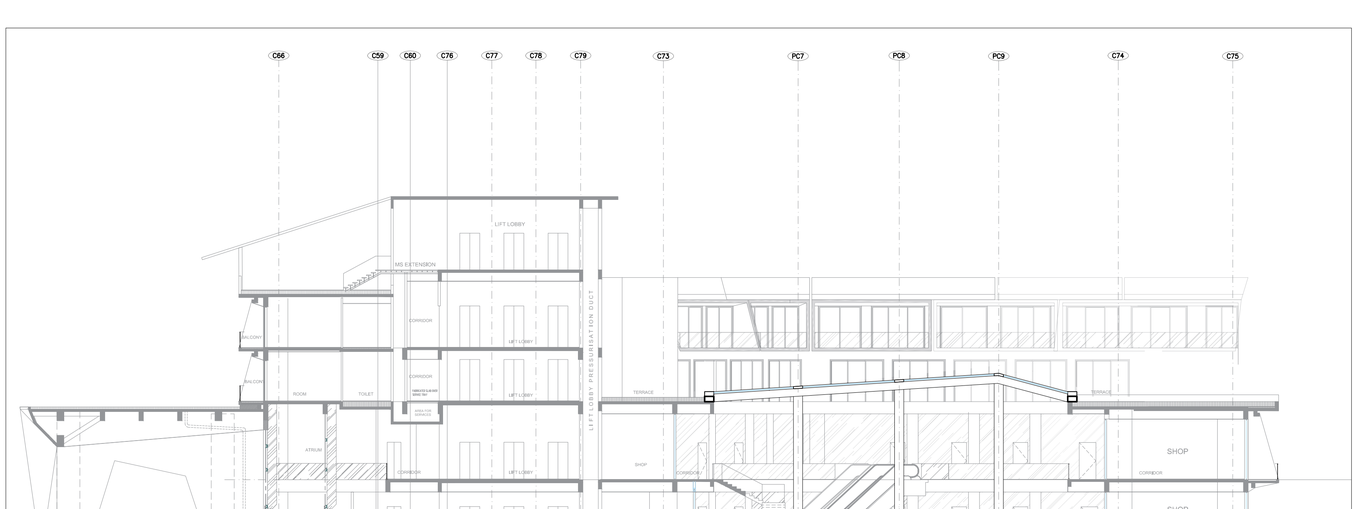


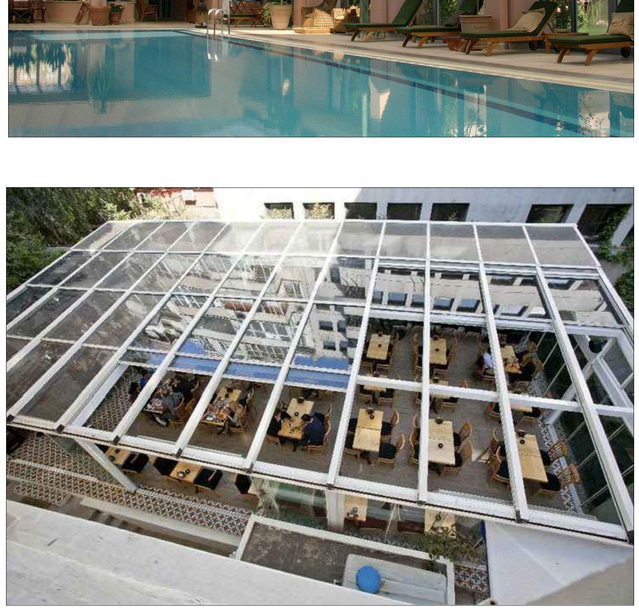


REFERENCE IMAGES

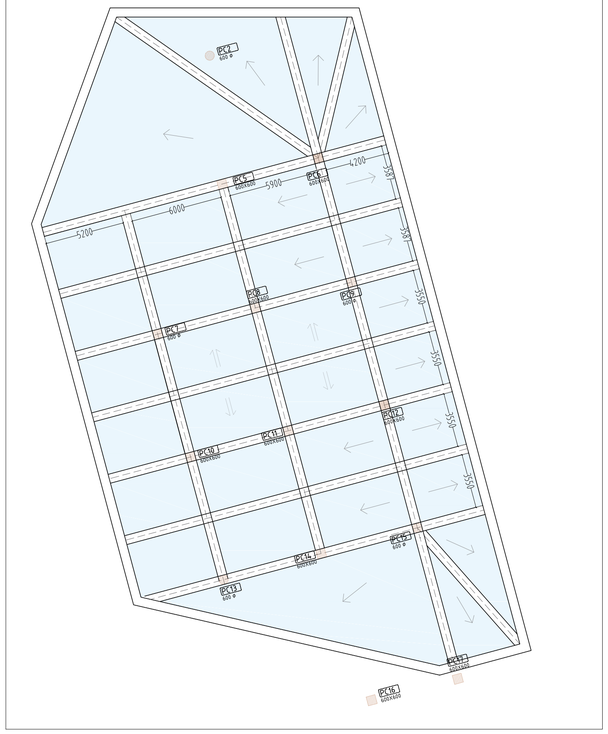

ATRIUM ROOF PLAN WITH ALL PANELS CLOSED
SCALE:1:200

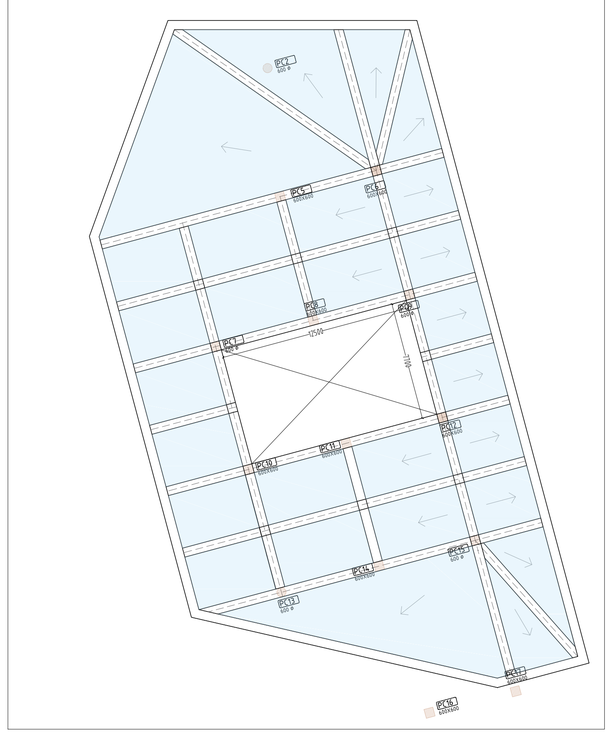

ATRIUM ROOF PLAN WITH ALL PANELS CLOSED
SCALE:1:200

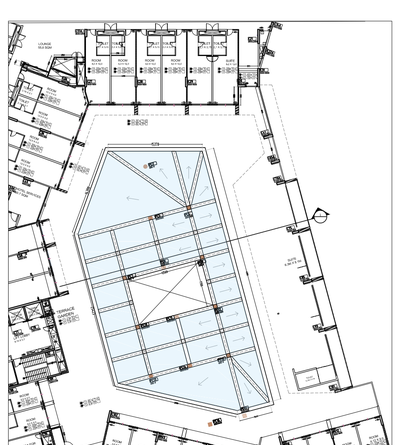

KEY PLAN
SCALE-1:500

NOTE: ALL DIMENSIONS ARE IN MM.

DRAWING NO.

ANJAY PURI ARCHITECTS

NOTES
1. THIS DRAWING IS THE COPYRIGHT OF SANJAY PURI ARCHITECTS PVT. LTD. AND MUST NOT BE RETAINED OR COPIED WITHOUT THE PERMISSION OF THE ABOVE CONSULTANTS.
2. DO NOT SCALE FROM THE DRAWINGS. ALL DIMENSIONS ARE IN MILLIMETRES AND LEVELS IN METRES UNLESS OTHERWISE NOTED.
3. ALL DIMENSIONS TO BE VERIFIED ON SITE AND APPROVED BY THE ENGINEER.
4. THIS DRAWING SHOULD BE READ IN CONJUNCTION WITH OTHER RELEVANT ARCHITECTURAL, STRUCTURAL, MECHANICAL, ELECTRICAL AND CIVIL DRAWINGS AND ALL RELEVANT SECTIONS OF THE STRCUTURAL AND SERVICES DWGS

KEY PLAN

| REV. | DESCRIPTION | DATE | REV. BY |
|---|---|---|---|
| | | | |

NORTH N

SCALE 1:200 A1

PROJECT NUMBER NS-HO-03
CLIENT CIE
PROJECT NAME, LOCATION LEGEND RESORTS SRINAGAR

DATE 18-08-2022
CHECKED BY:
DRAWN BY:

DRAWING NAME ATRIUM ROOF DESIGN
DRAWING NO.
REVISION
DRAWING STATUS

sanjay puri architects ltd 20 famous studio lane off dr e moses road mahalakshmi mumbai - 400011 t: +91-22-2496-5840 / 41 / 42 / 43 / 44 f: +91-22-2496-5896 e: snstudio@sanjayvuri.in i: www.sanjayvuriarchitects.com