


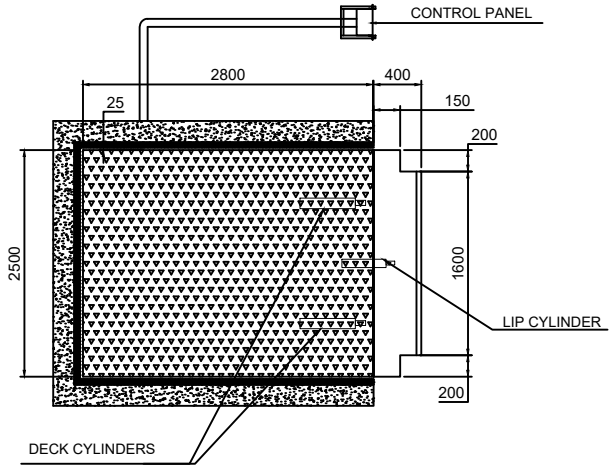


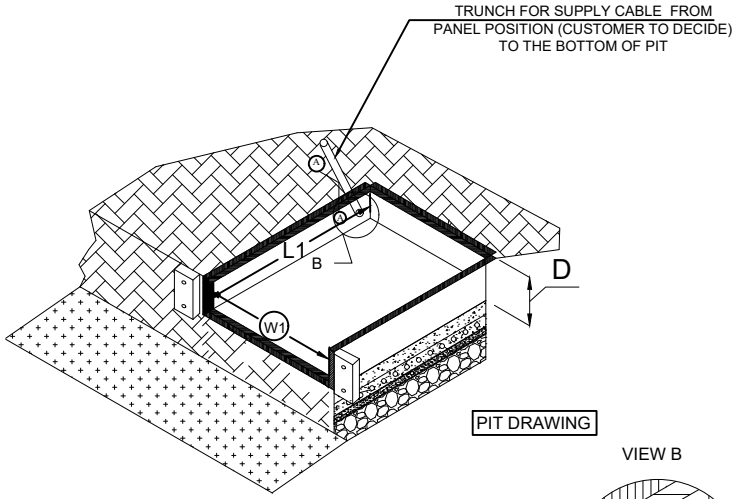


PIT DRAWING

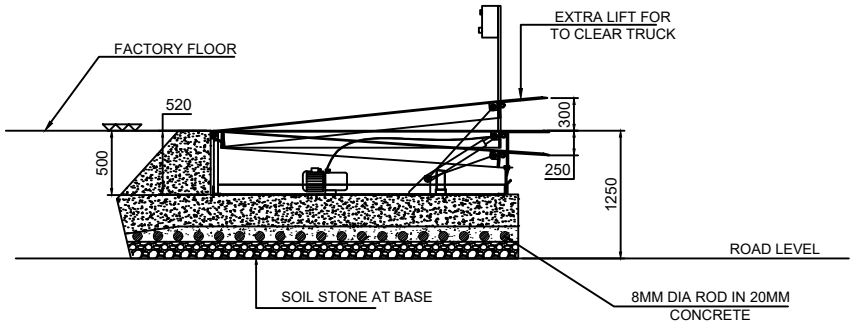

VIEW B

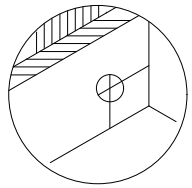

Section at A-A

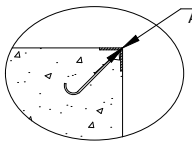

Capacity:- 06TON

DOCK LEVELER SIZE	WIDTH (W)	LENGTH (L)	HEIGHT (H)	LIP (C) LENGTH
	2500	2800	500	400

NOTE:-

1. ALL DIMENSIONS ARE IN MM
2. THES DRAWING IS FOR UNDERSTANDING PURPOSE
3. PIT,DUCT FOR HOSES & ALL CIVIL WORK IN CLIENT SCOPE

This drawing & design is the property of NIHVA TECHNOLOGIES. Not to be sold or copied to any other concern.

TITLE:- DOCK LEVELER GA DRAWING

NIHVA TECHNOLOGIES PVT. LTD.
NIHVA TECHNOLOGIES PVT. LTD. PUNE
Tel : 020 66304033
Email:- info@nihva.com
Website:- www.nihva.com

	NAME	DATE	SIGN
DRAWN	S.J	13/07/2024	
CHECK	A.K	13/07/2024	
APPRD.	V.T	13/07/2024	

CLIENT -

LOCATION -

PRODUCT - DOCK LEVELER

If any queries contact : design@nihva.com

DWG NO:-NIHVA/24-25/00XX

REV- 0

ALL DIMENSION ARE IN mm

SCALE: NTS

SCALE:-- 1:1

SHEET: 01 OF 01