
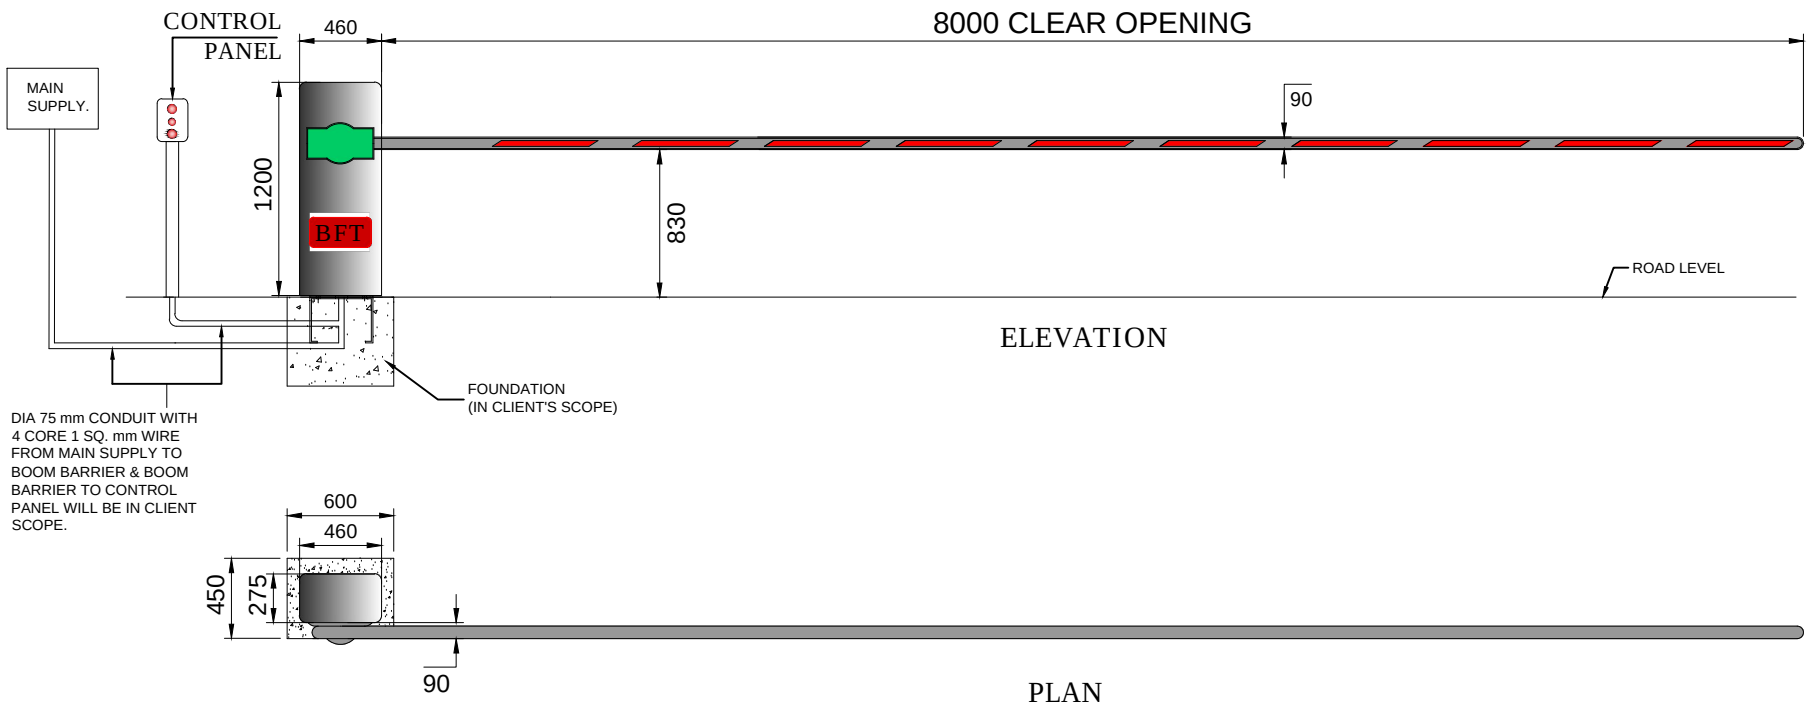


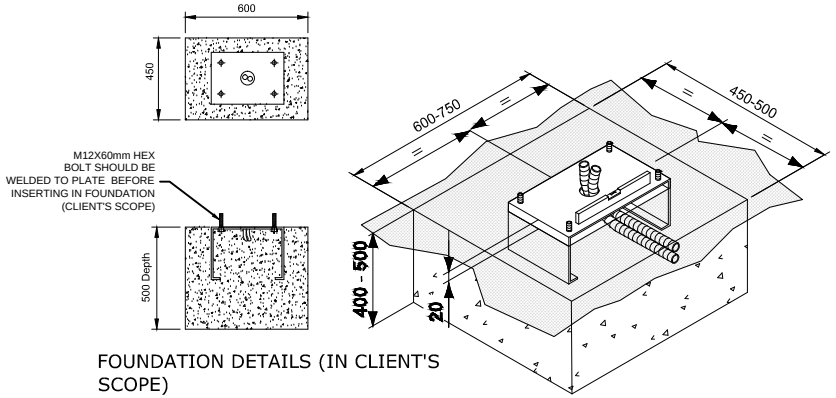

FOUNDATION DETAILS (IN CLIENT'S SCOPE)

SR NO	CLEAR WIDTH	QTY.
1	8000mm	01 NOS

TOLERANCE - ±10mm

This drawing & design is the property of NIHVA TECHNOLOGIES. Not to be sold or copied to any other concern.

TITLE: BOOM BARRIER 8m

NIHVA TECHNOLOGIES PVT. LTD. PUNE
Tel : 020 66304033
Email:- info@nihva.com
Website:- www.nihva.com

	NAME	SIGN	DATE
DRAWN	SURAJ		29-01-2018
CHECK	OMKAR		29-01-2018
APPRD.	SHEKHAR		29-01-2018
MFG.			

CLIENT - INBISCO INDIA PVT LTD.
PROJECT -
SITE LOCATION -AHMEDABAD,GUJARAT.
DWG. NO. : NIHVA/17-18/0341 REV-0
If any queries contact : projects@nihva.com
SCALE: NTS WT: SHEET: 01 OF 01
ALL DIMENSION ARE IN mm