


ITEM NO.	PART NUMBER	DESCRIPTION	QTY.
1	CIVIL BASE	(L)- 19000 (W) -3350	1
2	EN 8 BAR AND ISMB 1	(L) - 19200	1
3	SLIDING GATE ASM	(L)- 4800 (H)- 1675	2
4	POST ASM (75X75)	(L)- 330 (H)-1825	8
5	nylon roller and bolt asm	(DIA)- 50 (H)- 72	12
6	NUT	(ID)- 5 (OD)-10 (H)-10	12
7	SINGLE POST ASM (75X75)	(L)- 330 (H)-1825	4
8	Tower Bolt SUPPORT	(L)- 70 (H)-460	2
9	Tower Bolt	DIA- 29.8	2

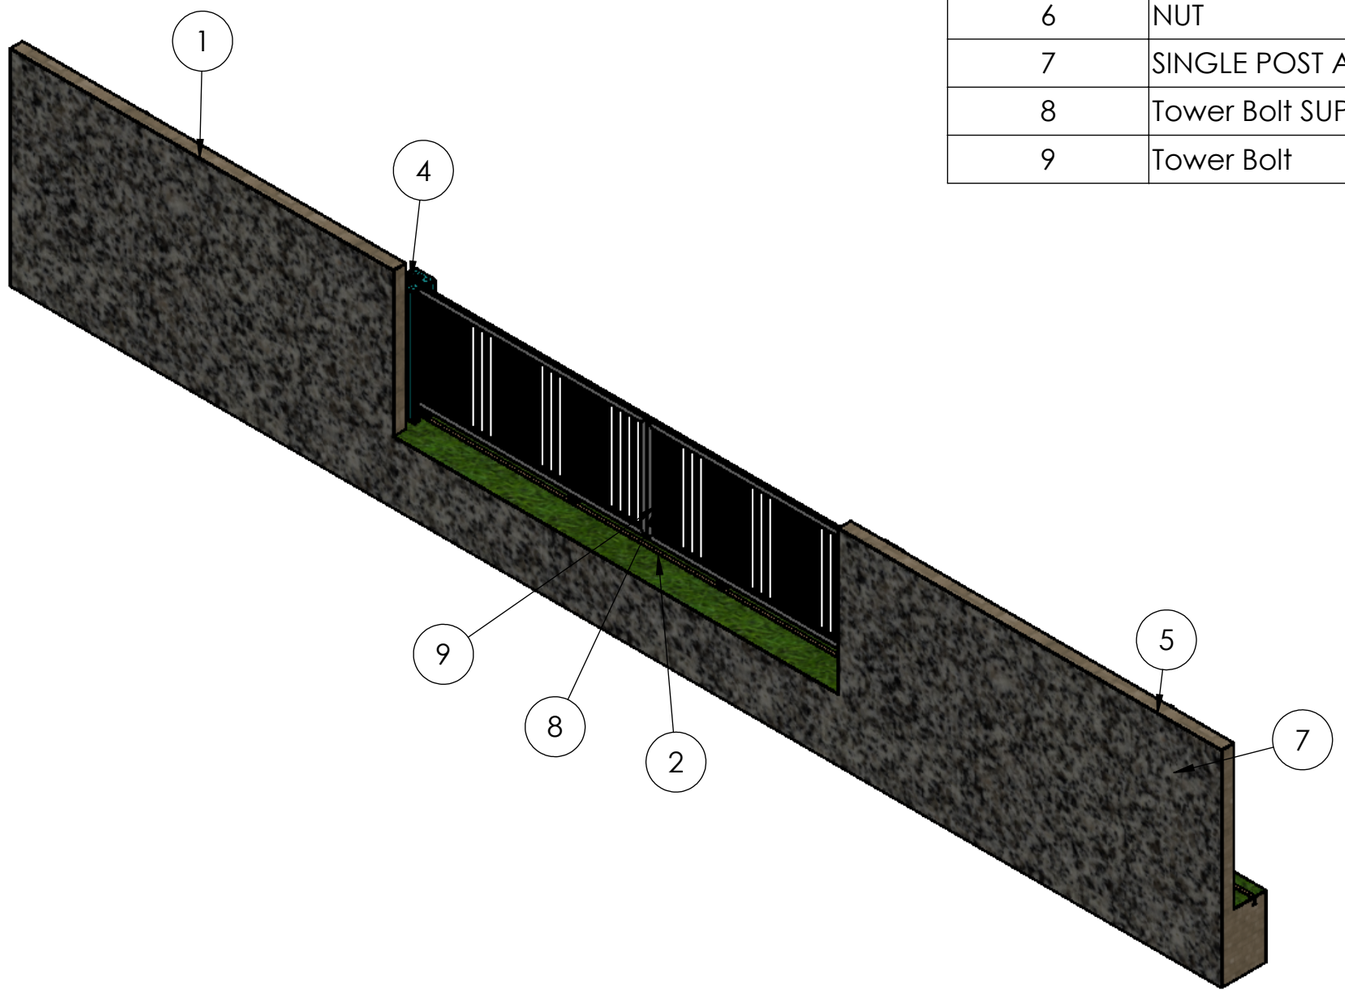


TITLE - GATE AUTOMATION				NIHVA TECHNOLOGIES PVT.LTD.PUNE Website - www.nihva.com
DWG NO - NTPL268-PM			QTY - 1	
	NAME	SIGNATURE	DATE	PROJECT NO - NTPL268-PM- AD
DRAWN	V.B.		03-03-2025	PRODUCT - BYPARTING SLIDING GATE
CHK'D	S.W.		03-03-2025	SITE LOCATION -
APPV'D	V.T.		03-03-2025	
if any queries contact - supportautomation@nihva.com				REVISION -
ALL DIMENSION ARE IN mm			A3	SCALE -

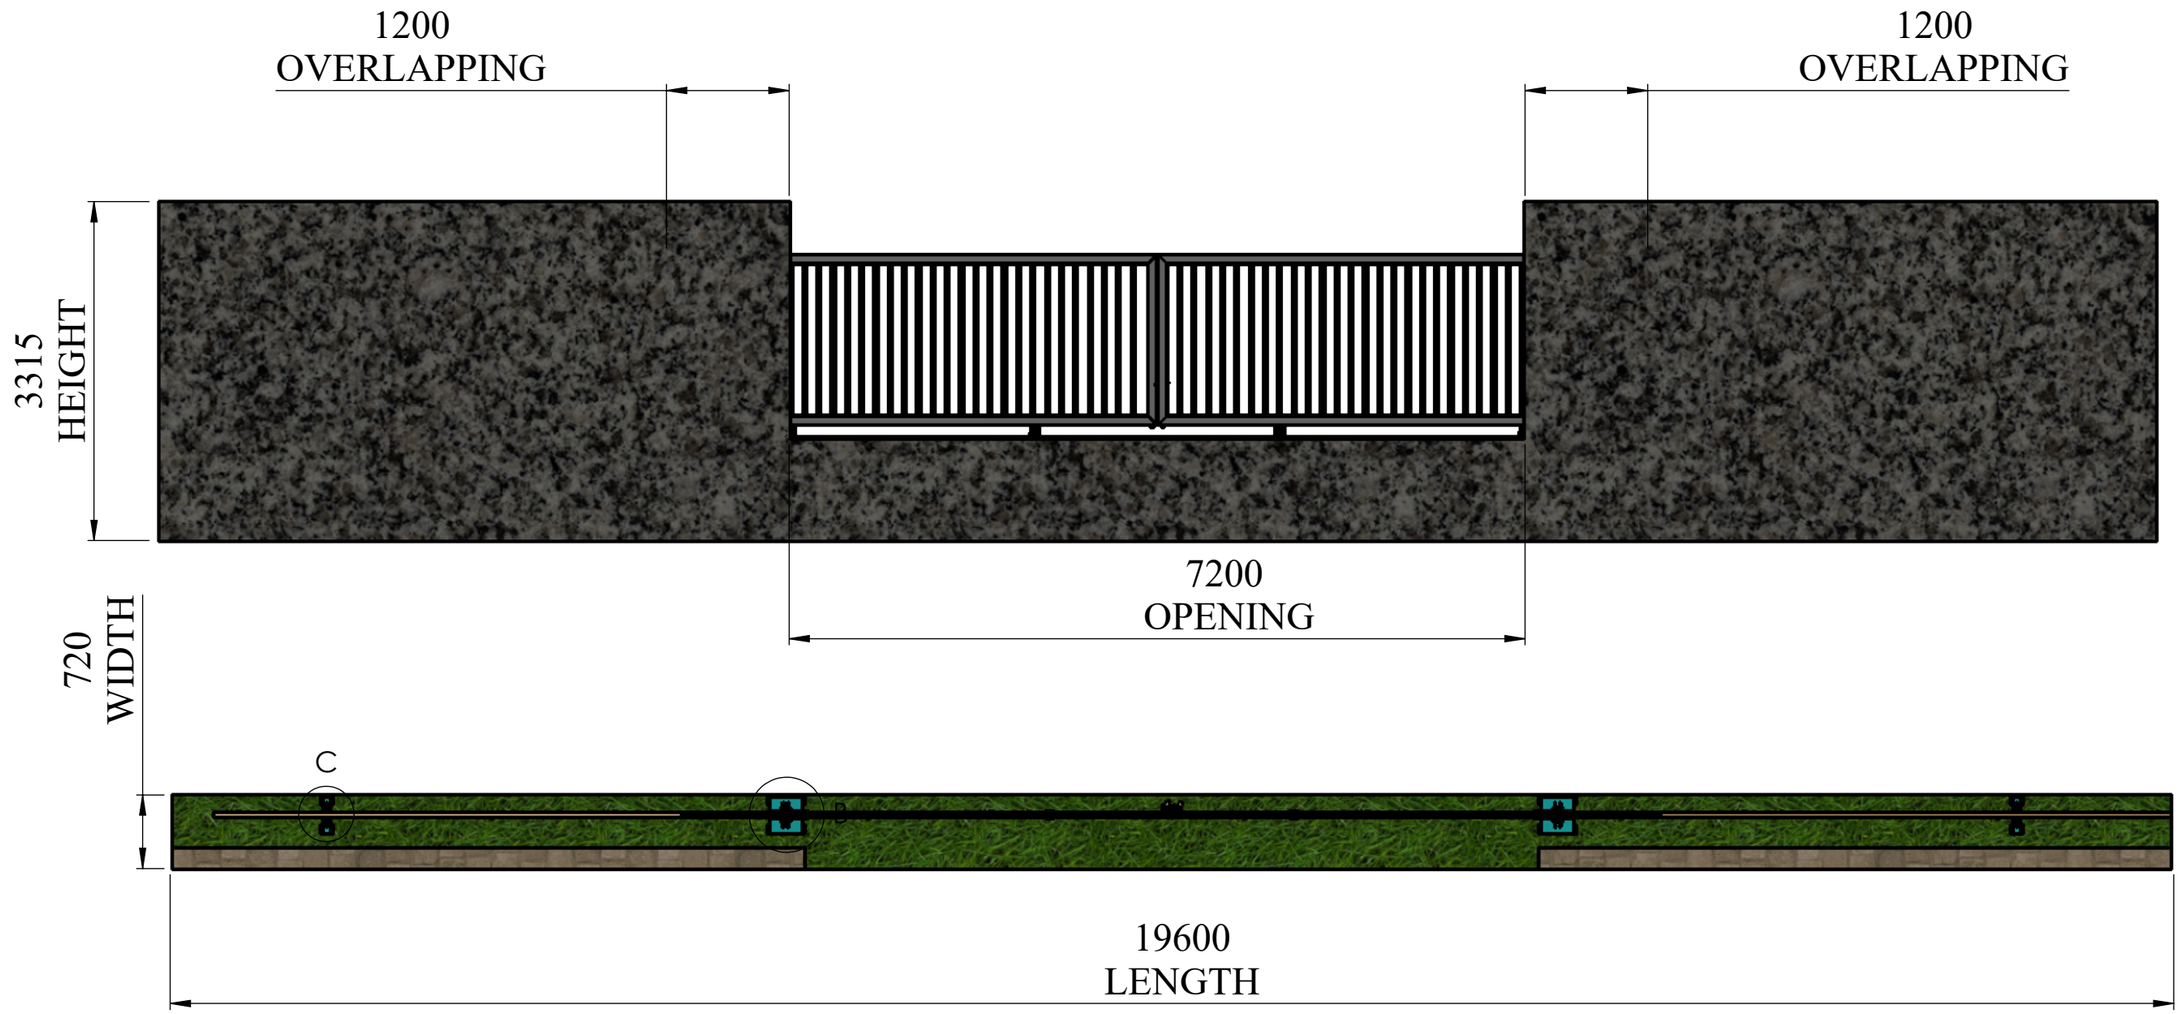

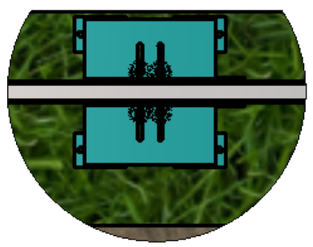

DETAIL B
SCALE 1 : 15

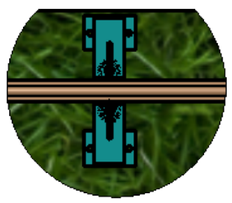


DETAIL C
SCALE 1 : 15


POST NO 1 AND NYLON ROLLER ASM

POST NO 2 AND NYLON ROLLER ASM

TITLE - GATE AUTOMATION				NIHVA TECHNOLOGIES PVT.LTD.PUNE Website - www.nihva.com
DWG NO - NTPL268-PM			QTY - 1	
	NAME	SIGNATURE	DATE	PROJECT NO - NTPL268-PM- AD
DRAWN	V.B.		03-03-2025	PRODUCT - BY PARTING SLIDING GATE
CHK'D	P.M.		03-03-2025	SITE LOCATION -
APPV'D	V.T.		03-03-2025	
if any queries contact - supportautomation@nihva.com				REVISION -
ALL DIMENSION ARE IN mm			A3	SCALE - SHEET 2 OF 20

ITEM NO.	PART NUMBER	DESCRIPTION	QTY.
1	SLIDING GATE	(L)- 4800 (H)- 1675	2
2	WHEEL AND PLATE ASM	4 INCH WHEEL	4

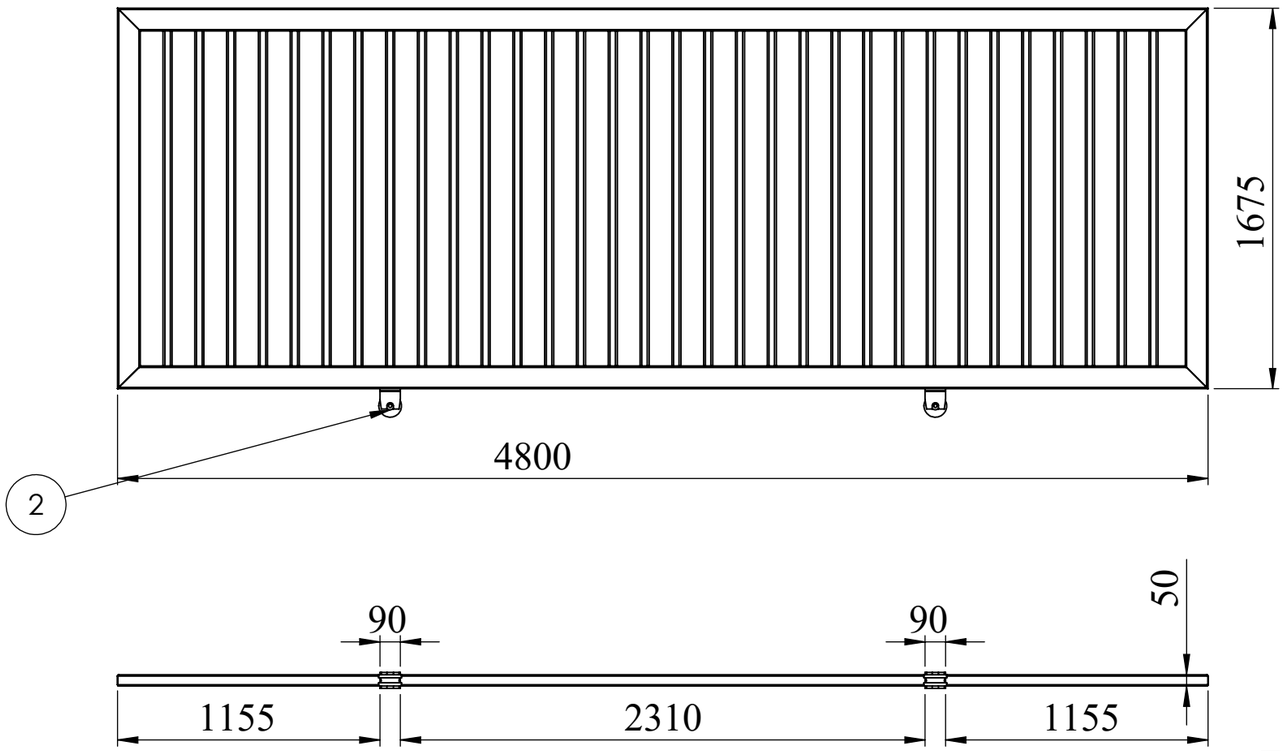


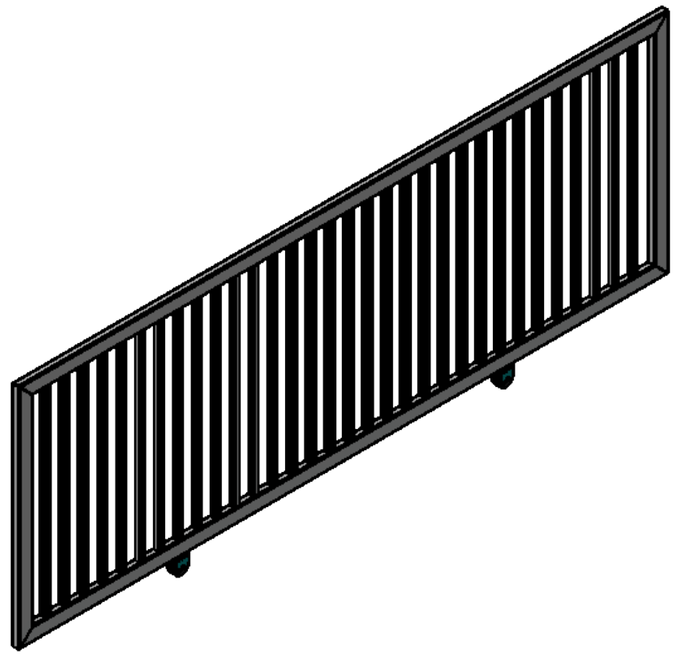


BY PARTING SLIDING LEAF:-2 NOS


TITLE - GATE AUTOMATION				NIHVA TECHNOLOGIES PVT.LTD.PUNE Website - www.nihva.com
DWG NO - NTPL268-PM			QTY - 1	
	NAME	SIGNATURE	DATE	PROJECT NO - NTPL268-PM- AD
DRAWN	S.W		03-03-2025	PRODUCT - BY PARTING SLIDING GATE
CHK'D	P.M.		03-03-2025	SITE LOCATION -
APPV'D	V.T.		03-03-2025	
if any queries contact - supportautomation@nihva.com				REVISION -
ALL DIMENSION ARE IN mm			A3	SCALE - SHEET 3 OF 20

ITEM NO.	PART NUMBER	DESCRIPTION	QTY.
1	SLIDING GATE	(L)- 4800 (H)- 1675	2
		TUBE, RECTANGULAR 100.000000 X 50.000000 X 3.00	4
		TUBE, RECTANGULAR 100.000000 X 50.000000 X 3.00	4
		TUBE, SQUARE 40.000000 X 40.000000 X 4.000000	64

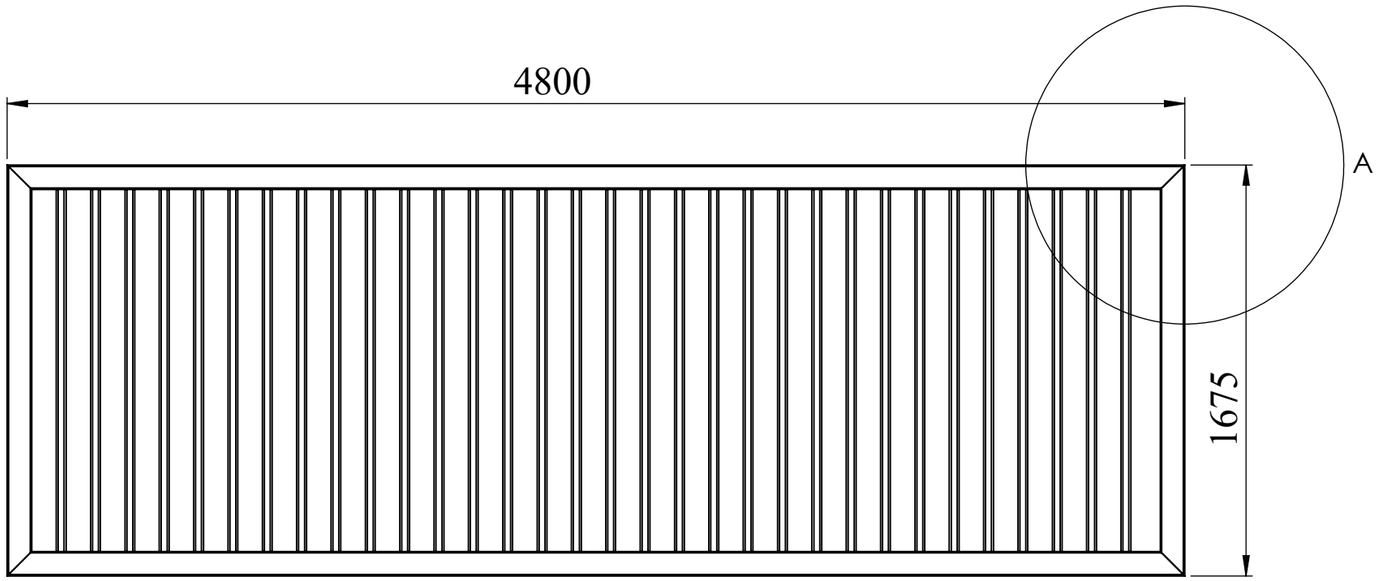

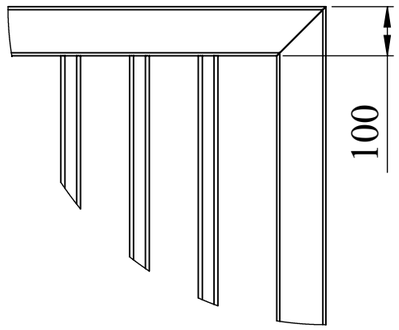

DETAIL A
SCALE 2 : 25

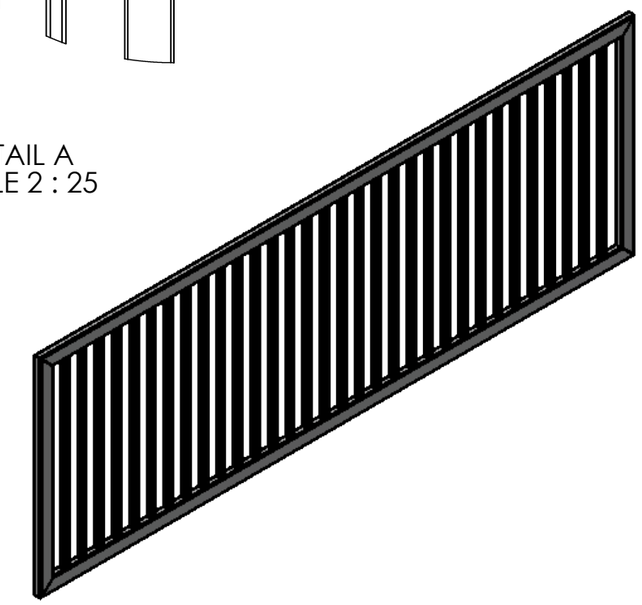






SQUARE TUBE
QTY:- 64 NOS FOR 2 LEAF

TITLE - GATE AUTOMATION				NIHVA TECHNOLOGIES PVT.LTD.PUNE
DWG NO - NTPL268-PM			QTY - 1	Website - www.nihva.com
	NAME	SIGNATURE	DATE	PROJECT NO - NTPL268-PM- AD
DRAWN	S.W		03-03-2025	PRODUCT - BY PARTING SLIDING GATE
CHK'D	P.M.		03-03-2025	SITE LOCATION -
APPV'D	V.T.		03-03-2025	
if any queries contact - supportautomation@nihva.com				REVISION -
ALL DIMENSION ARE IN mm			A3	SCALE - SHEET 4 OF 20

ITEM NO.	PART NUMBER	DESCRIPTION	QTY.
1	GUIDE PLATE	ID-14 (H)-94.91 (W)-10	2
2	SUPPORT PLATE	(L)-90 (W)- 70	1
3	WHEEL	OD-75.04 (W)-50	1

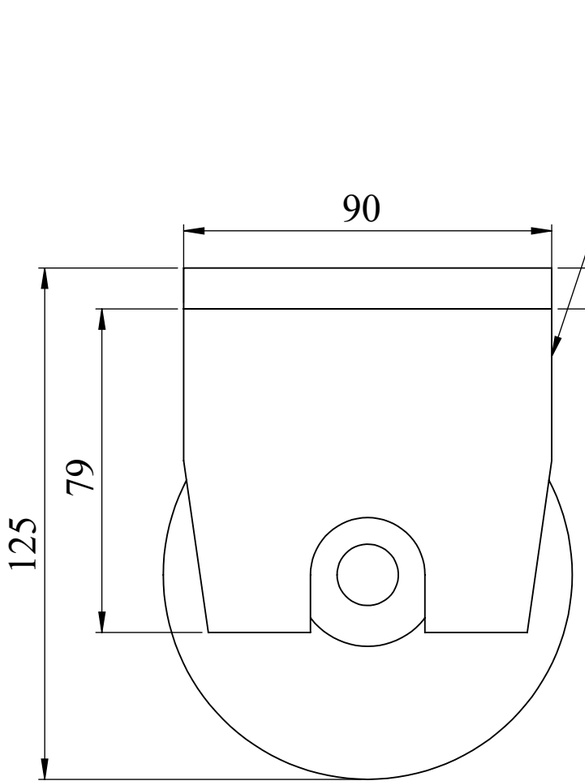

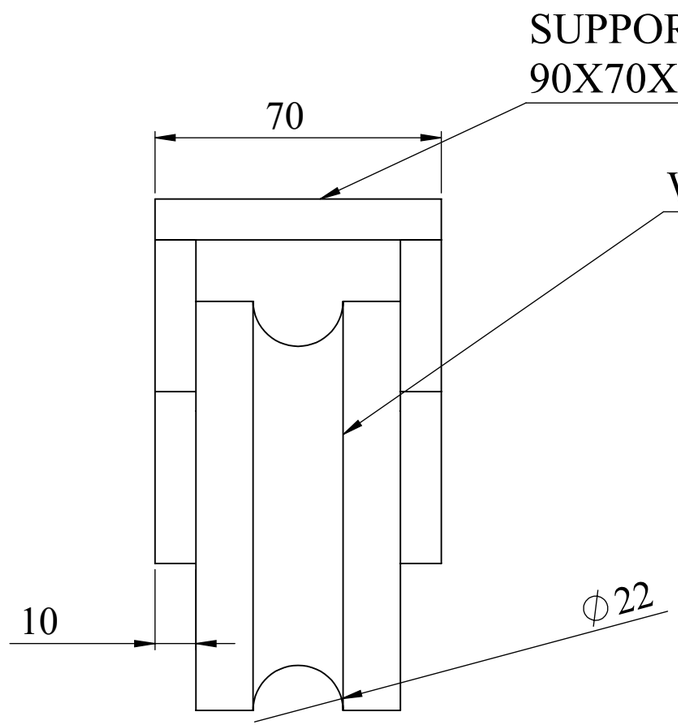


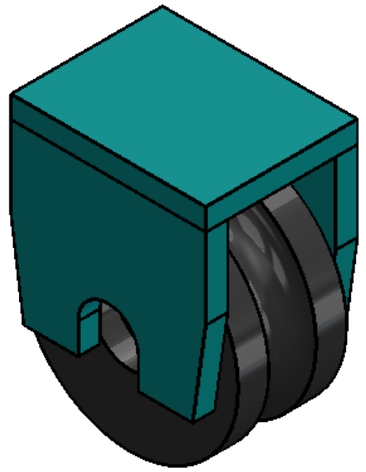



QTY- 4 NOS

TITLE - GATE AUTOMATION				NIHVA TECHNOLOGIES PVT.LTD.PUNE
DWG NO - NTPL268-PM			QTY - 1	Website - www.nihva.com
	NAME	SIGNATURE	DATE	PROJECT NO - NTPL268-PM- AD
DRAWN	V.B.		03-03-2025	PRODUCT - BY PARTING SLIDING GATE
CHK'D	P.M.		03-03-2025	SITE LOCATION -
APPV'D	V.T.		03-03-2025	
if any queries contact - supportautomation@nihva.com				REVISION -
ALL DIMENSION ARE IN mm			A3	SCALE - SHEET 5 OF 20

ITEM NO.	PART NUMBER	DESCRIPTION	QTY.
1	GUIDE PLATE	ID-14 (H)-94.91 (W)-10	8
		Sheet	1

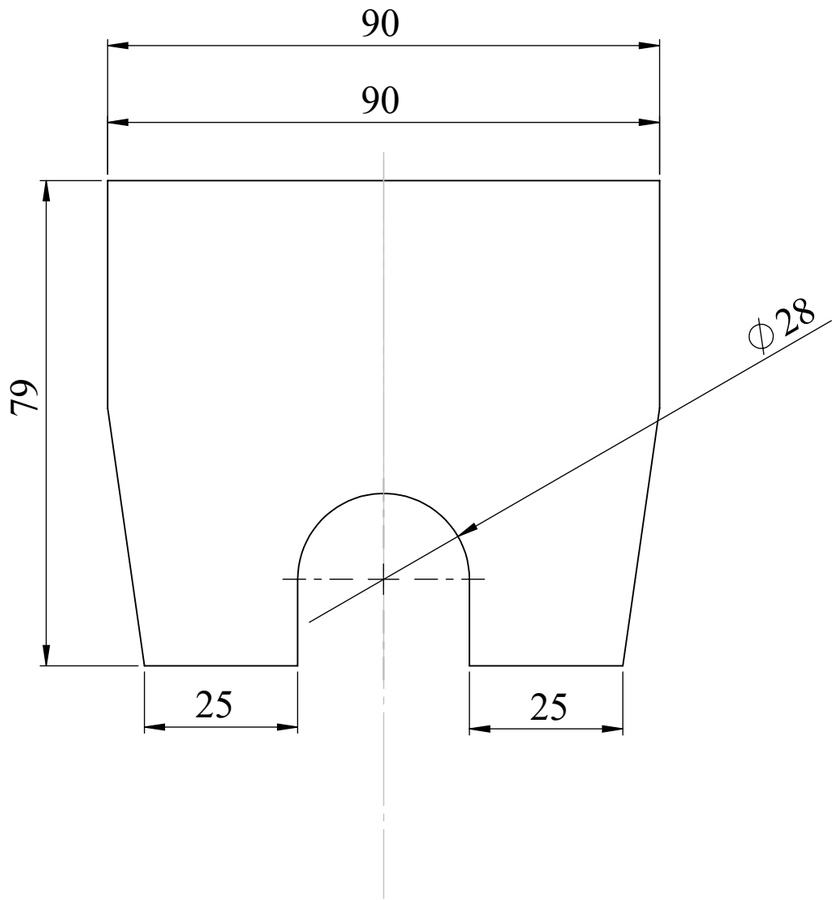

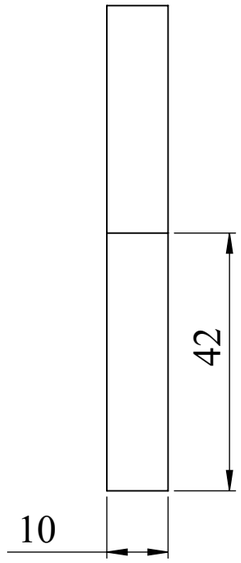


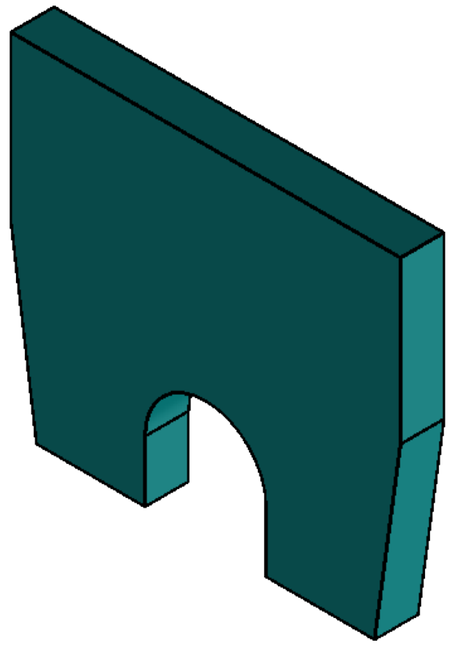


GUIDE PLATE

TITLE - GATE AUTOMATION				NIHVA TECHNOLOGIES PVT.LTD.PUNE Website - www.nihva.com
DWG NO - NTPL268-PM			QTY - 1	
	NAME	SIGNATURE	DATE	PROJECT NO - NTPL268-PM- AD
DRAWN	S.W		03-03-2025	PRODUCT - BY PARTING SLIDING GATE
CHK'D	P.M.		03-03-2025	SITE LOCATION -
APPV'D	V.T.		03-03-2025	
if any queries contact - supportautomation@nihva.com				REVISION -
ALL DIMENSION ARE IN mm			A3	SCALE - SHEET 6 OF 20

ITEM NO.	PART NUMBER	DESCRIPTION	QTY.
1	WHEEL	OD-75.04 (W)-50	4

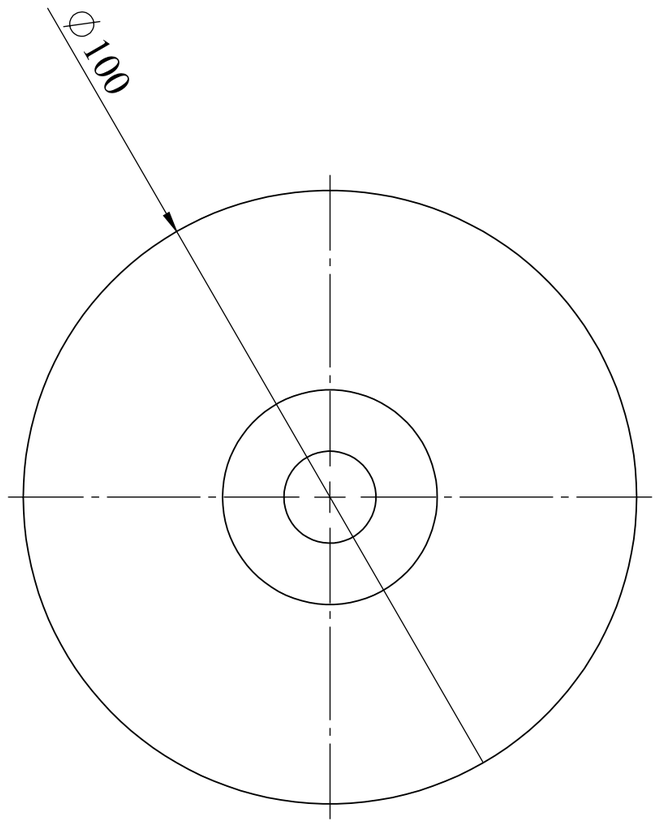

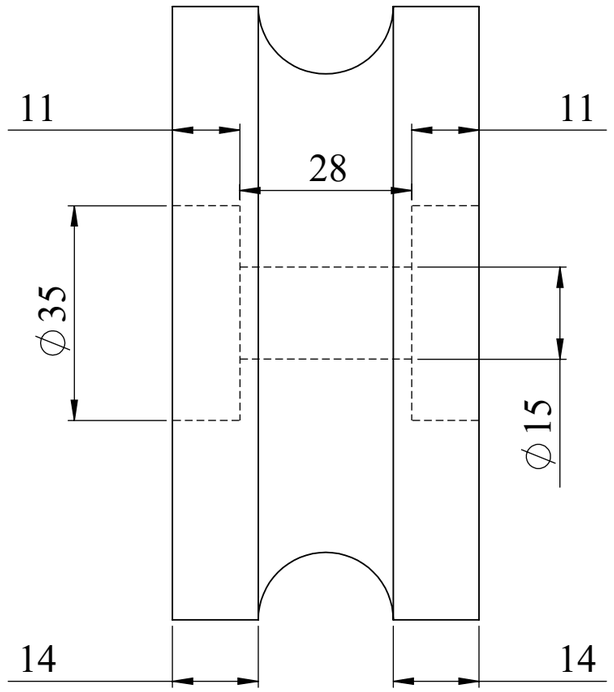






WHEEL

TITLE - GATE AUTOMATION				NIHVA TECHNOLOGIES PVT.LTD.PUNE
DWG NO - NTPL268-PM			QTY - 1	Website - www.nihva.com
	NAME	SIGNATURE	DATE	PROJECT NO - NTPL268-PM- AD
DRAWN	V.B.		03-03-2025	PRODUCT - BY PARTING SLIDING GATE
CHK'D	S.W.		03-03-2025	SITE LOCATION -
APPV'D	V.T.		03-03-2025	
if any queries contact - supportautomation@nihva.com				REVISION -
ALL DIMENSION ARE IN mm			A3	SCALE - SHEET 7 OF 20

ITEM NO.	PART NUMBER	DESCRIPTION	QTY.
1	TYPE3REF1nylon roller with bearing 43 final asm	STD	12
2	TYPE3REF1bolt	STD	12
3	NUT	STD	12

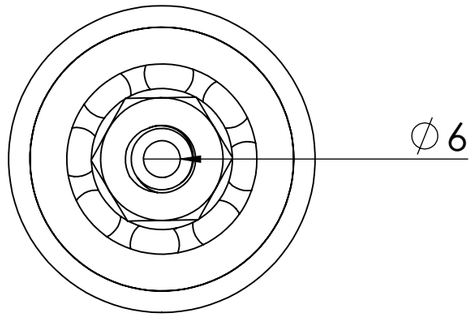

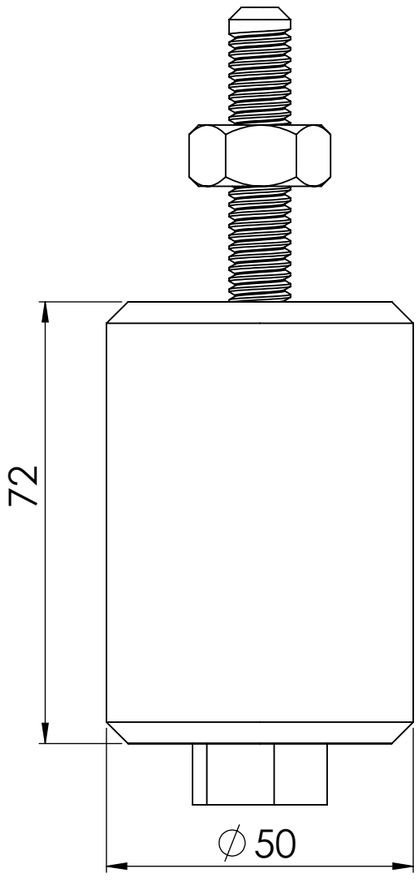

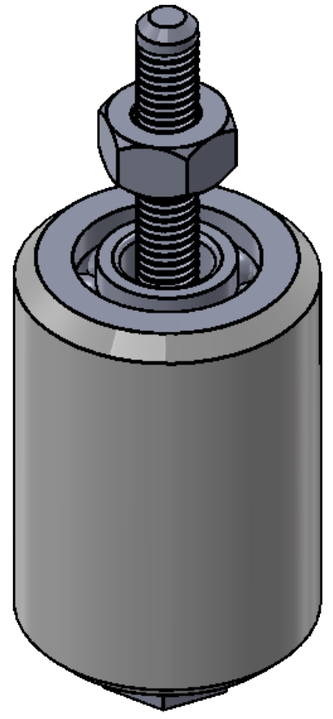



NYLON ROLLER ASM (STD)


QTY- 12 NOS

TITLE - GATE AUTOMATION				NIHVA TECHNOLOGIES PVT.LTD.PUNE Website - www.nihva.com
DWG NO - NTPL268-PM			QTY - 1	
	NAME	SIGNATURE	DATE	PROJECT NO - NTPL268-PM- AD
DRAWN	V.B.		03-03-2025	PRODUCT - BY PARTING SLIDING GATE
CHK'D	S.W.		03-03-2025	SITE LOCATION -
APPV'D	V.T.		03-03-2025	
if any queries contact - supportautomation@nihva.com				REVISION -
ALL DIMENSION ARE IN mm			A3	SCALE - SHEET 8 OF 20

ITEM NO.	PART NUMBER	DESCRIPTION	QTY.
1	TYPE31nylon roller with bearing 43		2
2	TYPE31nylon roller		1

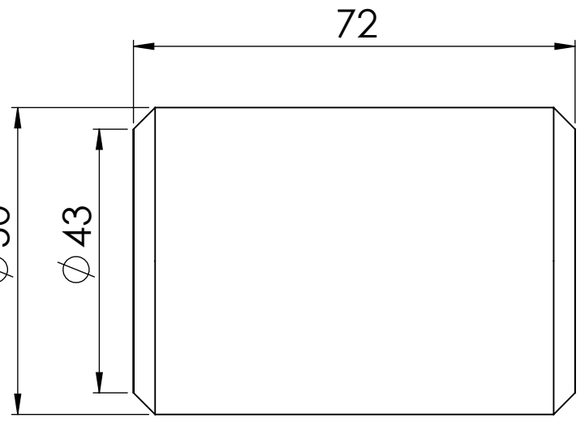

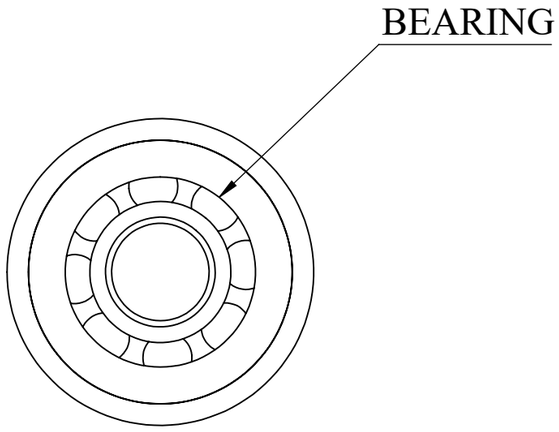


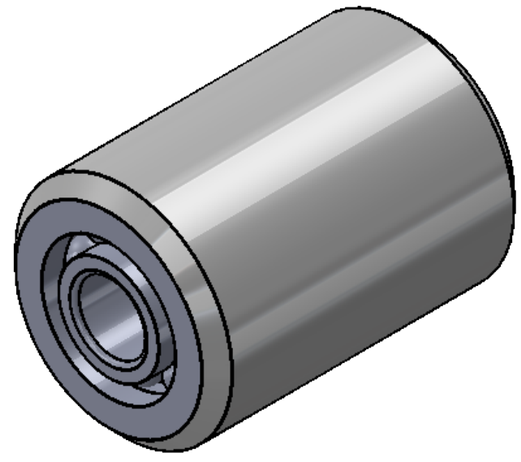


QTY:- 12 NOS


NYLON ROLLER


TITLE - RETRACTABLE ROOF				NIHVA TECHNOLOGIES PVT.LTD.PUNE Website - www.nihva.com
DWG NO - NTPL268-PM			QTY - 1	
	NAME	SIGNATURE	DATE	PROJECT NO - NTPL268-PM- AD
DRAWN	S.W		03-03-2025	PRODUCT - RETRACTABLE ROOF
CHK'D	P.M.		03-03-2025	SITE LOCATION - GUJARAT
APPV'D	V.T.		03-03-2025	
if any queries contact - supportautomation@nihva.com				REVISION -
ALL DIMENSION ARE IN mm			A3	SCALE -

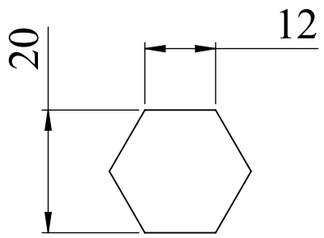

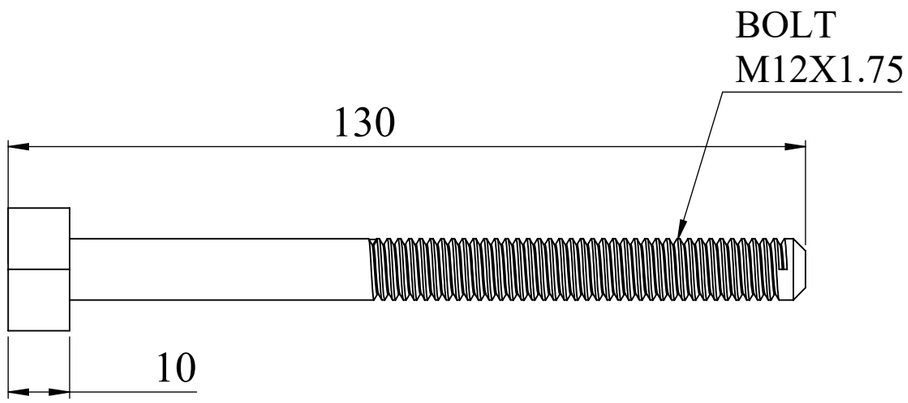

BOLT

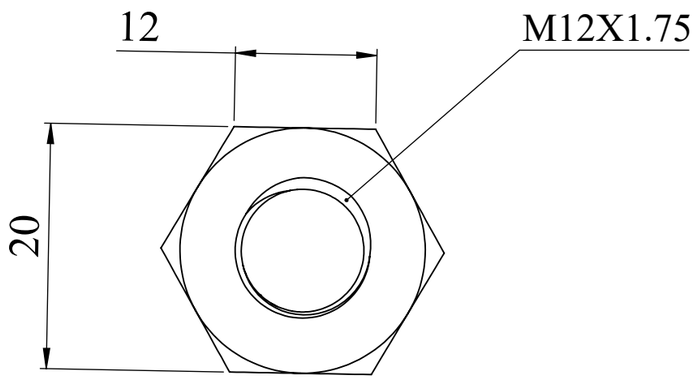

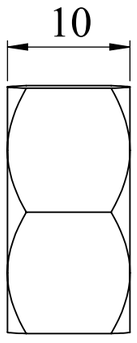



QTY- 12 NOS


NUT

TITLE - RETRACTABLE ROOF				NIHVA TECHNOLOGIES PVT.LTD.PUNE Website - www.nihva.com
DWG NO - NTPL268-PM			QTY - 1	
	NAME	SIGNATURE	DATE	PROJECT NO - NTPL268-PM- AD
DRAWN	S.W		03-03-2025	PRODUCT - RETRACTABLE ROOF
CHK'D	P.M.		03-03-2025	SITE LOCATION - GUJARAT
APPV'D	V.T.		03-03-2025	
if any queries contact - supportautomation@nihva.com				REVISION -
ALL DIMENSION ARE IN mm			A3	SCALE - SHEET 10 OF 20

ITEM NO.	PART NUMBER	DESCRIPTION	QTY.
1	HORIZONTAL PLATE	320X145X10	4
2	VERTICAL SQUARE TUBE	75x75x3	8
3	BOTTOM PLATE	125X85X10	8

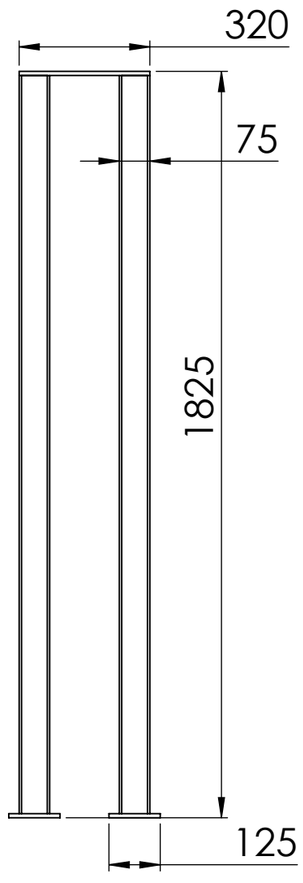

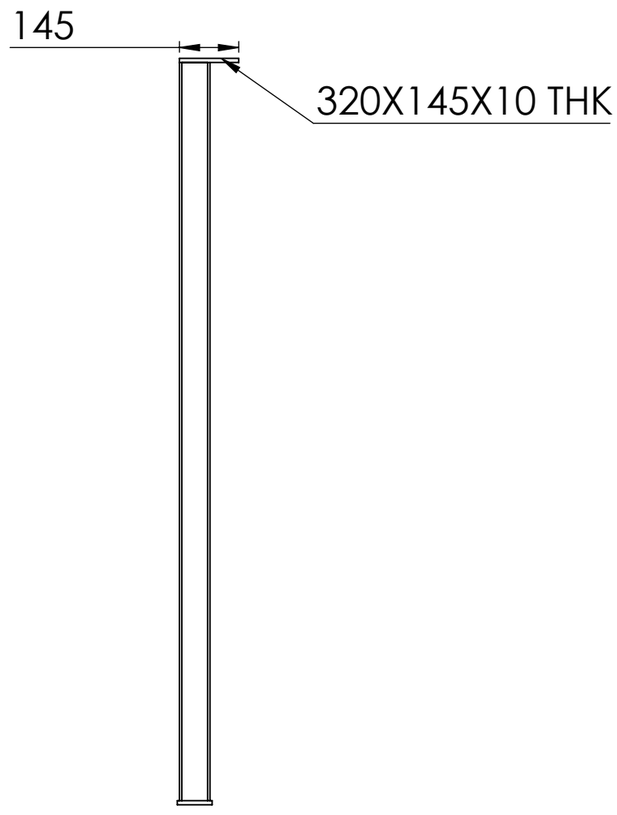

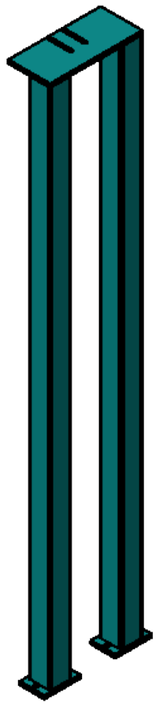



POST1 ASM


QTY- 4 NOS

TITLE - RETRACTABLE ROOF				NIHVA TECHNOLOGIES PVT.LTD.PUNE Website - www.nihva.com
DWG NO - NTPL268-PM			QTY - 1	
	NAME	SIGNATURE	DATE	PROJECT NO - NTPL268-PM- AD
DRAWN	S.W		03-03-2025	PRODUCT - RETRACTABLE ROOF
CHK'D	P.M.		03-03-2025	SITE LOCATION - GUJARAT
APPV'D	V.T.		03-03-2025	
if any queries contact - supportautomation@nihva.com				REVISION -
ALL DIMENSION ARE IN mm			A3	SCALE - SHEET 11 OF 20

ITEM NO.	PART NUMBER	DESCRIPTION	QTY.
1	HORIZONTAL PLATE	320X145X10	4

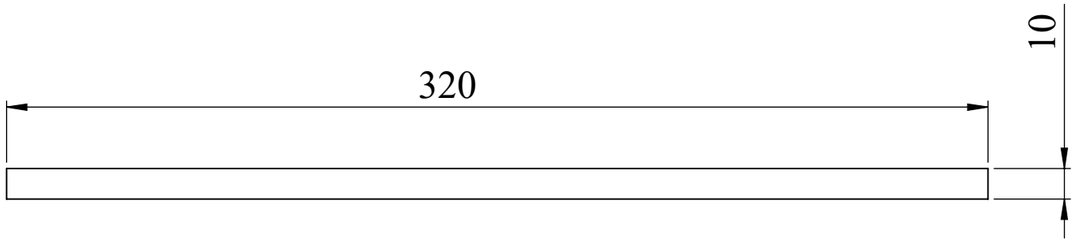

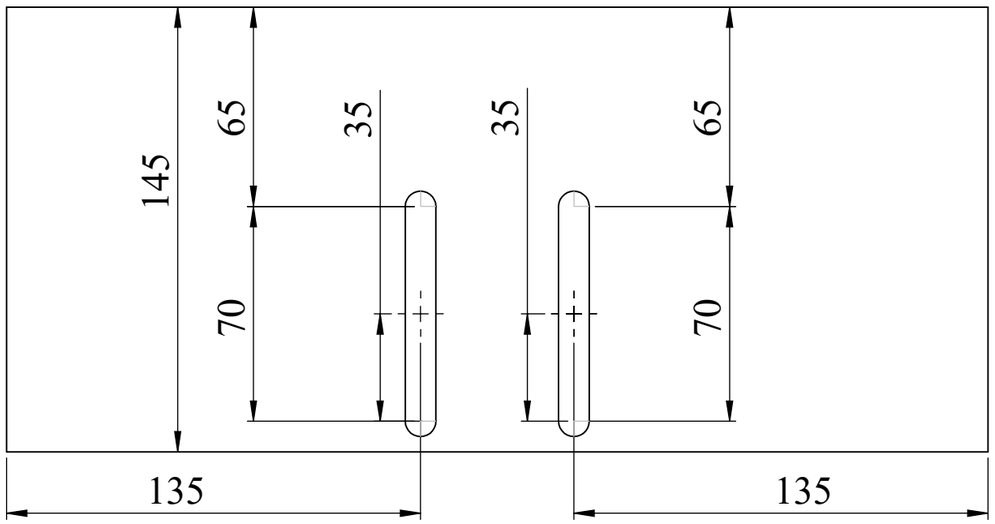

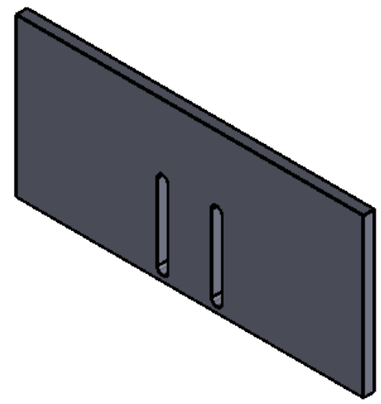



NOTE
POST 1 ROLLER SUPPORT PLATE
320X145X10MM THK


QTY- 4 NOS

TITLE - GATE AUTOMATION				NIHVA TECHNOLOGIES PVT.LTD.PUNE Website - www.nihva.com
DWG NO - NTPL268-PM			QTY - 1	
	NAME	SIGNATURE	DATE	PROJECT NO - NTPL268-PM- AD
DRAWN	V.B.		03-03-2025	PRODUCT - BY PARTING SLIDING GATE
CHK'D	S.W.		03-03-2025	SITE LOCATION -
APPV'D	V.T.		03-03-2025	
if any queries contact - supportautomation@nihva.com				REVISION -00
ALL DIMENSION ARE IN mm			A3	SCALE - SHEET 12 OF 20

ITEM NO.	PART NUMBER	DESCRIPTION	QTY.
1	BOTTOM PLATE FOR POST	125X85X10	12

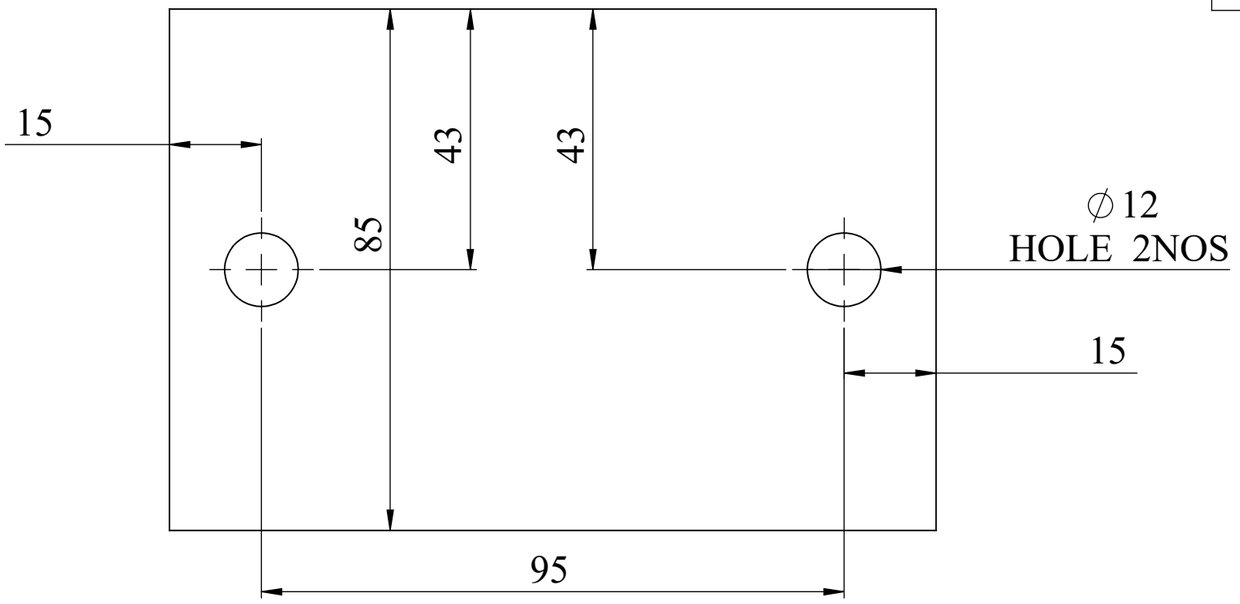

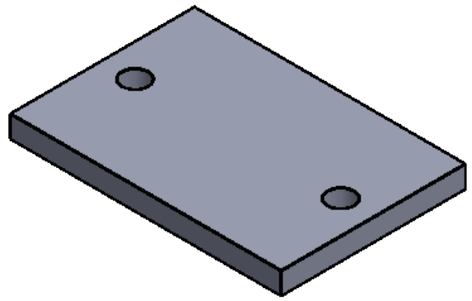

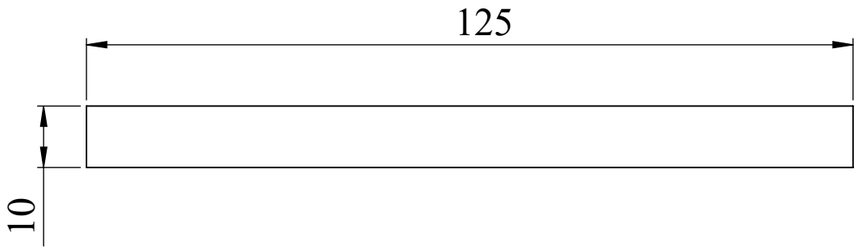


NOTE
POST BOTTOM PLATE
MS 117X85X10 THK


THIS BOTTOM PLATE
USED SAME FOR POST 2

QTY:- 12 NOS

TITLE - GATE AUTOMATION				NIHVA TECHNOLOGIES PVT.LTD.PUNE
DWG NO - NTPL268-PM			QTY - 1	Website - www.nihva.com
	NAME	SIGNATURE	DATE	PROJECT NO - NTPL268-PM- AD
DRAWN	V.B.		03-03-2025	PRODUCT - BYPARTING SLIDING GATE
CHK'D	S.W.		03-03-2025	SITE LOCATION -
APPV'D	V.T.		03-03-2025	
if any queries contact - supportautomation@nihva.com				REVISION -
ALL DIMENSION ARE IN mm			A3	SCALE - SHEET 13 OF 20

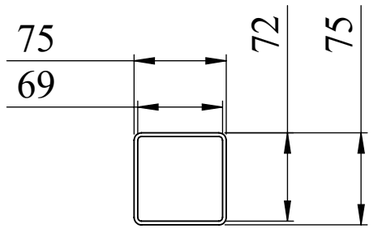

ITEM NO.	PART NUMBER	DESCRIPTION	QTY.
1	VERTICAL SQUARE TUBE	75x75x3	12
		TUBE, SQUARE 75.000000 X 75.000000 X 3.000000	1

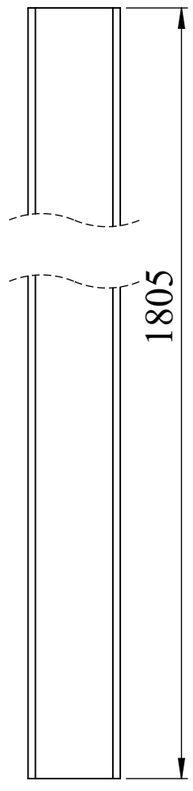




NOTE
POST 1 VERTICAL SUPPORT TUBE
MS 75X75X3 THK
THIS SQUARE TUBE USED FOR POST 2

QTY-12 NOS

TITLE - GATE AUTOMATION				NIHVA TECHNOLOGIES PVT.LTD.PUNE Website - www.nihva.com
DWG NO - NTPL268-PM				
	NAME	SIGNATURE	DATE	PROJECT NO - NTPL268-PM- AD
DRAWN	S.W		03-03-2025	PRODUCT - BY PARTING SLIDING GATE
CHK'D	P.M.		03-03-2025	SITE LOCATION -
APPV'D	V.T.		03-03-2025	
if any queries contact - supportautomation@nihva.com				REVISION -00 / QTY - 1
ALL DIMENSION ARE IN mm			A3	SCALE - / SHEET 14 OF 20

ITEM NO.	PART NUMBER	DESCRIPTION	QTY.
1	SINGLE plate for post 2	145X75X10	4
2	SINGLE1square tube for post 2	75X75X6	4
3	SINGLE1bottom plate for post 2	117X85X10	4

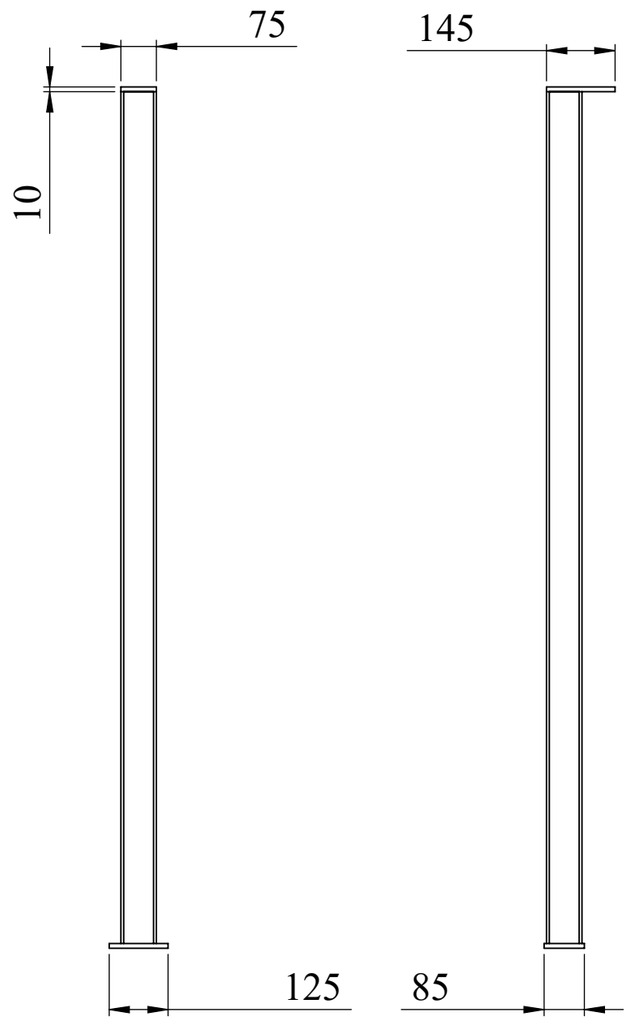





QTY- 4

POST 2 ASM

TITLE - GATE AUTOMATION				NIHVA TECHNOLOGIES PVT.LTD.PUNE Website - www.nihva.com
DWG NO - NTPL268-PM				
	NAME	SIGNATURE	DATE	PROJECT NO - NTPL268-PM- AD
DRAWN	V.B.		03-03-2025	PRODUCT - BY PARTING SLIDING GATE
CHK'D	S.W.		03-03-2025	SITE LOCATION -
APPV'D	V.T.		03-03-2025	
if any queries contact - supportautomation@nihva.com				REVISION - / QTY - 1
ALL DIMENSION ARE IN mm			A3	SCALE - / SHEET 15 OF 20

ITEM NO.	PART NUMBER	DESCRIPTION	QTY.
1	SINGLE plate for post 2	145X75X10	4

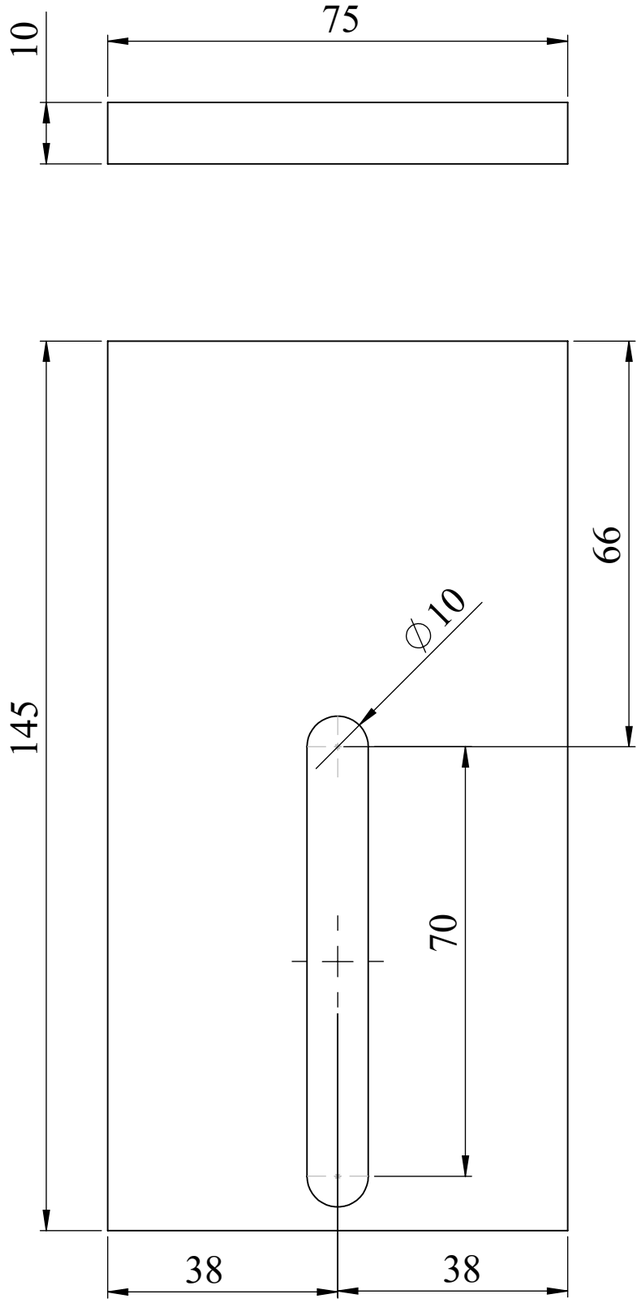


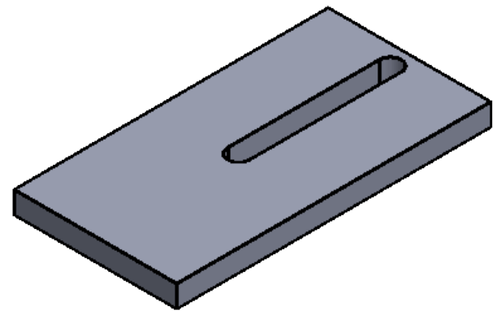



NOTE
POST 2 ROLLER SUPPORT PLATE
145X75X10 THK

TITLE - GATE AUTOMATION				NIHVA TECHNOLOGIES PVT.LTD.PUNE Website - www.nihva.com
DWG NO - NTPL268-PM			QTY - 1	
	NAME	SIGNATURE	DATE	PROJECT NO - NTPL268-PM- AD
DRAWN	S.W		03-03-2025	PRODUCT - BY PARTING SLIDING GATE
CHK'D	P.M.		03-03-2025	SITE LOCATION -
APPV'D	V.T.		03-03-2025	
if any queries contact - supportautomation@nihva.com				REVISION -00
ALL DIMENSION ARE IN mm			A3	SCALE - SHEET 16 OF 20


ITEM NO.	PART NUMBER	DESCRIPTION	QTY.
1	EN 8 BAR AND ISMB 1	(L) - 19200	1
		SB BEAM 100.000000 X 8	1
			1

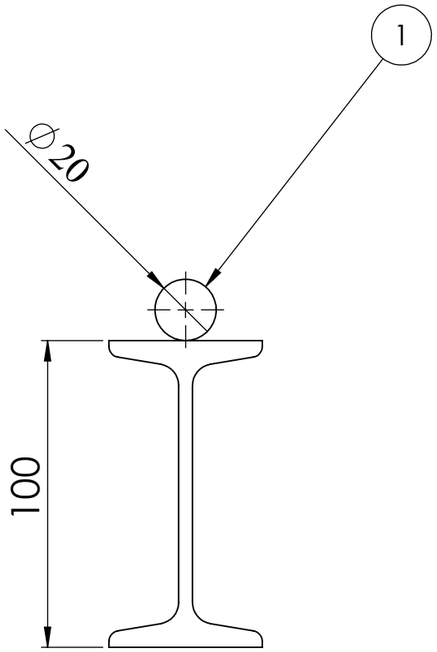

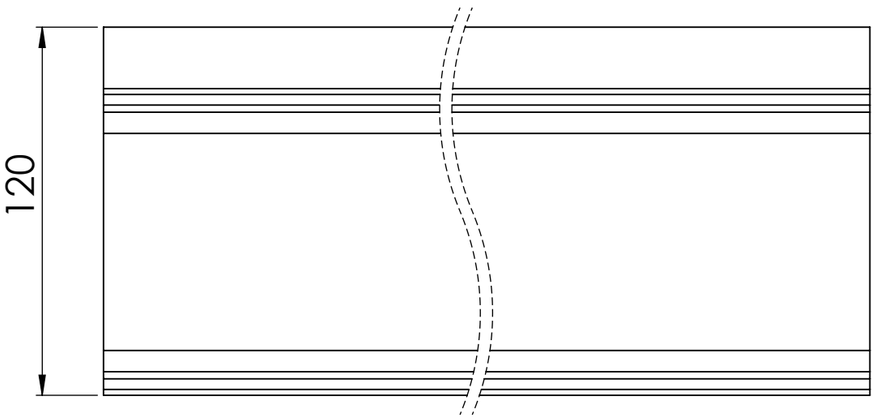


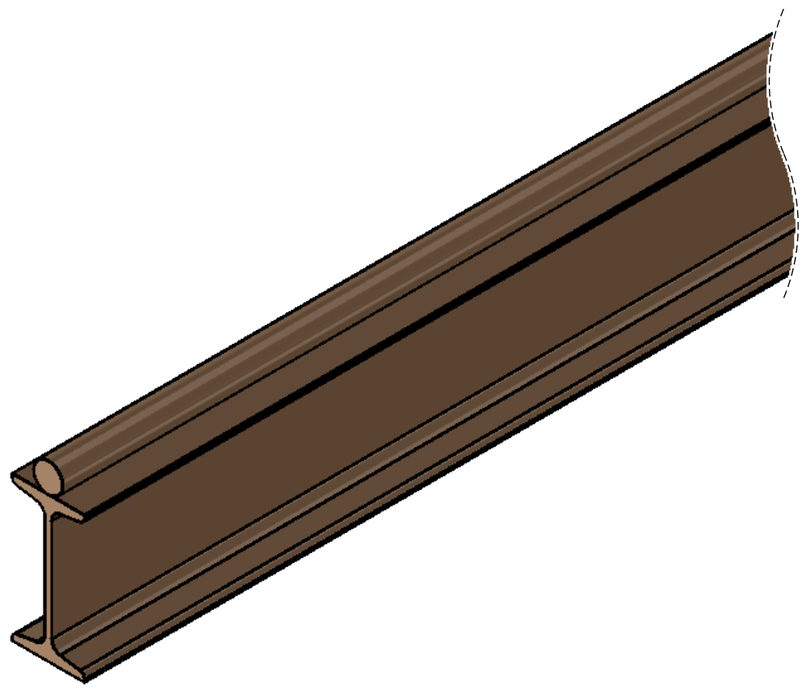

TITLE - GATE AUTOMATION				NIHVA TECHNOLOGIES PVT.LTD.PUNE Website - www.nihva.com
DWG NO - NTPL268-PM				
	NAME	SIGNATURE	DATE	PROJECT NO - NTPL268-PM- AD
DRAWN	V.B.		03-03-2025	PRODUCT - BY PARTING SLIDING GATE
CHK'D	S.W.		03-03-2025	SITE LOCATION -
APPV'D	V.T.		03-03-2025	
if any queries contact - supportautomation@nihva.com				REVISION -00 / QTY - 1
ALL DIMENSION ARE IN mm			A3	SCALE - / SHEET 17 OF 20

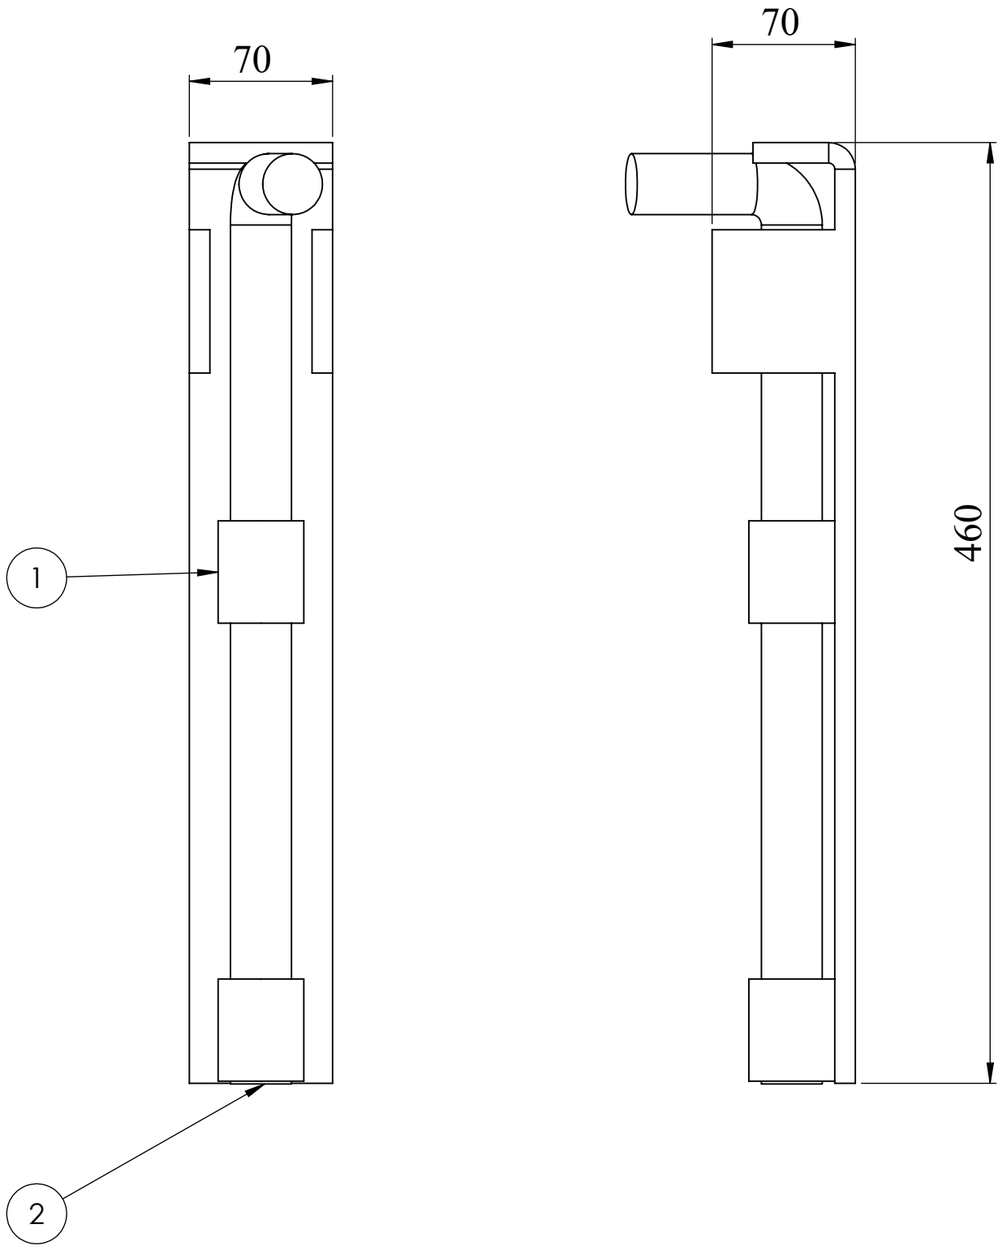

ITEM NO.	PART NUMBER	DESCRIPTION	QTY.
1	Tower Bolt SUPPORT	(L)-70 (H)-460	2
2	Tower Bolt	DIA- 29.8	2

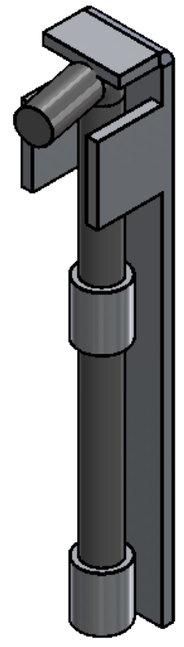



QTY- 2 NOS


TOWER BOLT


TITLE - GATE AUTOMATION				NIHVA TECHNOLOGIES PVT.LTD.PUNE Website - www.nihva.com
DWG NO - NTPL268-PM			QTY - 1	
	NAME	SIGNATURE	DATE	PROJECT NO - NTPL268-PM- AD
DRAWN	V.B.		03-03-2025	PRODUCT - BYPARTING SLIDING GATE
CHK'D	S.W.		03-03-2025	SITE LOCATION -
APPV'D	V.T.		03-03-2025	
if any queries contact - supportautomation@nihva.com				REVISION -00
ALL DIMENSION ARE IN mm			A3	SCALE - SHEET 18 OF 20

ITEM NO.	PART NUMBER	DESCRIPTION	QTY.
1	Tower Bolt SUPPORT	(L)-70 (H)-460	2

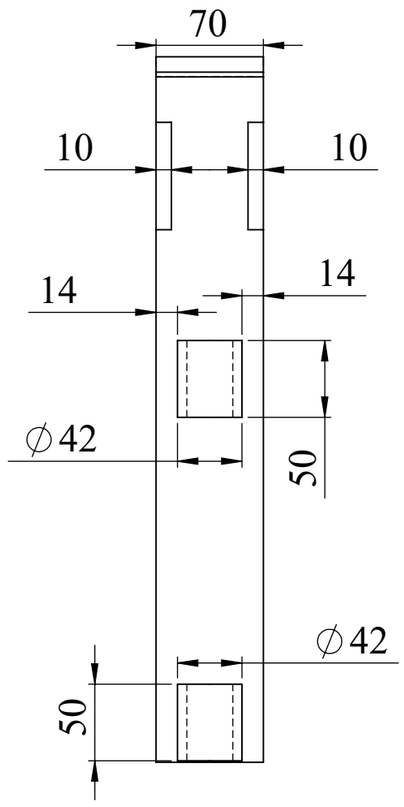


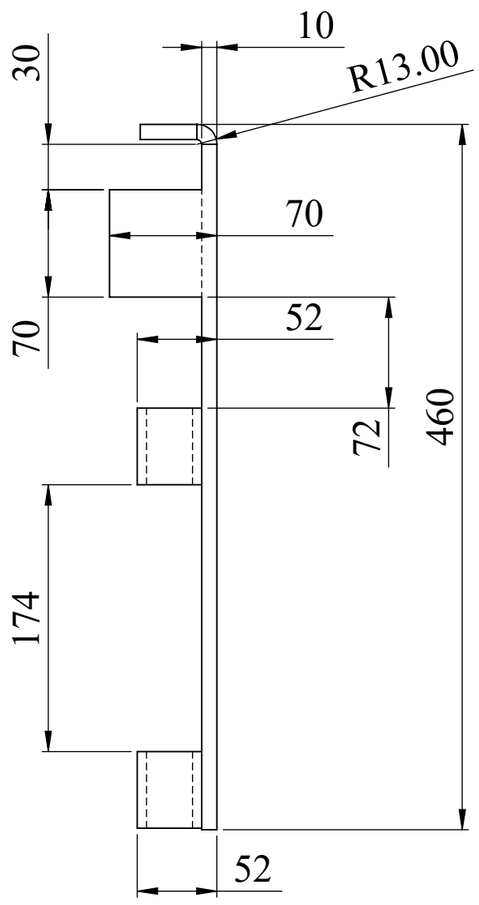

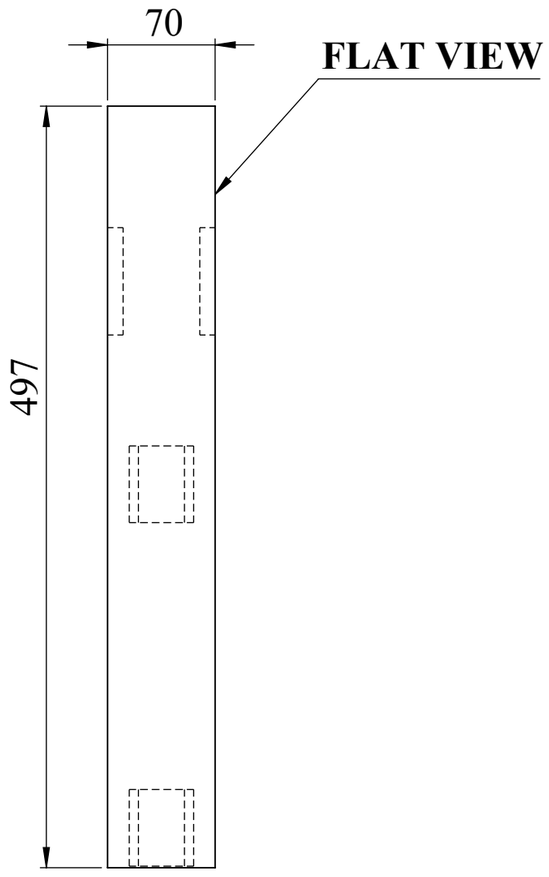

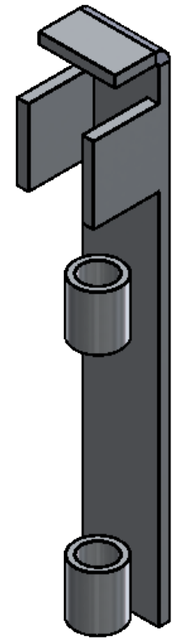


TOWER BOLT SUPPORT

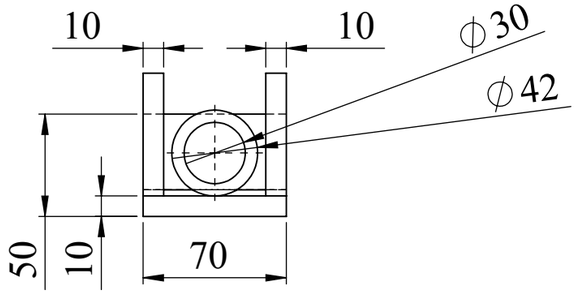


QTY- 2 NOS

TITLE - GATE AUTOMATION				NIHVA TECHNOLOGIES PVT.LTD.PUNE
DWG NO - NTPL268-PM			QTY - 1	Website - www.nihva.com
	NAME	SIGNATURE	DATE	PROJECT NO - NTPL268-PM- AD
DRAWN	V.B.		03-03-2025	PRODUCT - BYPARTING SLIDING GATE
CHK'D	S.W.		03-03-2025	SITE LOCATION -
APPV'D	V.T.		03-03-2025	
if any queries contact - supportautomation@nihva.com				REVISION -00
ALL DIMENSION ARE IN mm			A3	SCALE - SHEET 19 OF 20

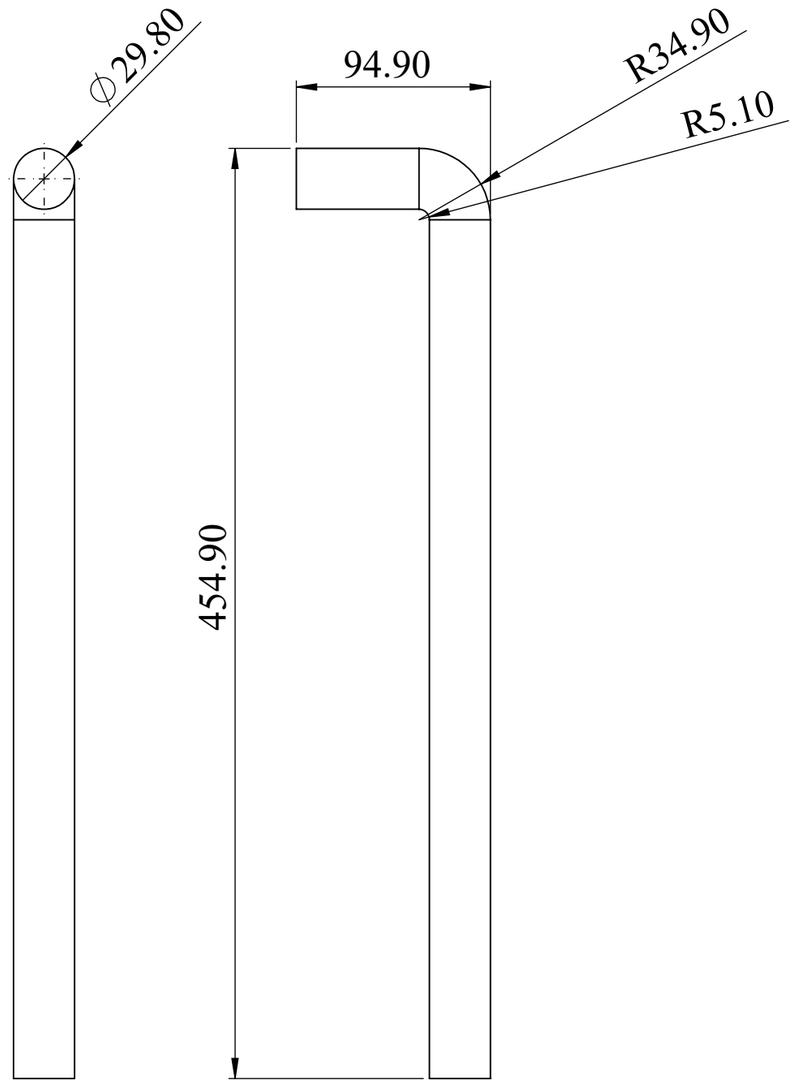

ITEM NO.	PART NUMBER	DESCRIPTION	QTY.
1	Tower Bolt	DIA- 29.8	2

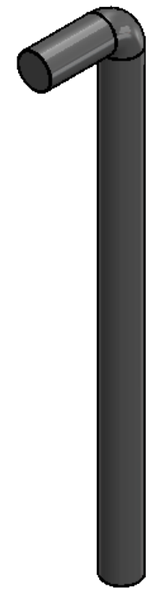

TOWER BOLT

QTY-2 NOS

TITLE - GATE AUTOMATION				NIHVA TECHNOLOGIES PVT.LTD.PUNE Website - www.nihva.com
DWG NO - NTPL268-PM			QTY - 1	
	NAME	SIGNATURE	DATE	PROJECT NO - NTPL268-PM- AD
DRAWN	V.B.		03-03-2025	PRODUCT - BY PARTING SLIDING GATE
CHK'D	S.W.		03-03-2025	SITE LOCATION -
APPV'D	V.T.		03-03-2025	
if any queries contact - supportautomation@nihva.com				REVISION -
ALL DIMENSION ARE IN mm			A3	SCALE - SHEET 20 OF 20