


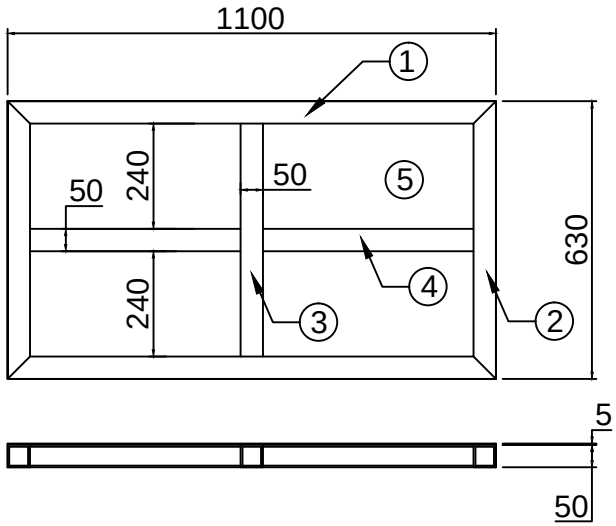


| SR NO | DESCRIPTION | SPECIFICATION | QTY |
|---|---|---|---|
| 11 | PLAIN SHEET | 1050 X 5 THK X 1100L | 1 NO |
| 10 | ISMC | 100 X 50 X 850L | 1 NO |
| 9 | ISMC | 100 X 50 X 545L | 4 NOS |
| 8 | ISMC | 100 X 50 X 400L | 2 NOS |
| 7 | ISMC | 100 X 50 X 1050L | 2 NOS |
| 6 | ISMC | 100 X 50 X 1100L | 2 NOS |
| 5 | PLAIN SHEET | 630 X 5 X 1100L | 1 NO |
| 4 | SQ. TUBE | 50 X 50 X 4 X 475L | 2 NOS |
| 3 | SQ. TUBE | 50 X 50 X 4 X 530L | 1 NO |
| 2 | SQ. TUBE | 50 X 50 X 4 X 630L | 2 NOS |
| 1 | SQ. TUBE | 50 X 50 X 4 X 1100L | 2 NOS |

This drawing & design is the property of NIHVA TECHNOLOGIES. Not to be sold or copied to any other concern.

TITLE: DOORS

NIHVA TECHNOLOGIES PVT. LTD.
NIHVA TECHNOLOGIES PVT. PUNE
Tel : 020 66304033
Email:- info@nihva.com
Website:- www.nihva.com
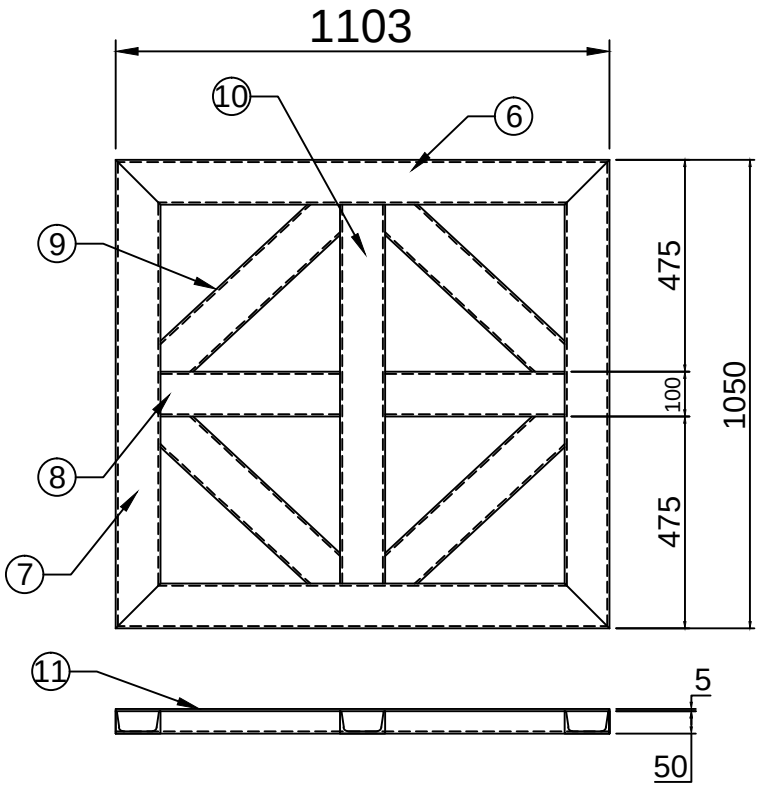
| | NAME | SIGN | DATE |
|---|---|---|---|
| DRAWN | P.A | | 22.10.2019 |
| CHECK | G.J | | 22.10.2019 |
| APPRD. | | | |

CLIENT -
PROJECT -
SITE LOCATION -
If any queries contact : design@nihva.com
DWG. NO. :NIHVA/19-20/VDR/194
REV- R00
ALL DIMENSION ARE IN mm
SCALE: NTS
WT:
SHEET: 01 OF 01