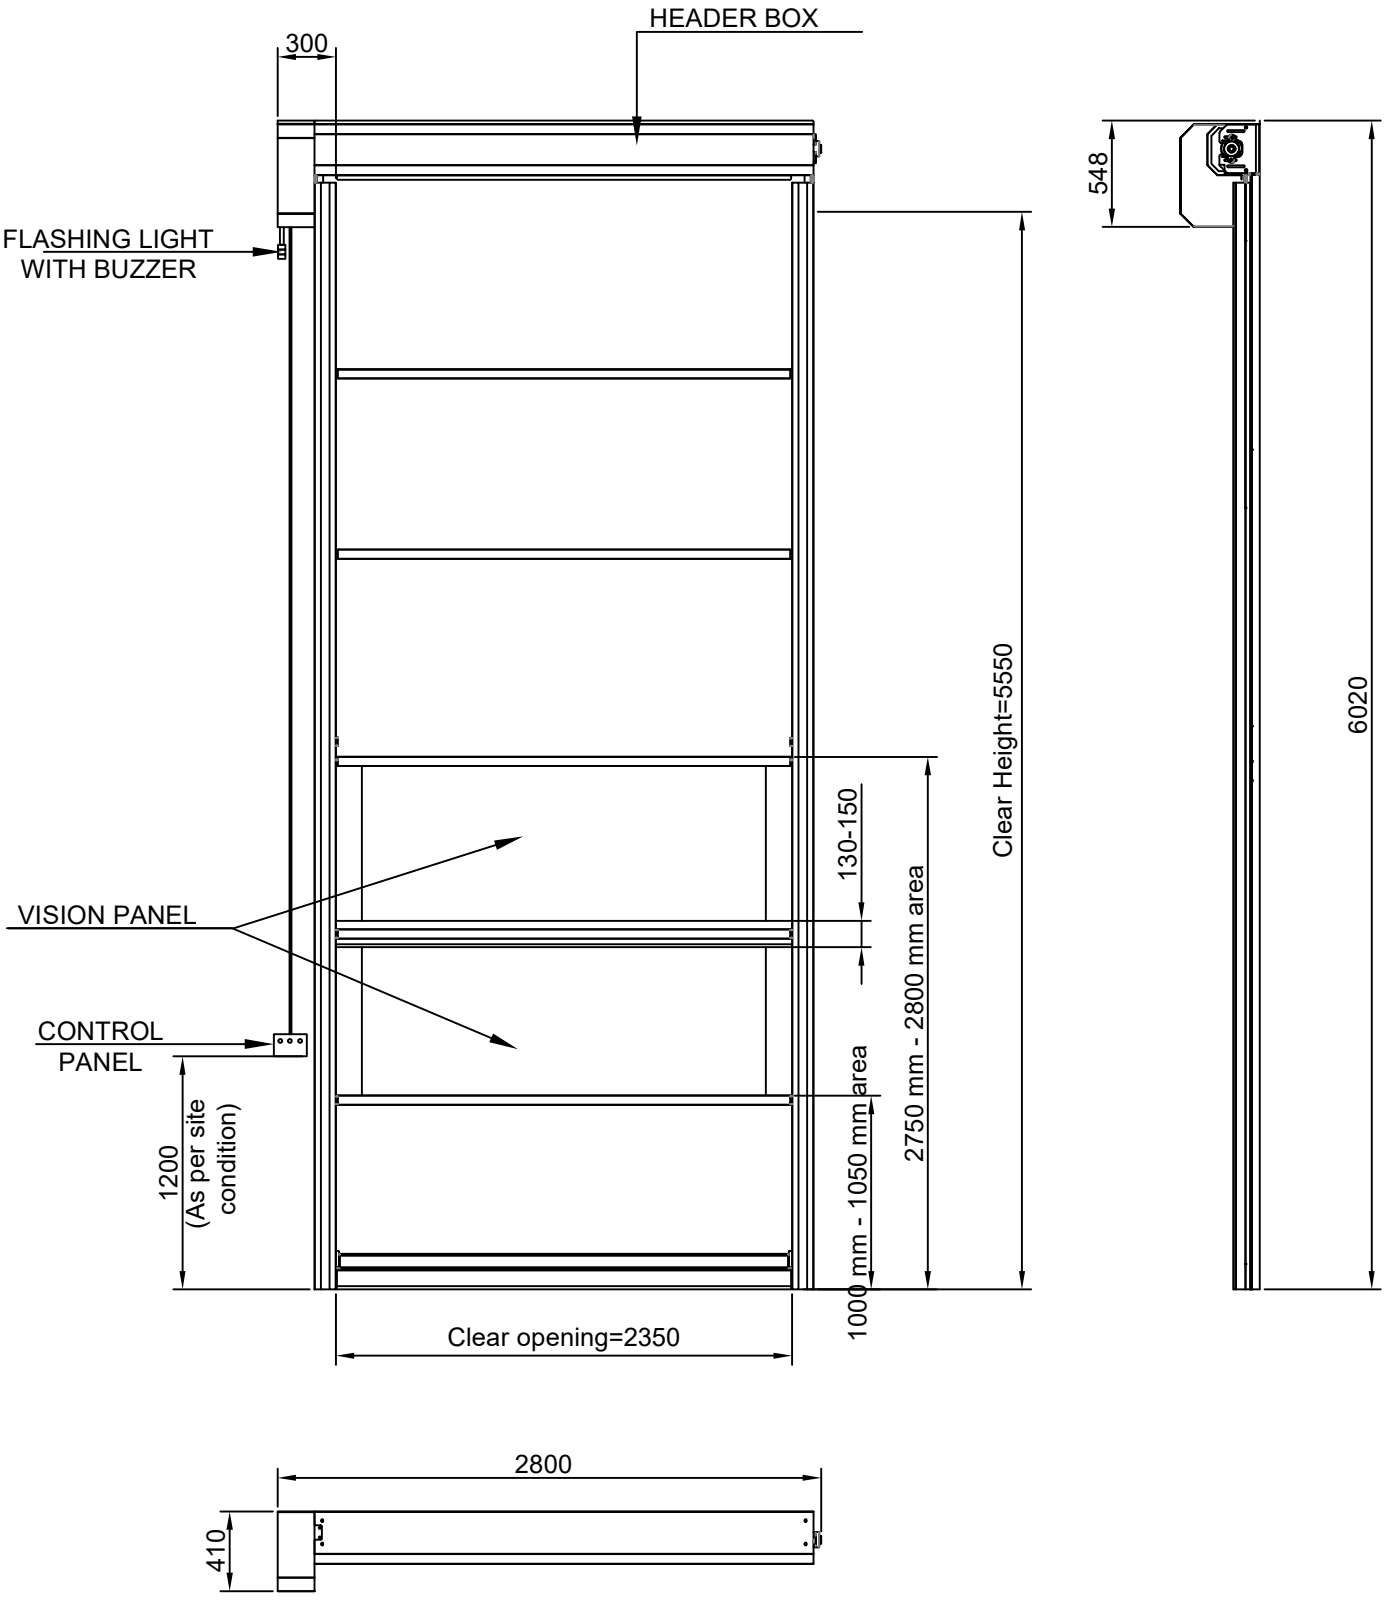


Note:-

1.All dimension are in MM

2.All civil work and Structure is in client scope

3.Curtain color is Gray RAL 7035

4.Height of the window can be changed to 0-50 mm area

Rev No.	Revision	Date	Revised By
1.	Overall dimension of the door has been changed.	18/01/2022	Sujata

This drawing & design is the property of NIHVA TECHNOLOGIES. Not to be sold or copied to any other concern.

TITLE:- HIGH SPEED DOOR

NIHVA TECHNOLOGIES PVT. LTD.
NIHVA TECHNOLOGIES PVT. LTD. PUNE
Tel : 020 66304033
Email:- info@nihva.com
Website:- www.nihva.com

	NAME	DATE	SIGN
DRAWN	SUJATA	18/01/2022	
CHECK	G. P	18/01/2022	
APPRD.	A.K	18/01/2022	

CLIENT - YASH HIGHVOLTAGE LTD.

LOCATION - GUJARAT

PRODUCT - HSD

If any queries contact : design@nihva.com

DWG NO:-NIHVA/21-22/CLT/0310 REV- 1

ALL DIMENSION ARE IN mm

SCALE: NTS SCALE:-- 1:1 SHEET: 01 OF 01