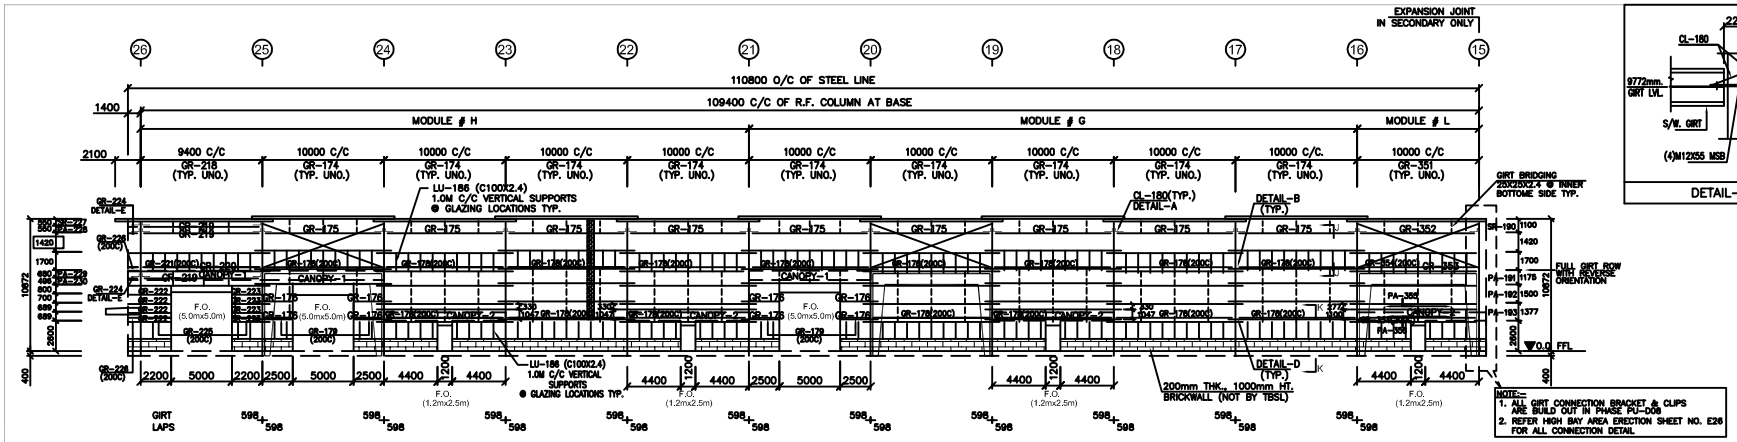


NOTE:-
1. ALL GIRT CONNECTION BRACKET & CLIPS ARE BUILD OUT IN PHASE P2-008
2. REFER HIGH BAY AREA ERECTION SHEET NO. E26 FOR ALL CONNECTION DETAIL


SIDEWALL FRAMING @ G.L. : A

PORTAL DETAIL & BRACNG DETAIL REFER DWG NO :-E23
FOR BRIDGING DETAILS AT EAVE REFER E11


ALL 5.0MX5.0M F.O. JAMB AND HEADER SIZES ARE ISMC-300
AND 1.2Mx2.5M F.O. JAMB AND HEADER SIZES ARE C240x3.0

:- DENOTES INSULATION – ROCK WOOL, 50MM THICK 48KG/M3 WITH FSK FACING, REFER E32


FOR SHEETING REFER E-20A

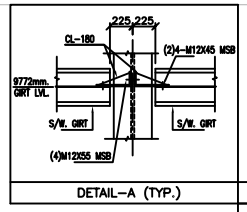


DETAIL–A (TYP.)

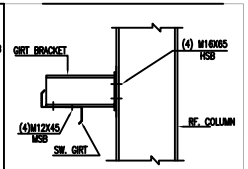


TYPICAL GIRT CONNECTION DETAIL

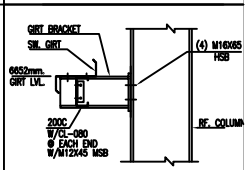


DETAIL–B
GIRT CONNECTION DETAIL (TYP.)

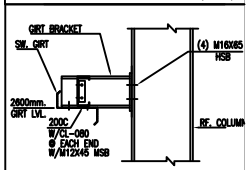


DETAIL–D
GIRT CONNECTION DETAIL (TYP.)

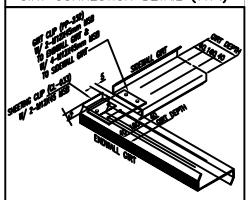

SW. GIRT CONNECTION DETAIL
WITH EW GIRT
(FOR REMAINING LEVELS REFER DWG. NO. E29)

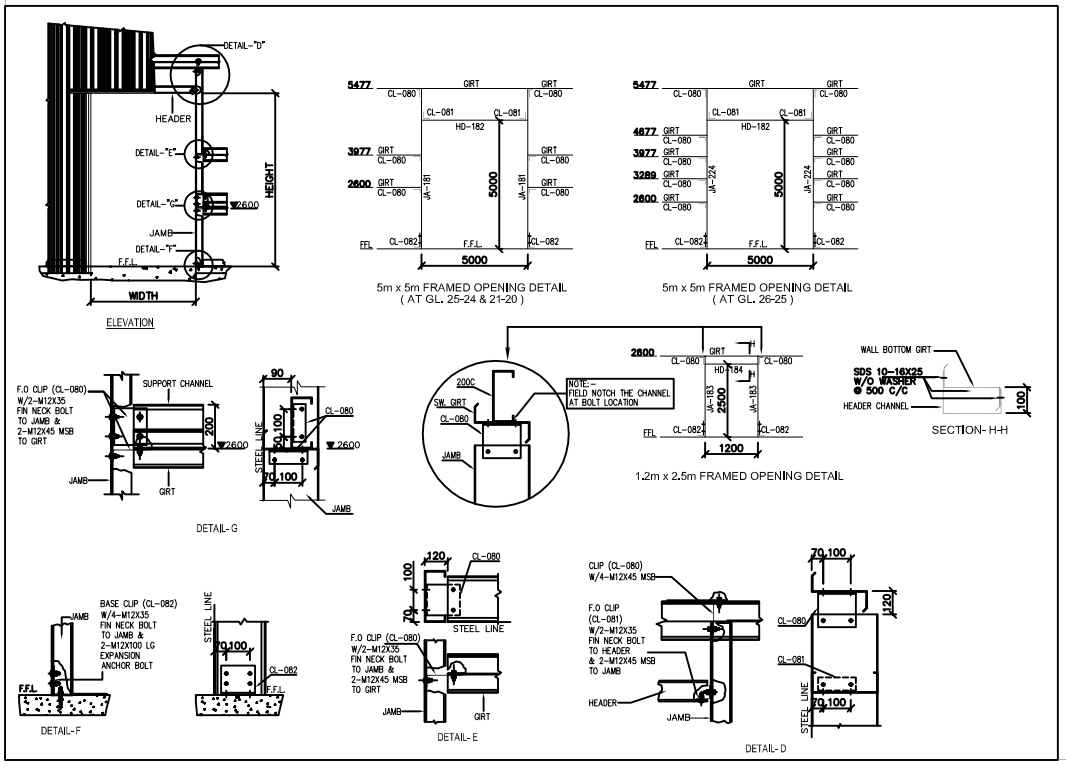

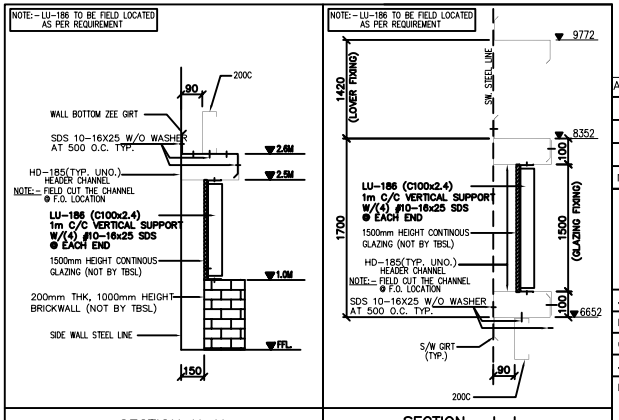

ALL DIMENSIONS ARE IN MM

NO.	DATE	DESCRIPTION	DRN	CHK	DSN
00	04.07.13	ISSUED FOR CONSTRUCTION	PKM	GHR	SSS/SSD

Tata BlueScope Steel Limited
Survey No. 247 & 250,
Hinjewadi, Taluka Mulshi,
Pune - 411057, India.
Telephone : +91 20 6674 2000
Facsmile : +91 20 6674 2001
www.tatabluescopesteel.com

JOB NO.	: FM1-1384	BUILDING NO. : 01 (F.L. 15 TO 26)
PROJECT NAME	: GE INDIA INDUSTRIAL PVT. LTD	
CUSTOMER	: GE INDIA INDUSTRIAL PVT. LTD	
JOBSITE LOCATION	: CHAKAN, PUNE	
DRAWING TITLE	: SIDEWALL FRAMING @ G.L. : A	DRAWING NO. E20