

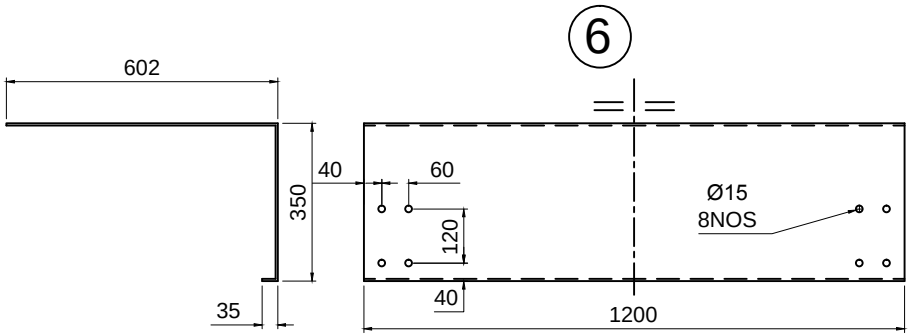


6. FRONT PLATE 965 X 5 THK X 1200L = 1 NO

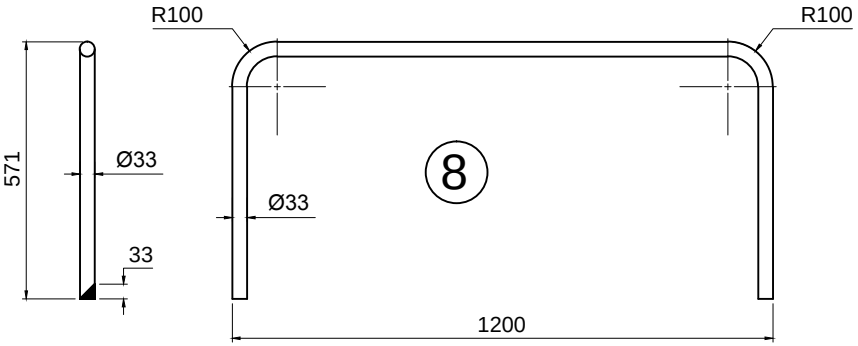

8. HANDLE OD 33 X 2340L = 1 NO

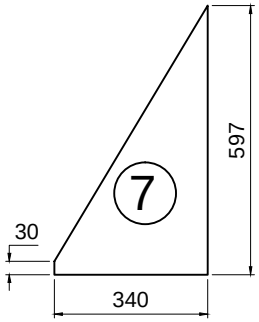

7. RIB 340X 5 THK X 597L = 2 NOS

This drawing & design is the property of NIHVA TECHNOLOGIES. Not to be sold or copied to any other concern.

TITLE : -

BASE FRAME DETAILS

	SIGN	DATE
DRAWN	P.A	04.10.2018
CHECK	R.D	04.10.2018
REV.		
APPROVAL		

NIHVA TECHNOLOGIES PVT. LTD.

NIHVA TECHNOLOGIES PVT. LTD. PUNE
Tel : 020 66304033
Email:- info@nihva.com
Website:- www.nihva.com

CLIENT -

PROJECT -

SITE -

DWG. NO. : NIHVA/18-19/MFG/NSL/1018/014

If any queries contact : projects@nihva.com

SCALE: NTS | WT: | SHEET: 01 OF 01

ALL DIMENSION ARE IN mm