Rep	Qté	Mat	Débits
A	1	E24-2	TUBE 300x200x5 Lg:1470 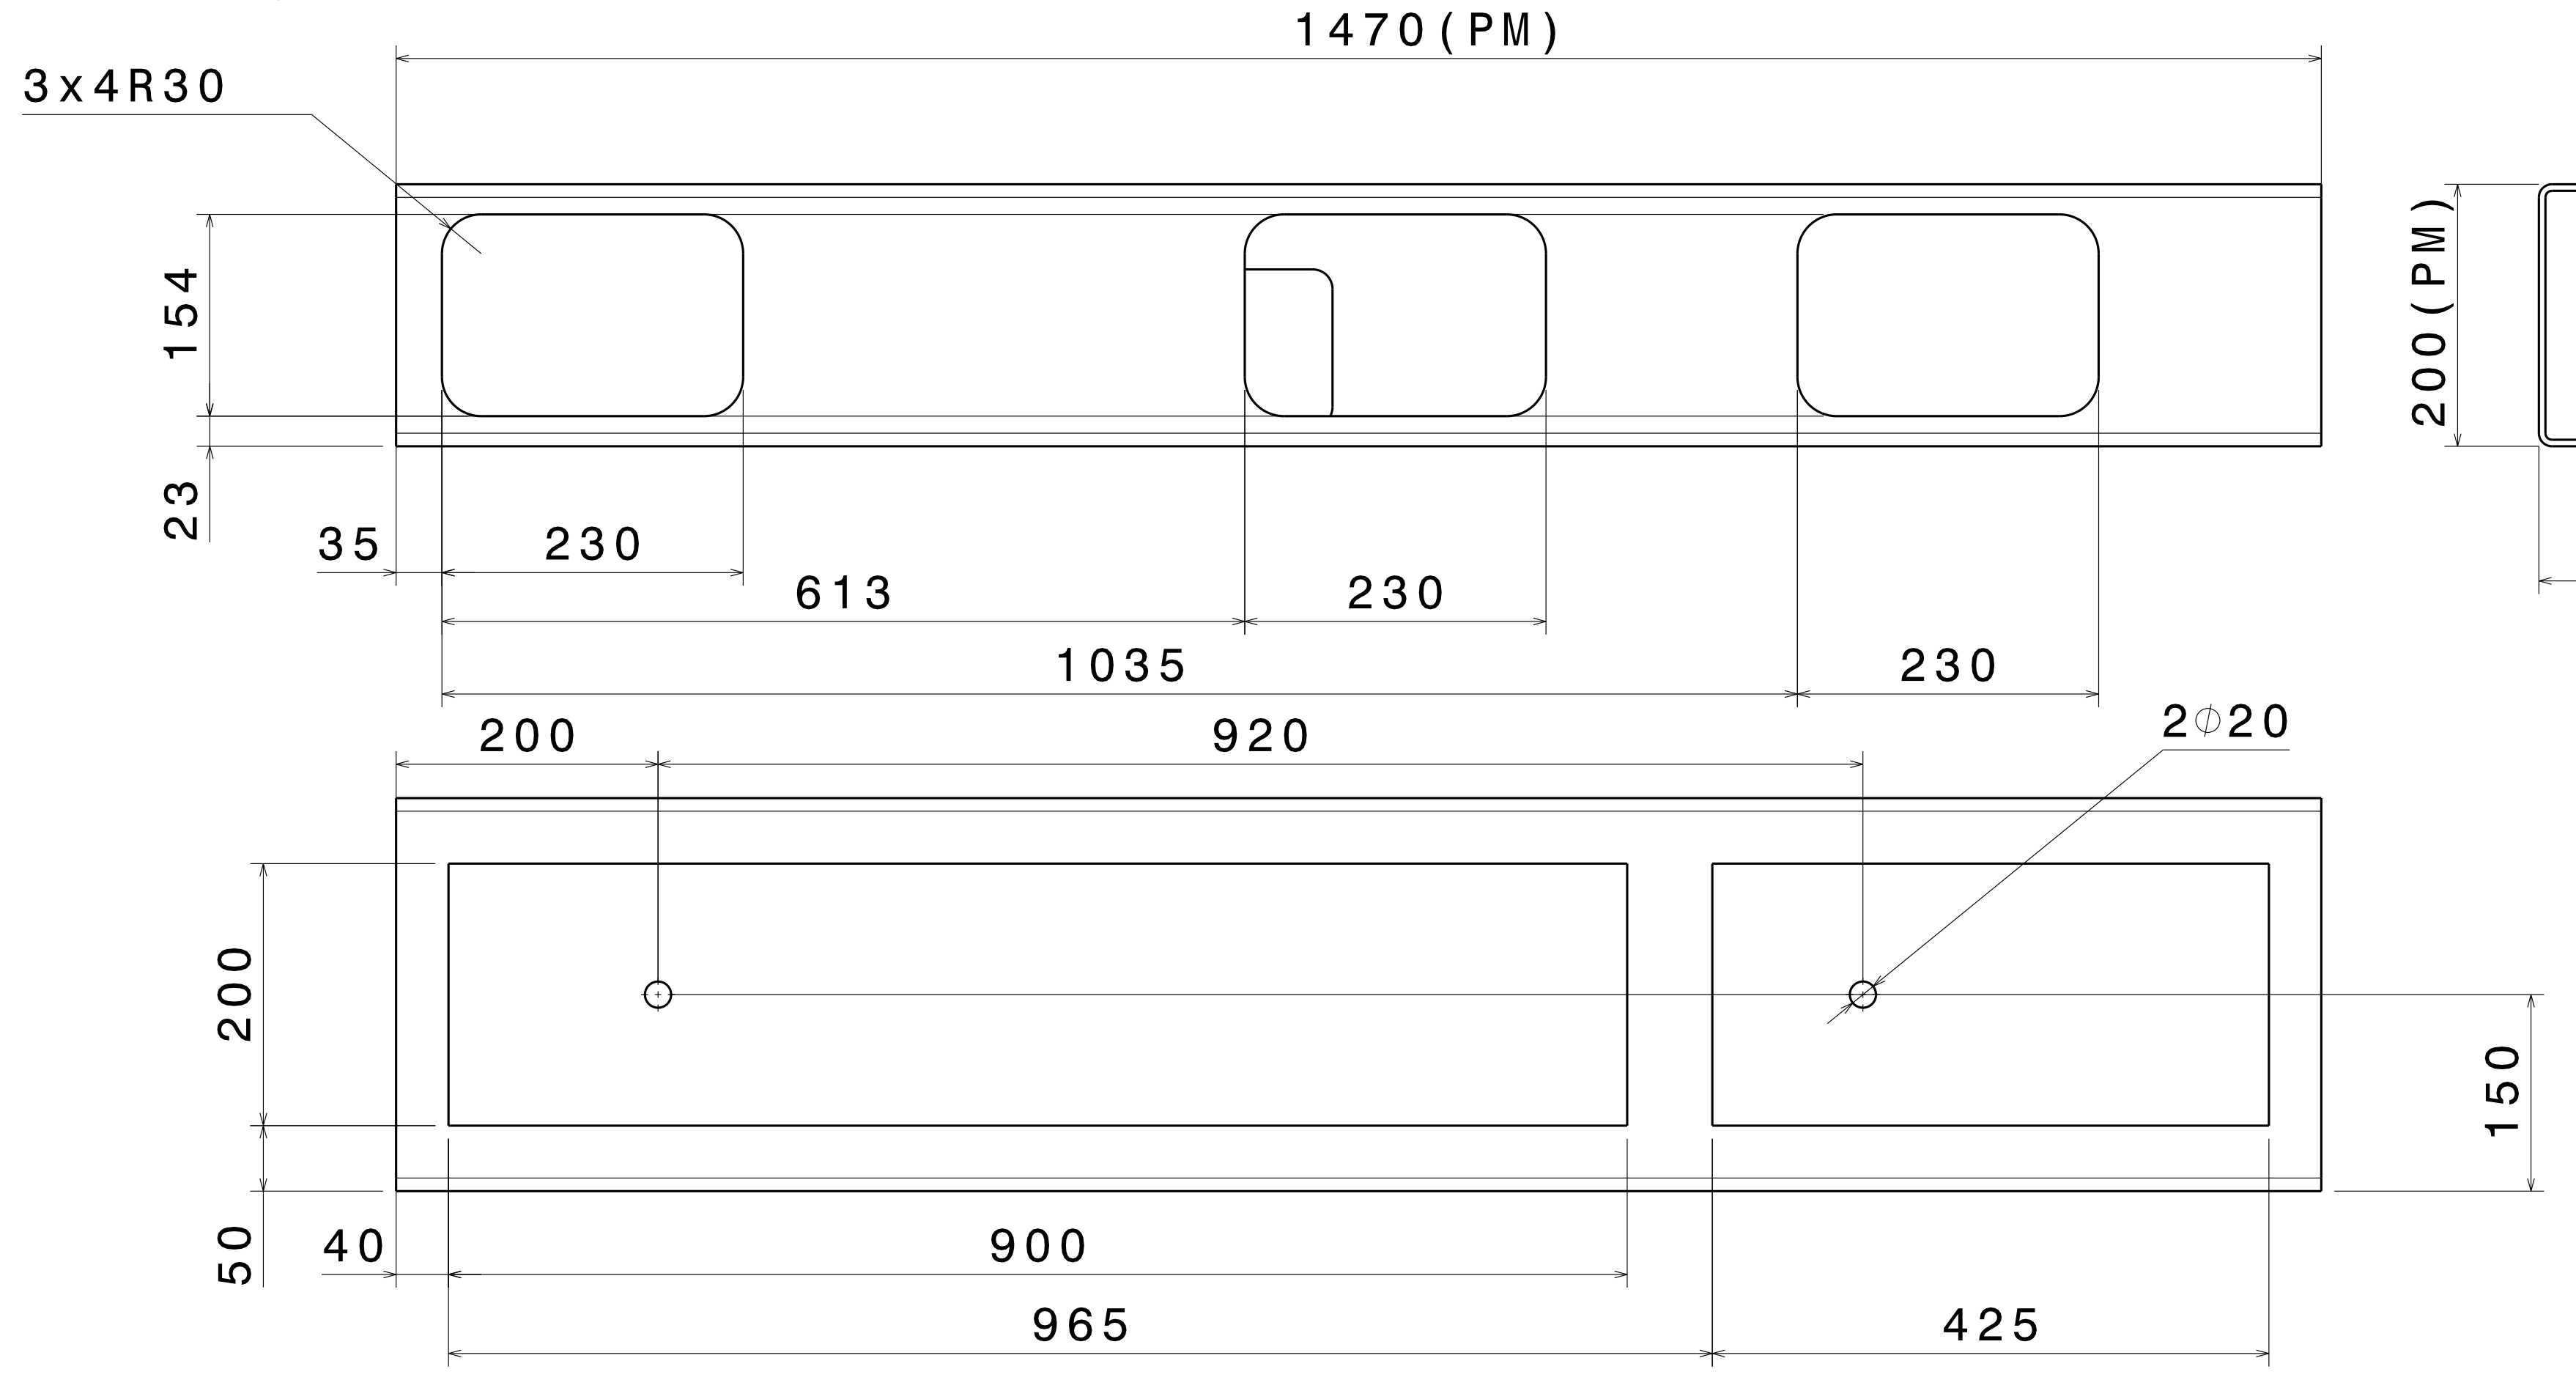
B	5	E24-2	Ep:18 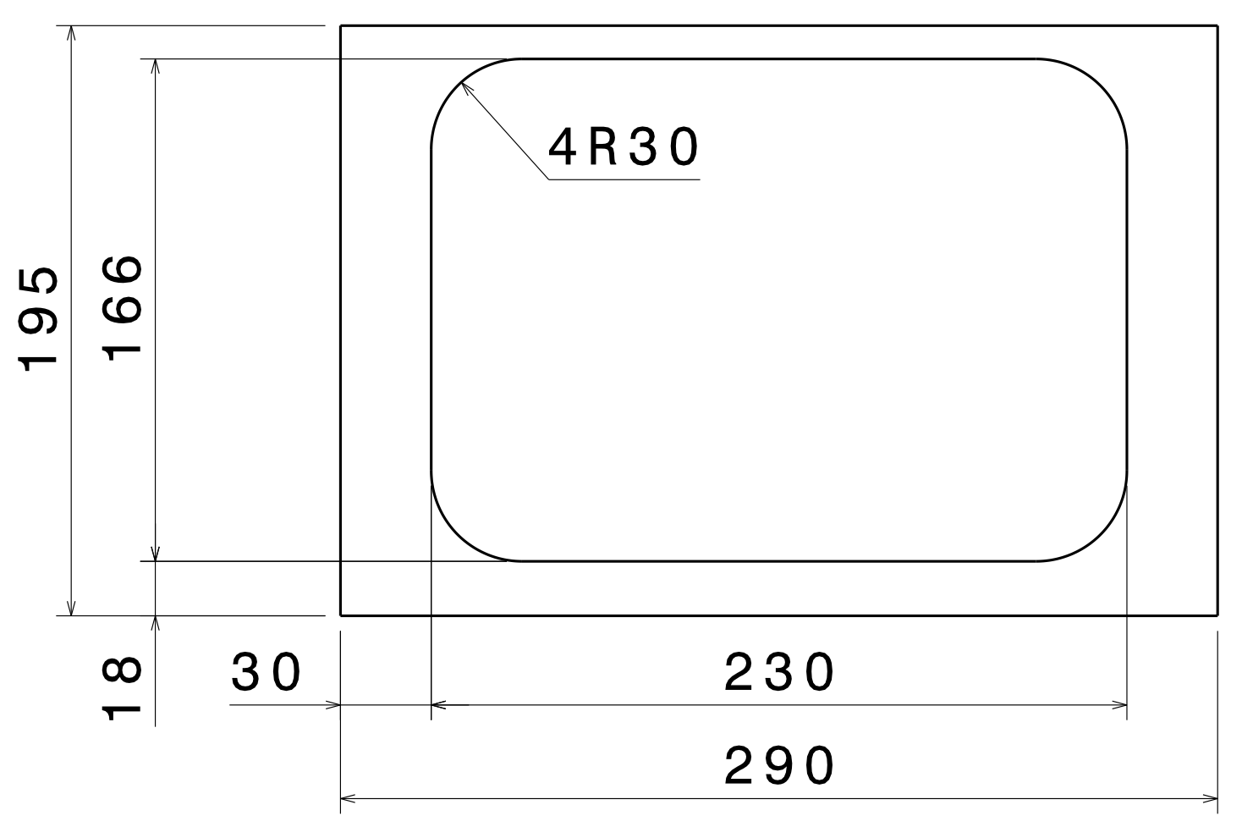
C	1	E24-2	Ep:18 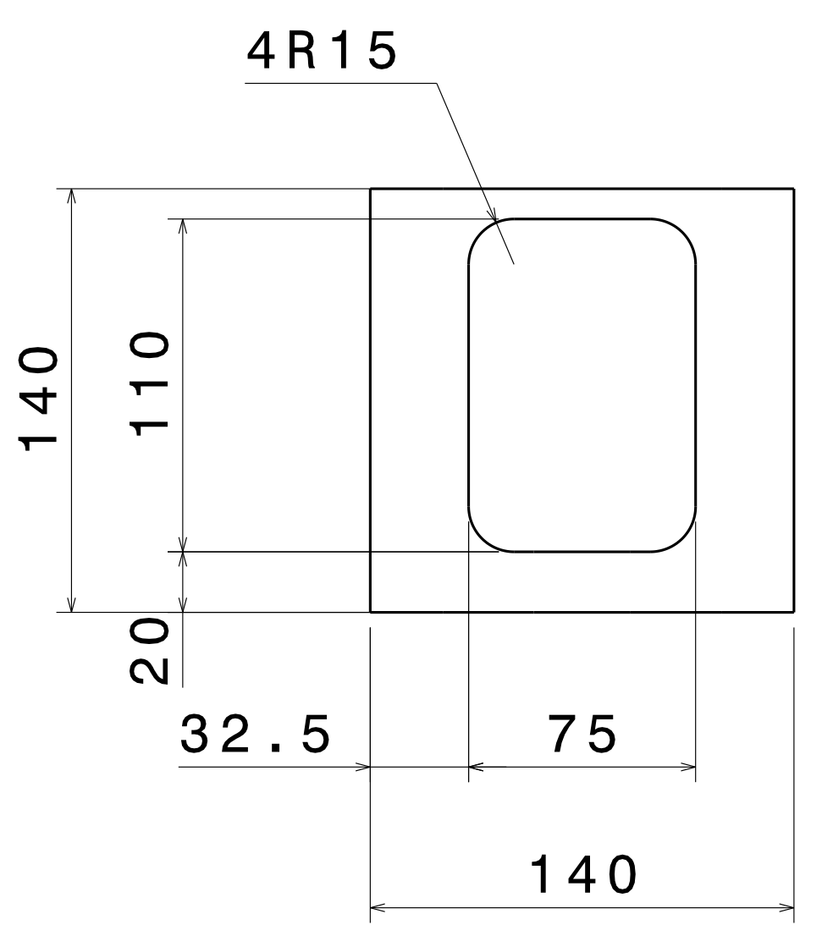
D	2	E24-2	270x130x10
E	2	E24-2	260x120x10
F	2	E24-2	300x200x6

3x4R30
1470(PM)
154
23
35
230
613
230
1035
230
200(PM)
300(PM)
2x4R30
154
120
15
23
4R15
230
35
100
615
230
1070
200
920
2⌀20
200
150
50
40
900
965
425

4R30
195
166
18
30
230
290

4R15
140
110
20
32.5
75
140

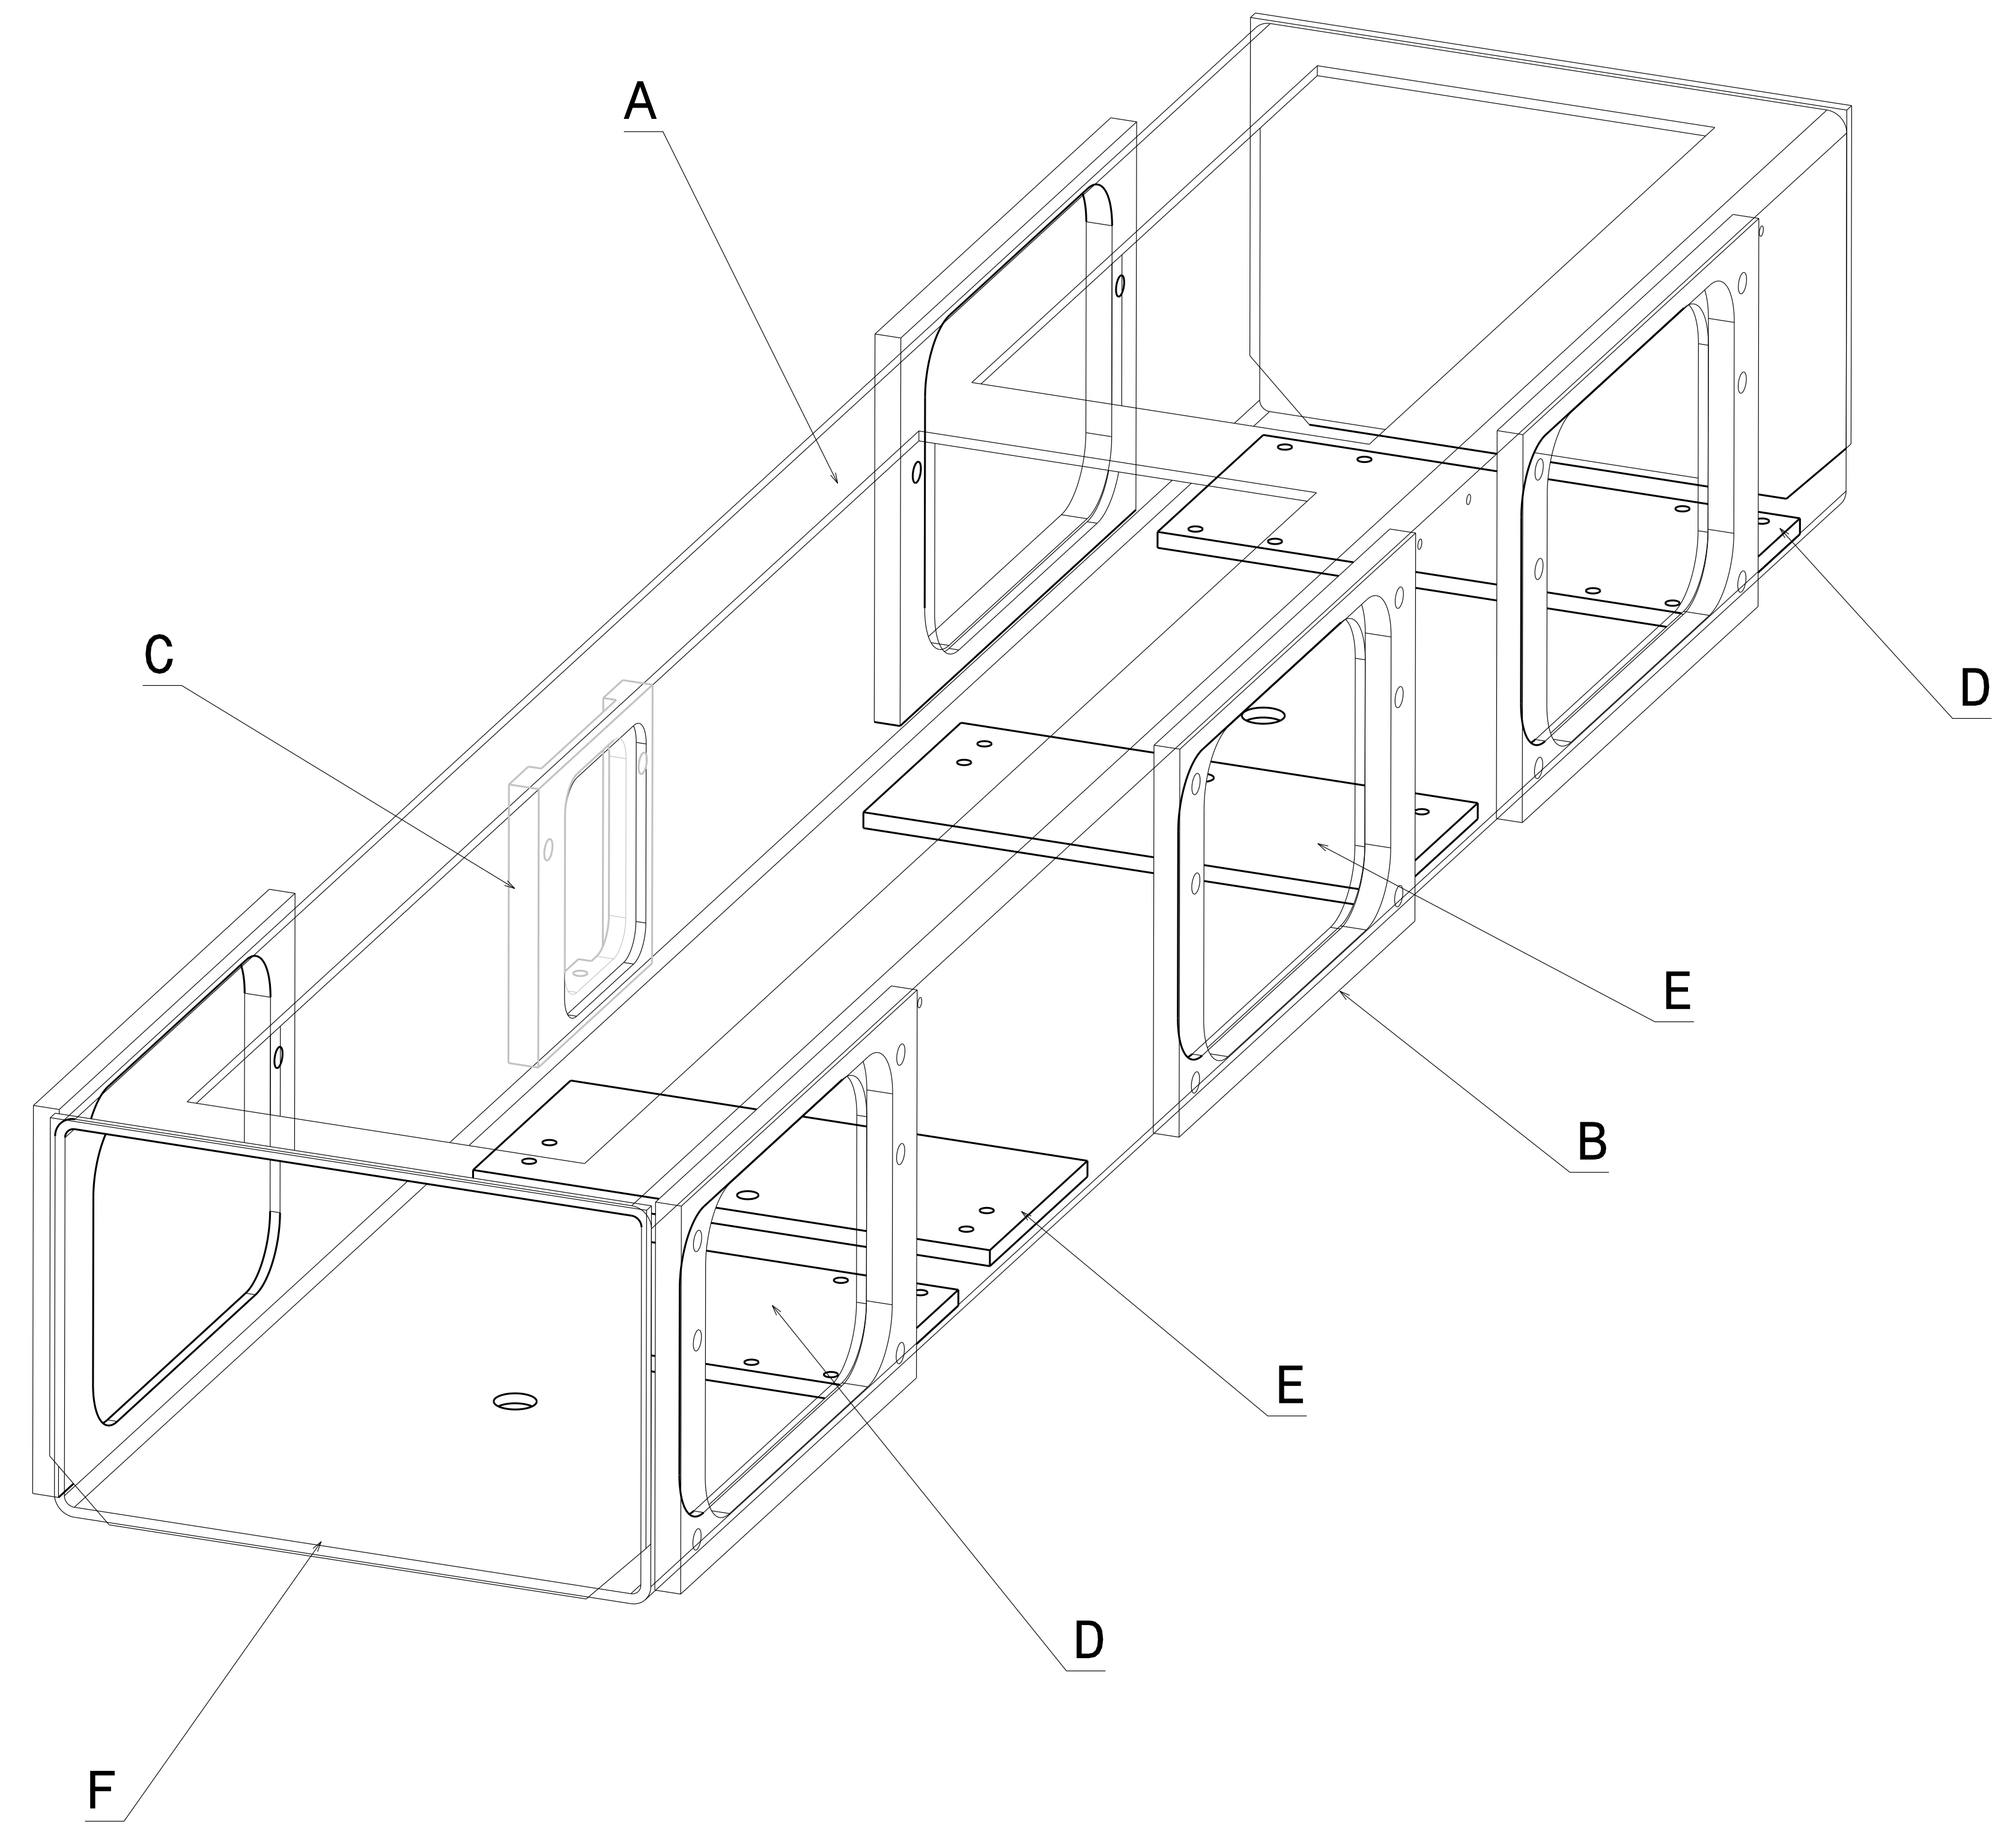

SPECIFICATIONS PARTICULIERES COTATION

RAYONS NON COTES : R=5mm

CASSER LES ANGLES VIFS : 0.5x0.5

COTES SOULIGNEES = COTE DE SOUDURE

COTES ENCADREES = COTE DEPART USINAGES

TOLERANCES COTES ENCADREES : ⌖ | 0.2 | X | Y | Z

TOLERANCES ENTRAXES GOUPILLES: +/- 0.02

TOLERANCES ENTRAXES VIS: +/- 0.2

TOLERANCES ENTRAXES GROUPES DE TROUS: +/- 0.2

POUR LES PERCAGES ⌀H7: R 6,3 √

USINAGE : ∿ (R 12,5 √ R 6,3 √)

SPECIFICATIONS PARTICULIERES REALISATION

STABILISATION A REALISER APRES SOUDURE

INDICATION DE SOUDURE

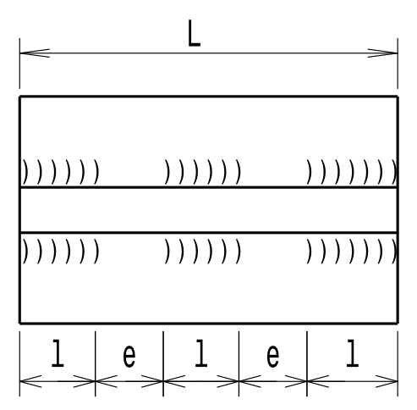

L	a ◣ l	(e)
jusqu'à 200	30	40
jusqu'à 400	40	60
sup à 400	60	80

ACTEMIUM
7 avenue Roger Hennequin
B.P. 42
ZA TRAPPES-ELANCOURT
78193 TRAPPES CEDEX

MASSE(kg): 62,685

✓ Sauf indications contraires
Cotes sans Tolérances : Js13
Casser les angles 0,5 à 45°
Etats de surface:
NORME E00.14.020.N
Tolérances de forme et de position:
NORME NF E04-552

DATE	Ets	SERVICE	NOM	MODIFICATIONS	IND

ECHELLE 1 Cm

DESIGNATION : piece, sous-ensemble ou ensemble
MANUTENTION
S/ENS TGC Lg 1500
-
POUTRE TABLE A GALET LG 1500

MATIERE ENS-SOUDE -
TRAITEMENT RAL-3001
BRUT -

RESPONSABLE D'AFFAIRE : NOM	SERVICE	ETABLISSEMENT	DESSINE PAR : NOM	SERVICE	ETABLISSEMENT	DATE	VISA
H. LEGROS	65306	RENAULT	HSK	BE	ACT	05-2013	CCO

ORIGINAL — FORMAT: A0 — CONCEPTION: ⊞ MANUELLE ⊞ NUMERIQUE — ARCHIVAGE: -
COPIE: ⊞ PAPIER ⊞ MICROFILM ⊞ SCANNER

Ce document est la propriete de RENAULT et ne peut etre reproduit ou communique a un tiers sans son autorisation ecrite prealabre.

RENAULT
92109 Boulogne - Billancourt Cedex

AUTRE NUMERO: -

MATRICULE	ETABLISSEMENT ou SYMETRIE	N° MABEC BED ⊞ SPECIFIQUE ⊞ STANDARD	SUFFIXE	
-	-	—	-	VEHICULE ou ORGANE KF67 -
-	SYMETRIE	-	-	
-	AVTOVAZ 3	E840010511	-	PLANCHE 1/3

0 10 20 30 40 50 60 70 80 90 100mm