


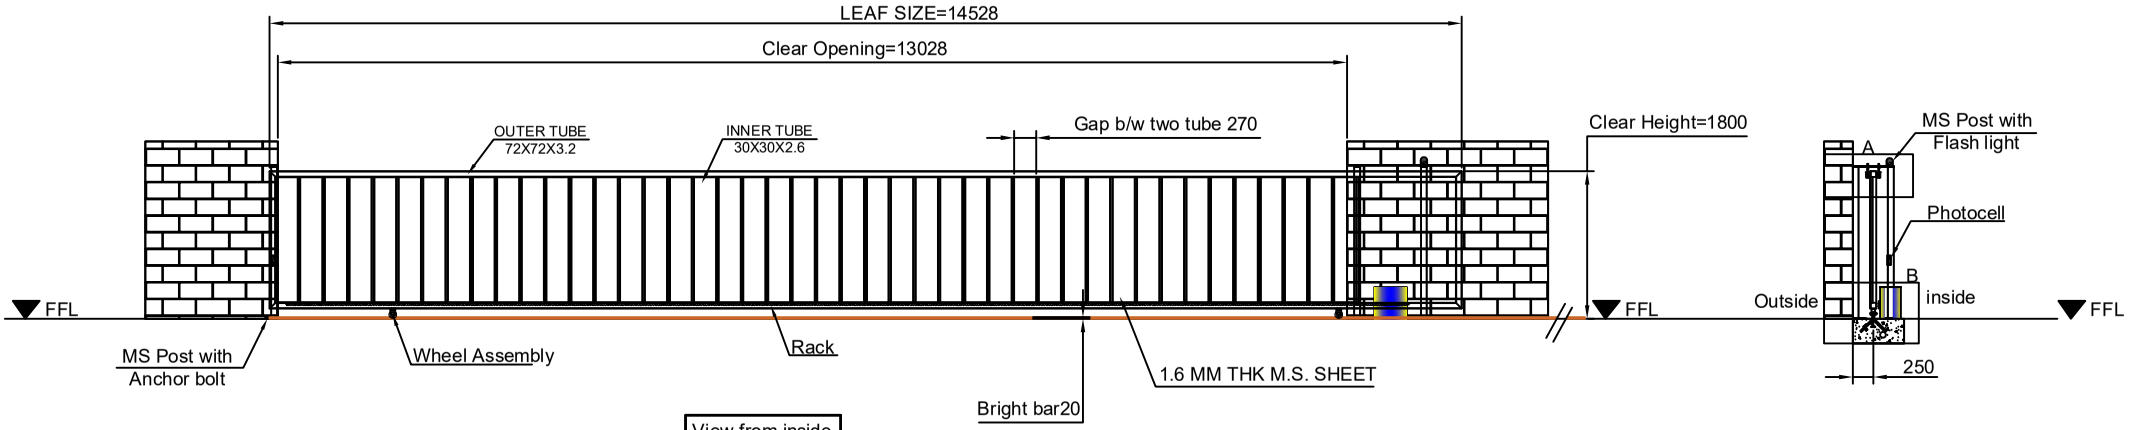


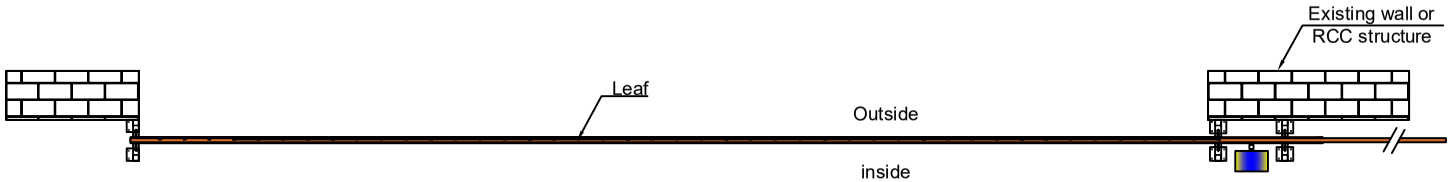

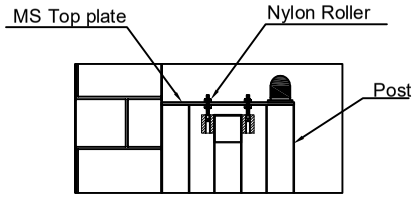

Opening direction

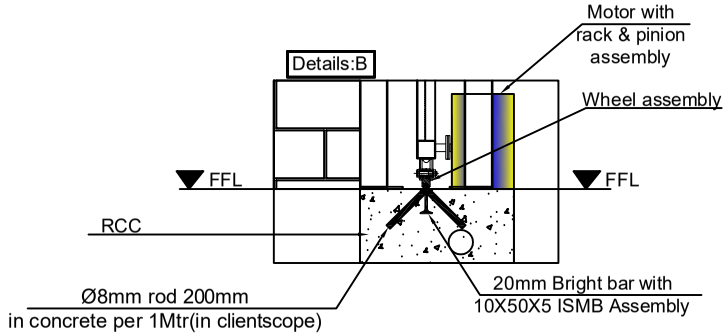

Note:-

1.All Dimension are in MM.
2.All Civil work and if required motor foundation or ms bracket will be in Client scope
3.Civil,Installation and Fabrication Tolerance will be ±20mm
4.Reuired Parking will be 14628 mm
5.Surface Finish(painting): Approved RAL 7031
6.CD between 2 tubes may vary

Rev No.	Revision	Date	Revised By
3	Sheet design changed to tray	01/02/2023	Nirmala
2	Sq. tube size changed from 32x32 to 30x30 and so gap b/w tube changed	28/01/2023	Nirmala
1	Revision Done As Per Client Requirements	23/01/2023	Nirmala

This drawing & design is the property of NIHVA TECHNOLOGIES. Not to be sold or copied to any other concern.

TITLE:- Motorized Sliding Gate

NIHVA TECHNOLOGIES PVT. LTD.

NIHVA TECHNOLOGIES PVT. LTD. PUNE
Tel : 020 66304033
Email:- info@nihva.com
Website:- www.nihva.com

	NAME	DATE	SIGN
DRAWN	NIRMALA	20/1/2023	
CHECK	A.K	20/1/2023	
APPRD.	V.T	20/1/2023	

If any queries contact : design@nihva.com

ALL DIMENSION ARE IN mm

CLIENT - Poonam Roller Flour Mill Pvt. Ltd.

LOCATION -

PRODUCT - Motorized Sliding Gate | QTY-01

DWG NO:- NIHVA/22-23/CLT/0179 | REV-02

SCALE: NTS | SCALE:-- 1:1 | SHEET: 01 OF 01