


DRAWING

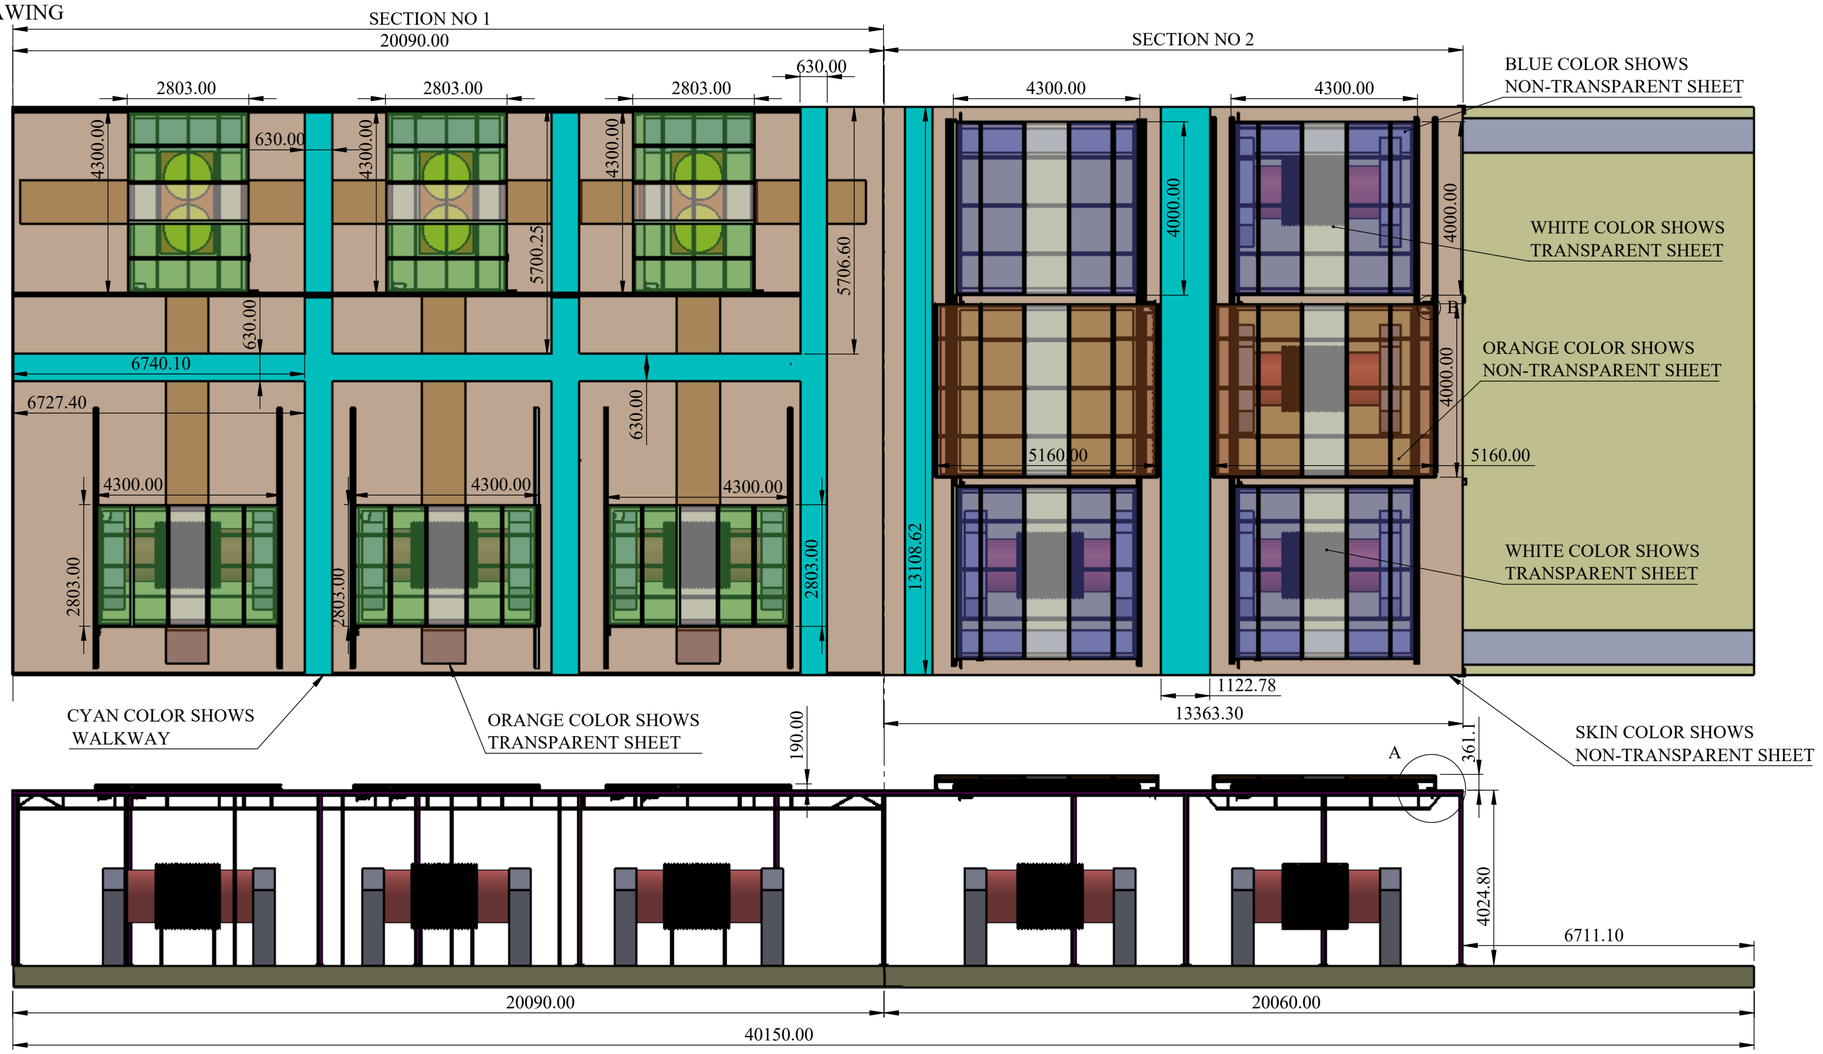

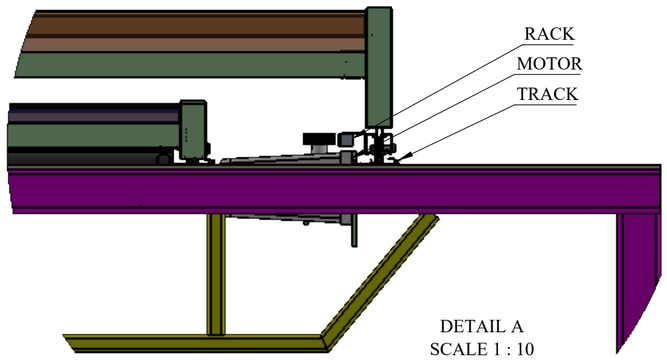

DETAIL A
SCALE 1 : 10
MOTOR ARRANGMENT

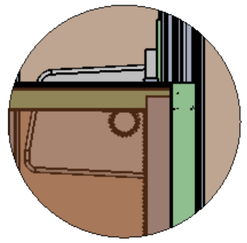

DETAIL B
SCALE 1 : 10

REV DESCRIPTION	DATE	REV NO
	08-08-2025	REV 00
1.		

NOTE :

GA DRAWING

SPECIAL INSTRUCTION'S :

	NAME	SIGNATURE	DATE
DRAWN	V.W.		28-08-2025
CHK'D	S.P.		04-09-2025
APPV'D	V.T.		05-09-2025

TITLE - ROOF AUTOMATION

DWG NO - NTPL-244-PM-001-00-00-00

NIHVA TECHNOLOGIES PVT.LTD.PUNE
Website - www.nihva.com

PRODUCT - RETRACTABLE ROOF

PROJECT NO - NTPL-244-PM | REVISION - 00

SITE LOCATION - GUJARAT | WEIGHT -

MATRIAL - | QTY - 1

If any queries contact - Design@nihva.com


ALL DIMENSION ARE IN mm | A2

PROJECTION METHOD:

SCALE :

DRAWING

REV DESCRIPTION	DATE	REV NO
	28-08-2025	REV 00
1.		

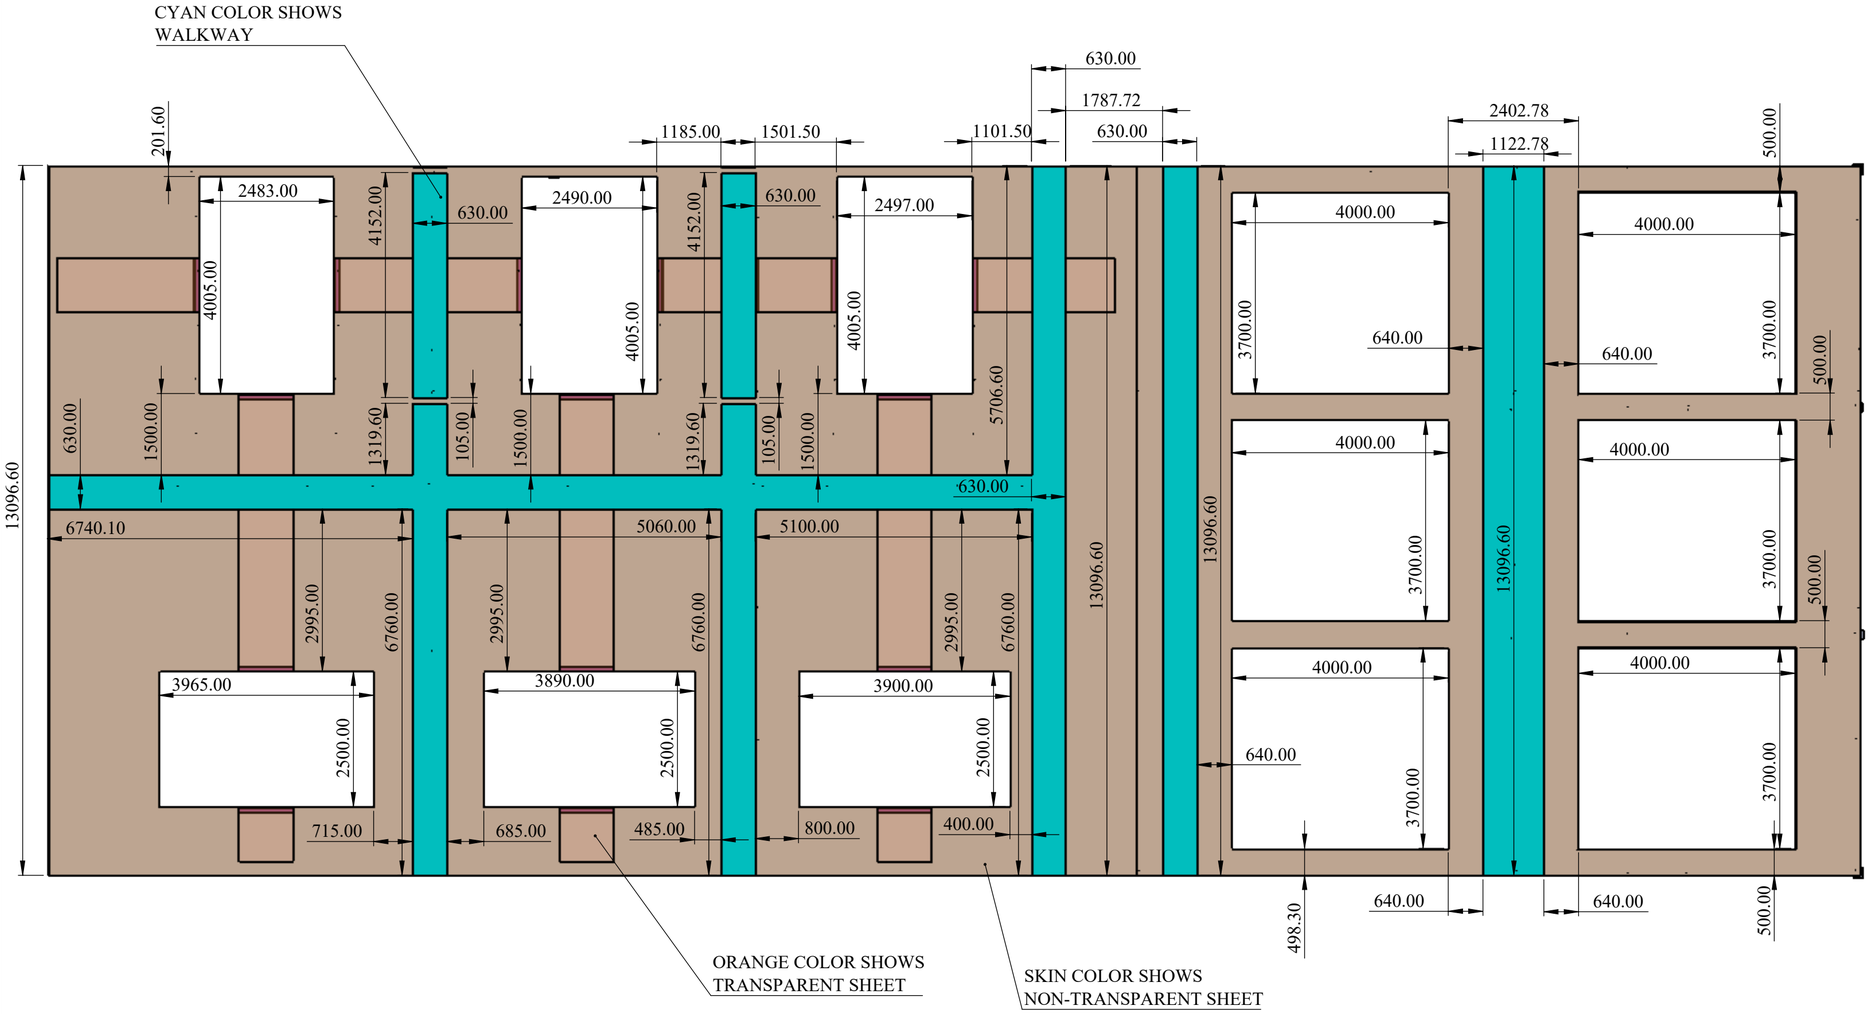

NOTE :

TOP STRUCTURE DRAWING

SPECIAL INSTRUCTION'S :

TITLE - ROOF AUTOMATION

DWG NO - NTPL-244-PM-001-00-00-00

NIHVA TECHNOLOGIES PVT.LTD.PUNE
Website - www.nihva.com

	NAME	SIGNATURE	DATE
DRAWN	V.W.		28-08-2025
CHK'D	S.P.		04-09-2025
APPV'D	V.T.		05-09-2025

If any queries contact - Design@nihva.com

ALL DIMENSION ARE IN mm | A2

PRODUCT - RETRACTABLE ROOF

PROJECT NO - NTPL-244-PM | REVISION - 00

SITE LOCATION - GUJARAT | WEIGHT -

MATRIAL - | QTY - 1

PROJECTION METHOD:

SCALE :