

Abbrevation's:
WOW-Wall Opening Width
WOH-Wall Opening Height
UC-Under Cut
FFL-Finished Floor Level

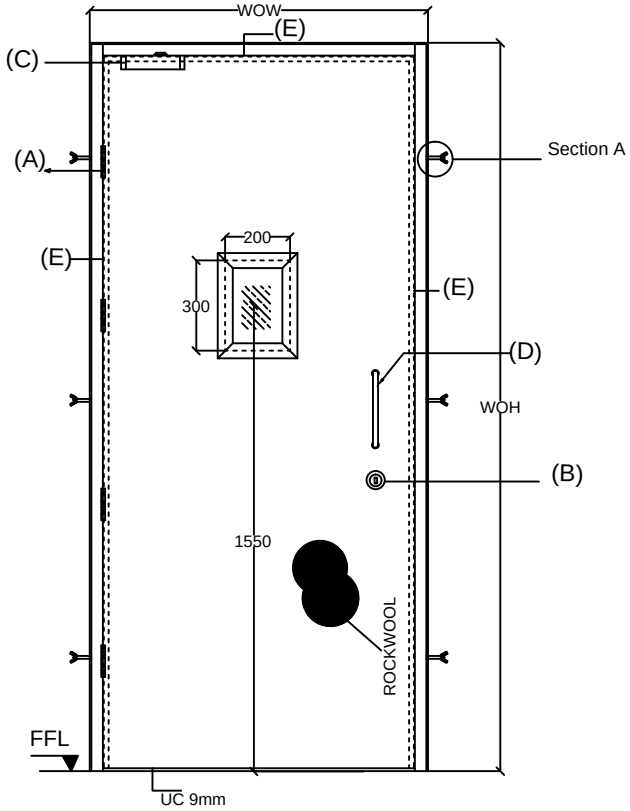


ELEVATION



TOP VIEW

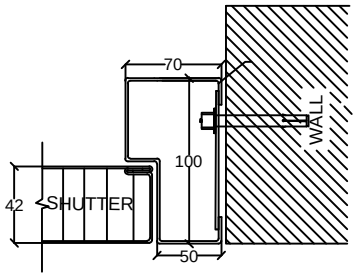


Section A

## ASSESORIES DETALES

(A) HINGES: DORMA MAKE

(B) LOCK : DORMA MAKE.

(C) DOOR CLOSER: DORMA MAKE.

(D) HANDLE : 'D' HANDLE (BOTH SIDE) dia 200mmX22mm
DORMA MAKE.

Shutter thickness : 42 mm
Frame Sheet thick : 1.5mm
Shutter sheet thick : 1.2mm
Fixing : On Solid Brick plastered wall with Anchors

NOTE:- *All Dimensions are in mm.
*Tolerance:-All Linear Dimensions ±3mm,Others ±0.5mm.
*The Drawing Is For Location of Hardware only. Drawing Does Not Represent The Hardware For More Clarity, Please Go Through Hardware Broucher.

COLOR
1.(RAL 9010)

| Steel door size | | |
|---|---|---|
| WOW | WOH | QUANTITY |
| 1000mm | 2200mm | 02 NOS |

NOTE - 1. POLYCARBONET SHEET VISION PANEL REQ.

This drawing & designing is the property of NIHVA TECHNOLOGIES. Not be sold or copy to any other concern.

| TITLE: STEEL DOOR (SINGLE LEAF) | | | | NIHVA TECHNOLOGY PVT. LTD. PUNE |
|---|---|---|---|---|
| | NAME | SIGN. | DATE | Tel : 020 66304033 |
| DRAWN | P.V.A | | 17.07.19 | Email:- info@nihva.com |
| CHECK | V.M.T | | 17.07.19 | Website:-www.nihva.com |
| APPRD. | | | | CLIENT - FERRERO INDIA PVT LTD |
| If any queries contact: design@nihva.com | | | | PROJECT - |
| ALL DIMENSION ARE IN mm | | | | SITE LOCATION - BARAMATI |
| | | | | DWG. NO. - NIHVA/19-20/0050 REV.:-R00 |
| | | | | SCALE: NTS WT: SHEET: 01 OF 01 |