

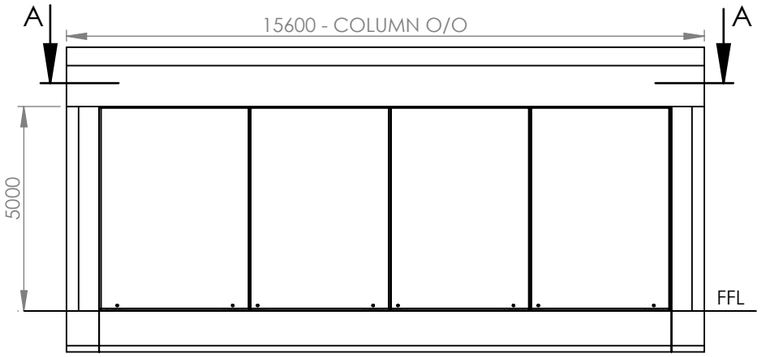



CLOSED POSITION

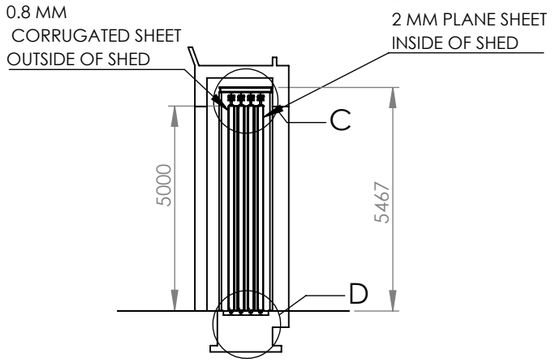

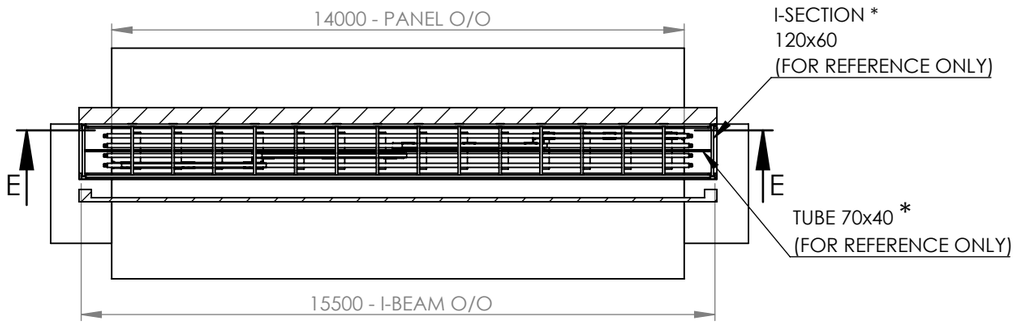


SECTION A-A


* -SUBJECT TO CHANGE AS PER SITE CONDITIONS
-CLIENT SCOPE

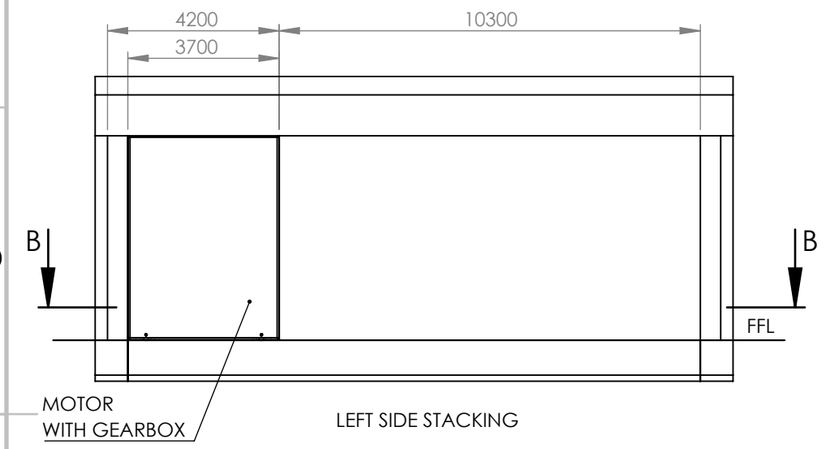


LEFT SIDE STACKING

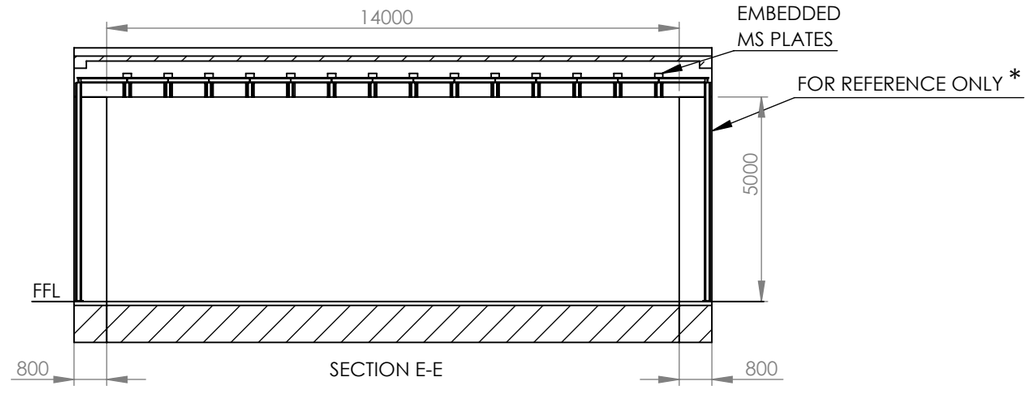


SECTION E-E

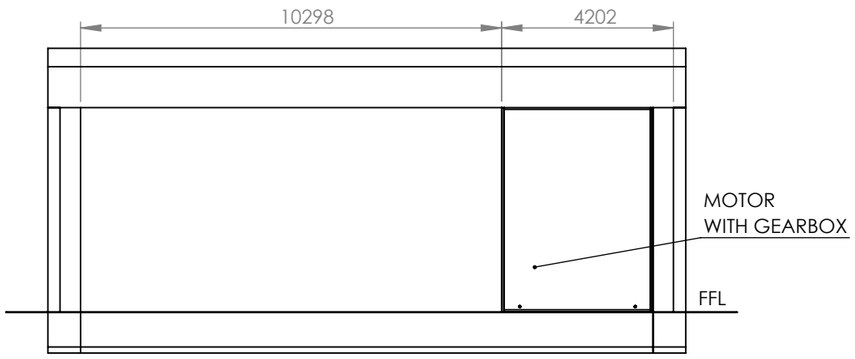


RIGHT SIDE STACKING

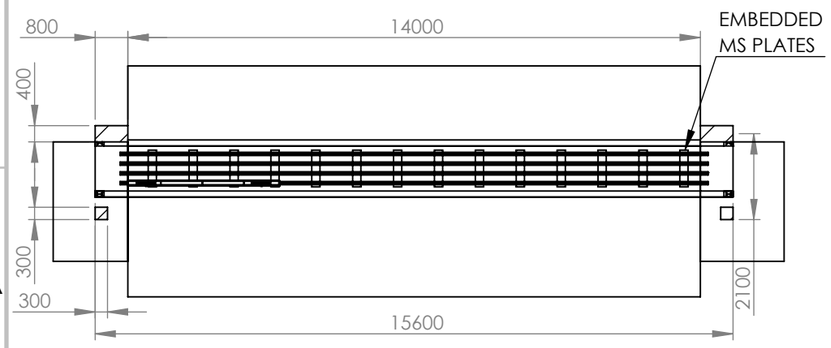


SECTION B-B

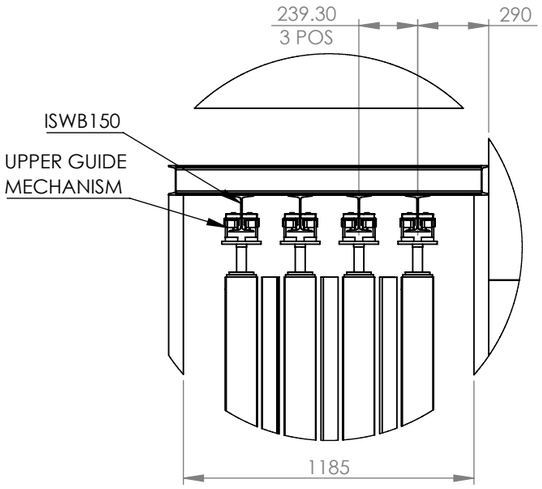

DETAIL C
SCALE 1 : 25

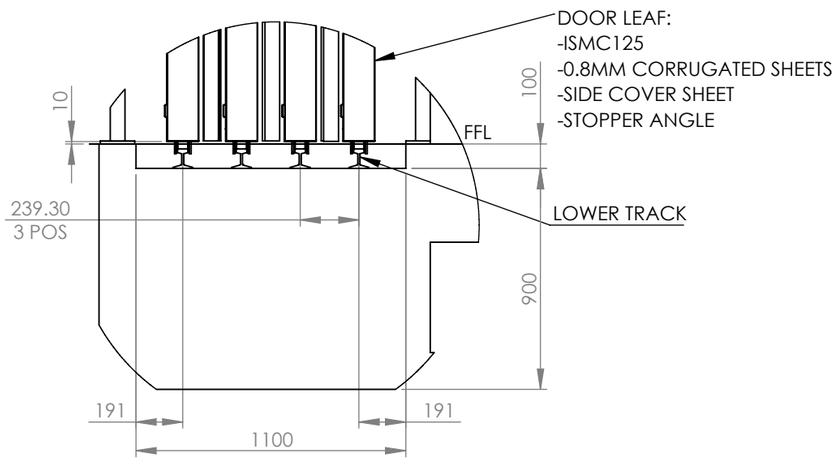

DETAIL D
SCALE 1 : 25

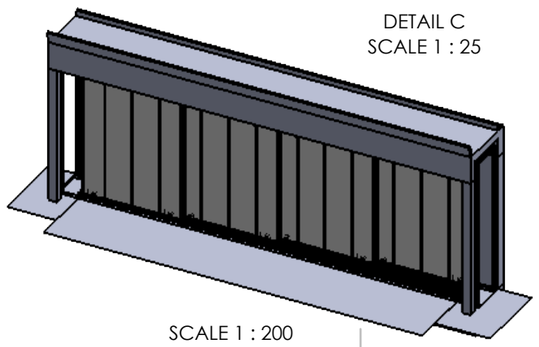

SCALE 1 : 200

TITLE :	**HANGING SLIDING DOOR**		**NIHVA TECHNOLOGIES PVT LTD**
	NAME	**SIGN**	**DATE**
DRAWN	BHARATI SABALE		14-02-2025
CHK'D	SURAJ WARALE		14-02-2025
APPV'D	VIJAY T		14-02-2025
CLIENT NAME :	ISRO		
PRODUCT NAME :	HANGING SLIDING DOOR		
SITE LOCATION :	ALUVA, KERALA		
DWG NO.	GA		A3
			REVISION : 1
DIMENSIONS ARE IN MILLIMETERS	SCALE:		SHEET 1 OF 1