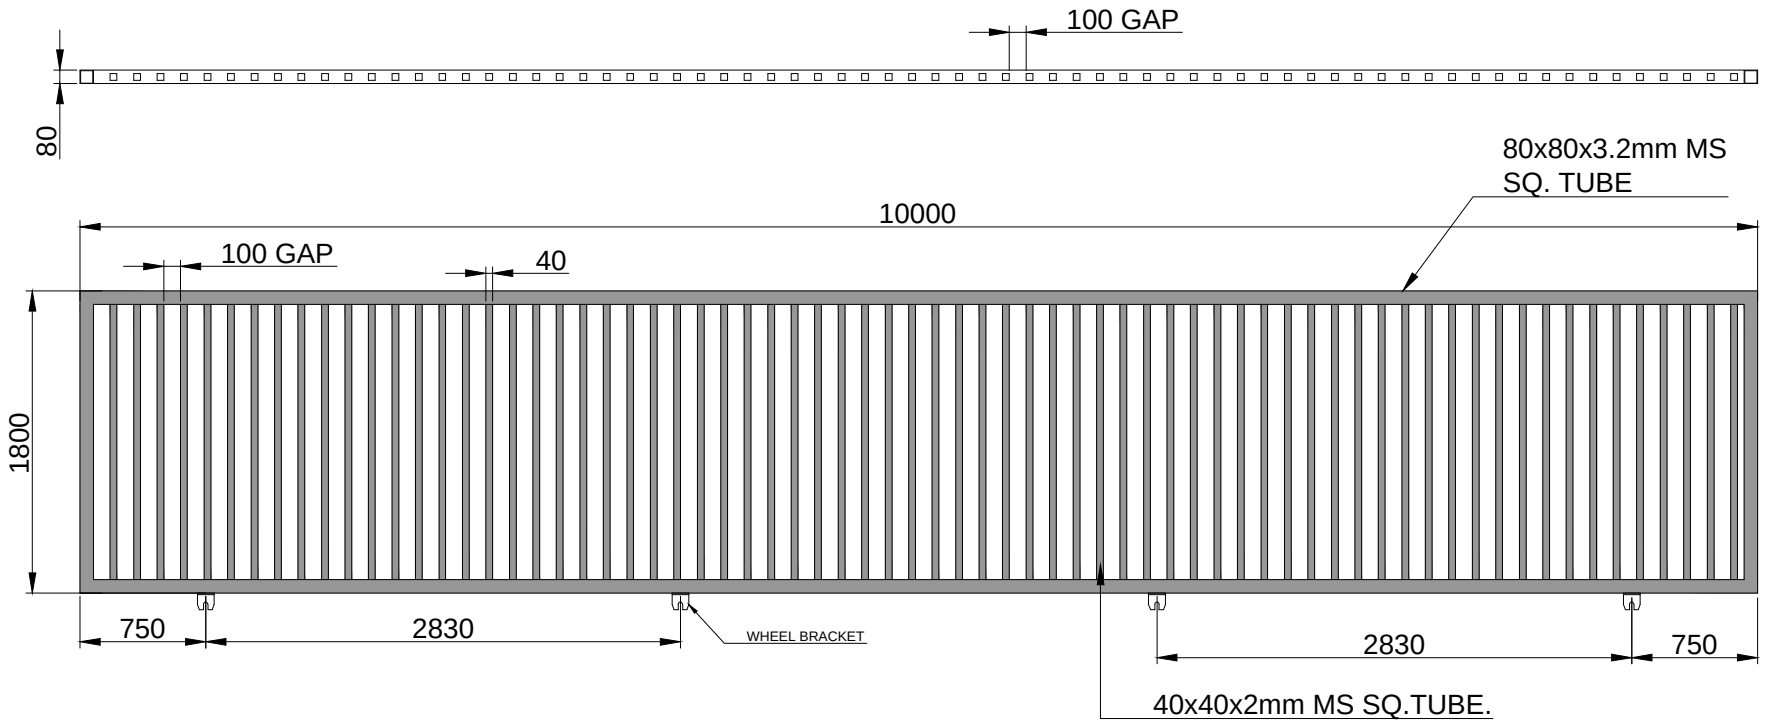


QTY- 2 NOS

TOLERANCE- ±10mm

SR NO	TUBE SPECIFICATION	
1	80X80X3.2mm	OUTER TUBE
2	40X40X2mm	INNER TUBE
3	GAP B/W INNER TUBES	100mm

NOTE-
1. ALL REQUIRED CIVIL WORK WILL BE IN CLIENTS SCOPE.
2. ONE COAT OF RED OXIDE & TWO COAT OF APPROVED RAL SHADE WILL BE GIVEN TO THE GATE.
3.IF REQUIRED GATE LEAF WILL BE IN TWO PARTS FOR TRANSPORTATION & WILL BE WELD TOGETHER ON SITE.

This drawing & designing is the property of NIHVA TECHNOLOGIES. Not to be sold or copied to any other concern.

TITLE
GATE NO 3 & 4

NIHVA TECHNOLOGIES PVT. LTD.

NIHVA TECHNOLOGIES PVT. LTD. PUNE
Tel : 020 66304033
Email:- info@nihva.com
Website:- www.nihva.com

	SIGN	DATE
DRAWN	OMKAR	04/11/17
CHECK	SHEKHAR	04/11/17
APPROVAL	SHEKHAR	04/11/17

CLIENT -
PROJECT -
SITE LOCATION -
DWG. NO. : NIHVA/17-18/VDR/0170 REV-0
If any queries contact : projects@nihva.com
SCALE: NTS WT: SHEET: 01 OF 01
ALL DIMENSION ARE IN mm