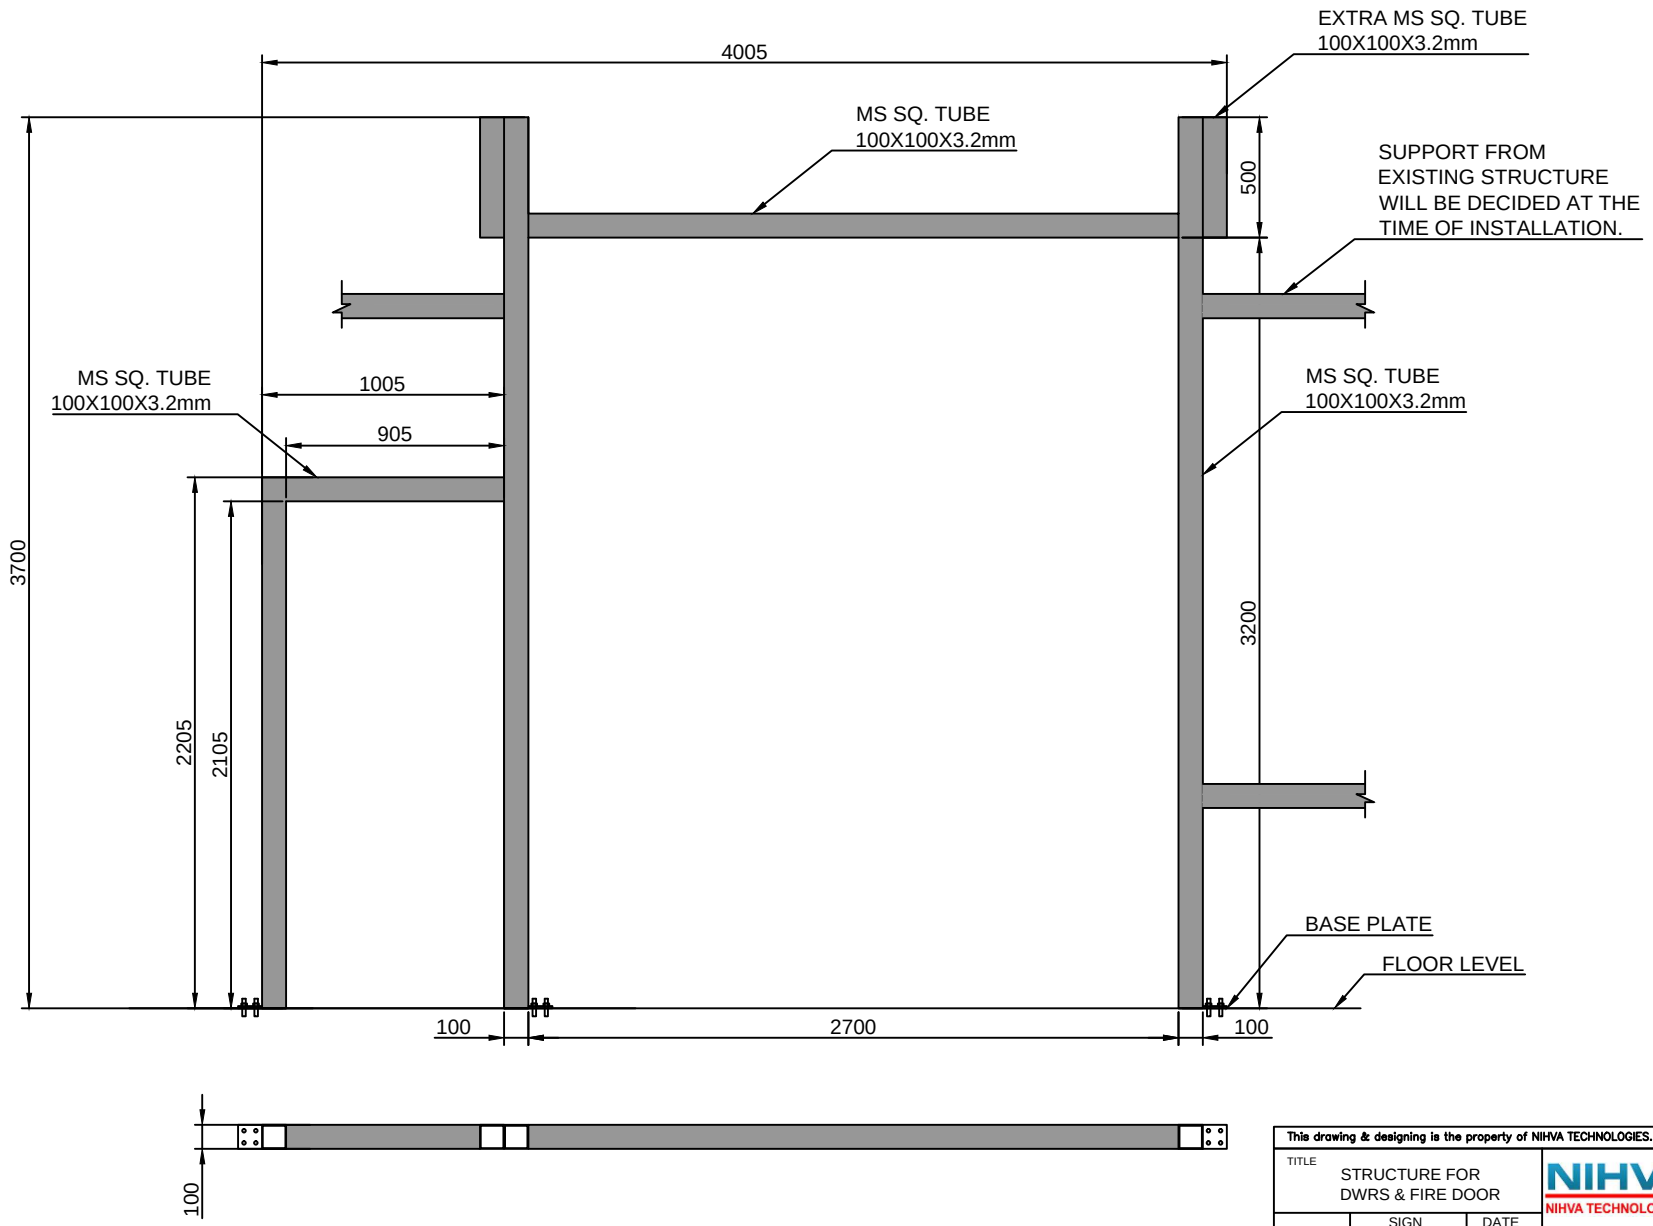

This drawing & designing is the property of NIHVA TECHNOLOGIES. Not to be sold or copied to any other concern.

TITLE: STRUCTURE FOR DWRS & FIRE DOOR	NIHVA TECHNOLOGIES PVT. LTD.	NIHVA TECHNOLOGIES PVT. LTD. PUNE Tel : 020 66304033 Email:- info@nihva.com Website:- www.nihva.com

	SIGN	DATE
DRAWN	OMKAR	22/11/17
CHECK	SHEKHAR	22/11/17
APPROVAL	SHEKHAR	22/11/17

CLIENT - FERRERO INDIA PVT. LTD.
PROJECT -
SITE - BARAMATI
DWG. NO. : NIHVA/17-18/0286 | REV-0
If any queries contact : design@nihva.com | SCALE: NTS | WT: | SHEET: 01 OF 01
ALL DIMENSION ARE IN mm