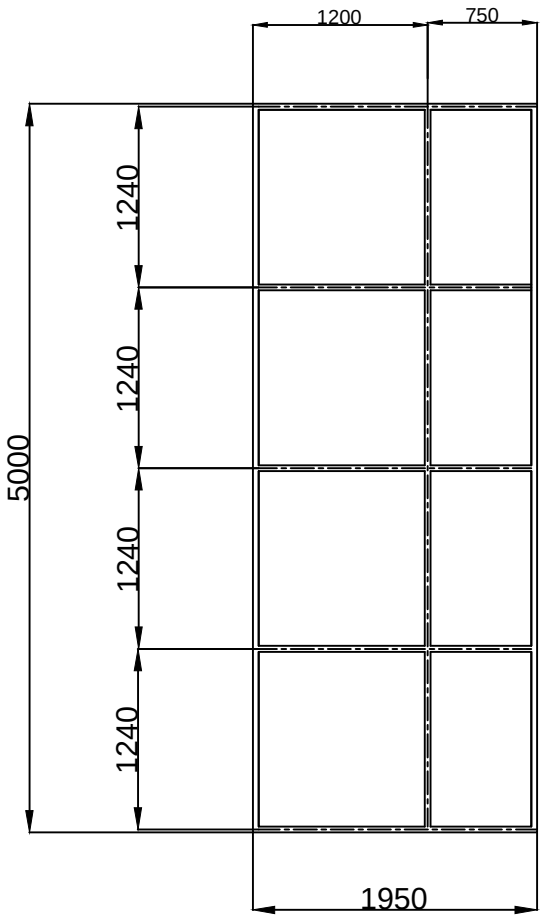

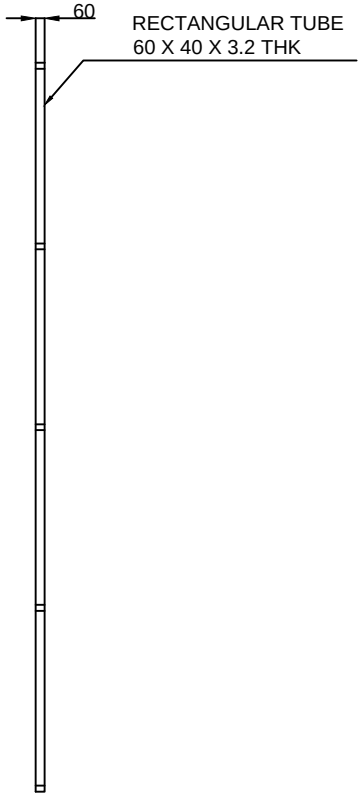

QTY=04 NOS

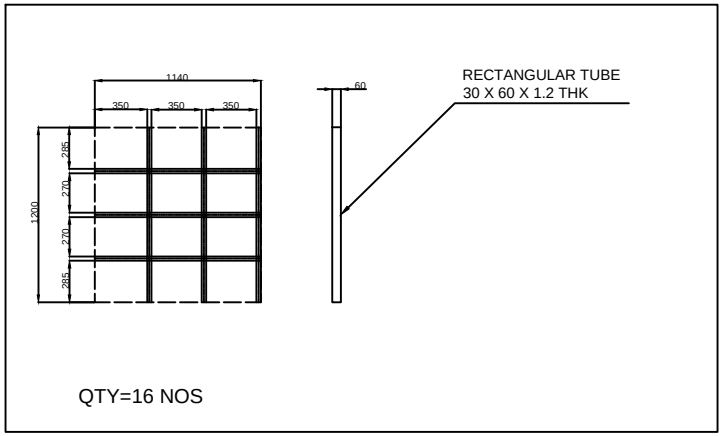

QTY=16 NOS

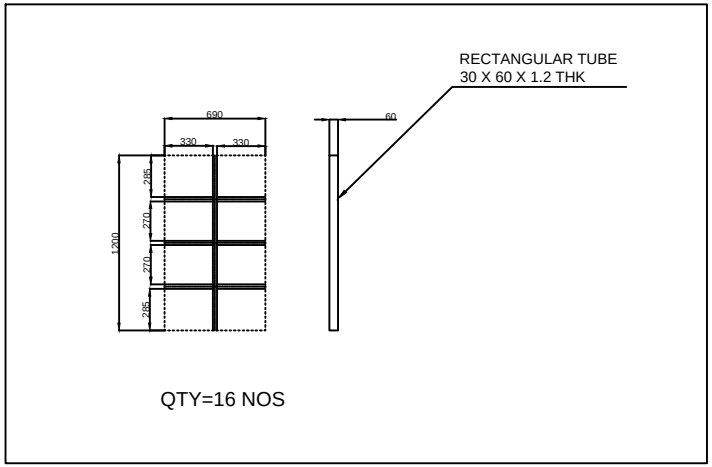

QTY=16 NOS

CRM DOOR 10

This drawing & design is the property of NIHVA TECHNOLOGIES. Not to be sold or copied to any other concern.

TITLE:- 4 LEAF CRM DOOR 10			NIHVA TECHNOLOGIES PVT. LTD. PUNE Tel : 020 66304033 Email:- info@nihva.com Website:- www.nihva.com
	NAME	DATE	SIGN
DRAWN	KISHAN	03/05/2022	
CHECK	M.SUTAR	03/05/2022	
APPRD.			
CLIENT - LESTECH			
LOCATION - POSCO MANGAON			
PRODUCT - SLIDING DOOR			
If any queries contact : design@nihva.com		DWG NO:-NIHVA/21-22/	REV- 0
ALL DIMENSION ARE IN mm		SCALE: NTS	SCALE:-- 1:1 SHEET: 01 OF 01

	Date	Revised By