
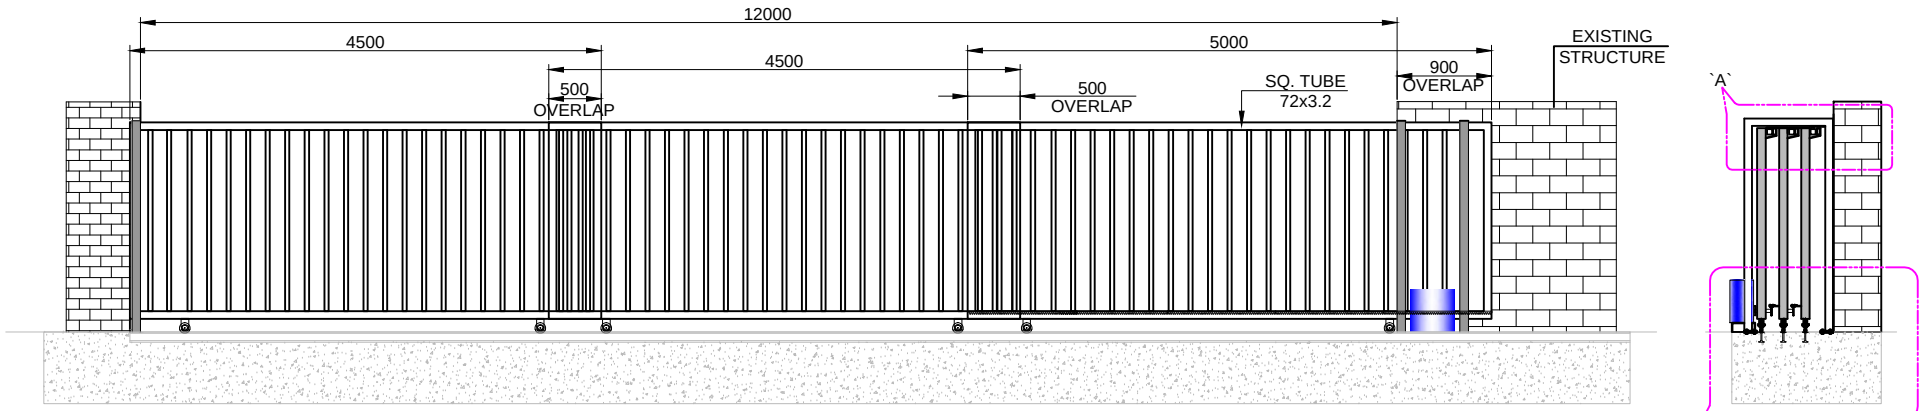
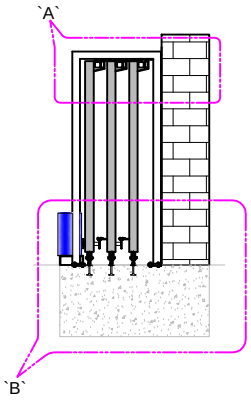
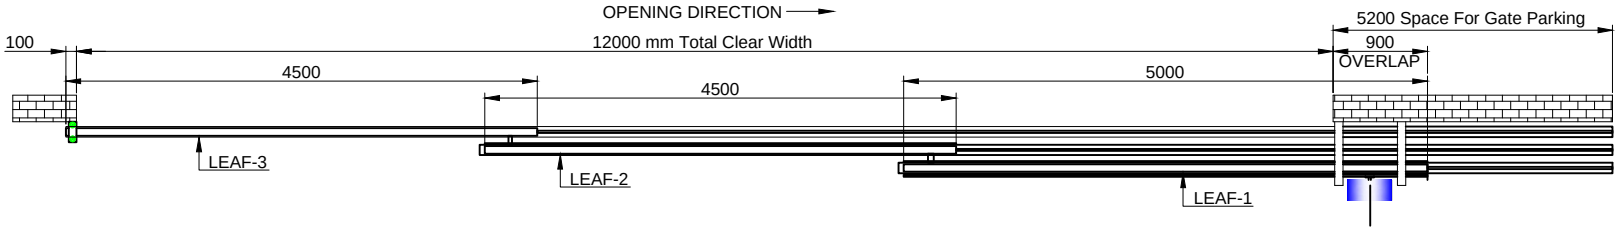
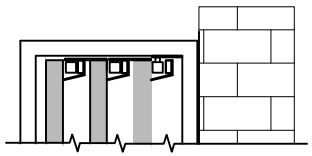


DETAIL -`A`

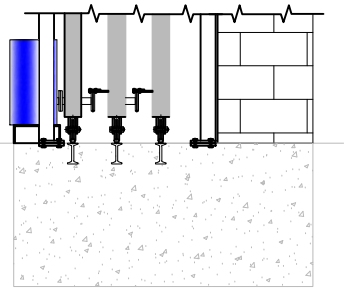

DETAIL- `B`

NOTE-
1. ALL REQUIRED CIVIL WORK WILL BE IN CLIENTS SCOPE.
3.GATE LEAF WILL BE IN TWO PARTS FOR TRANSPORTATION & WILL BE WELD TOGETHER ON SITE.

TOLERANCE - ±10mm

| CLEAR WIDTH | CLEAR HEIGHT | QUANTITY |
|---|---|---|
| 12000 | 2000 | 01 NOS |

| REV. | DESCRIPTION | DRAWN | DATE | REMARK |
|---|---|---|---|---|
| R01 | GATE TYPE CHANGED | AKASH | 24.01.19 | REMARK |

This drawing & design is the property of NIHVA TECHNOLOGIES. Not to be sold or copied to any other concern.

TITLE
SLIDING GATE

NIHVA TECHNOLOGIES PVT. LTD.

NIHVA TECHNOLOGIES PVT. LTD. PUNE
Tel : 020 66304033
Email:- info@nihva.com
Website:- www.nihva.com

| | NAME | SIGN | DATE |
|---|---|---|---|
| DRAWN | A.K. | | 21.01.2019 |
| CHECK | P.A. | | 21.01.2019 |
| APPRD. | R.D. | | 21.01.2019 |

CLIENT - ESR PUNE
PROJECT - BMW
SITE LOCATION - CHAKAN, PUNE.
If any queries contact : design@nihva.com
DWG. NO. : NIHVA/18-19/0251/R01 | REV- 01
ALL DIMENSION ARE IN mm
SCALE: NTS | WT: | SHEET: 01 OF 01