



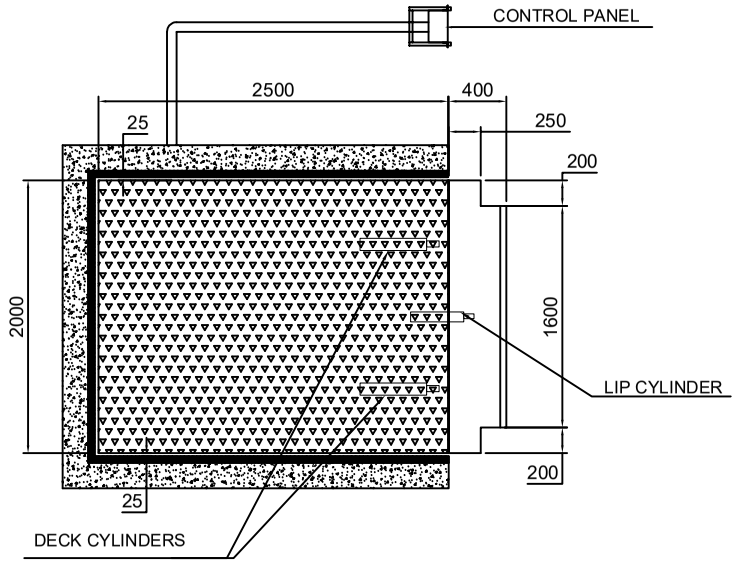


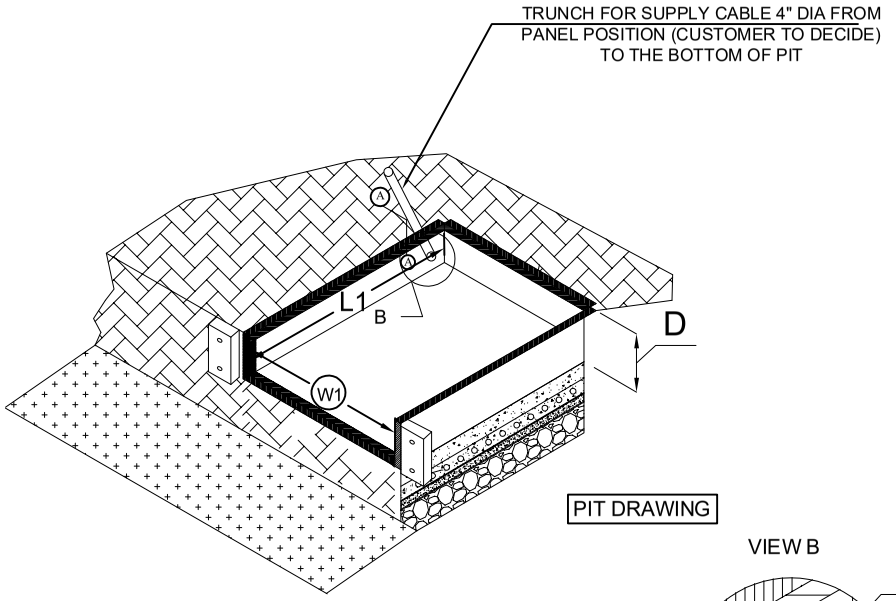

PIT DRAWING

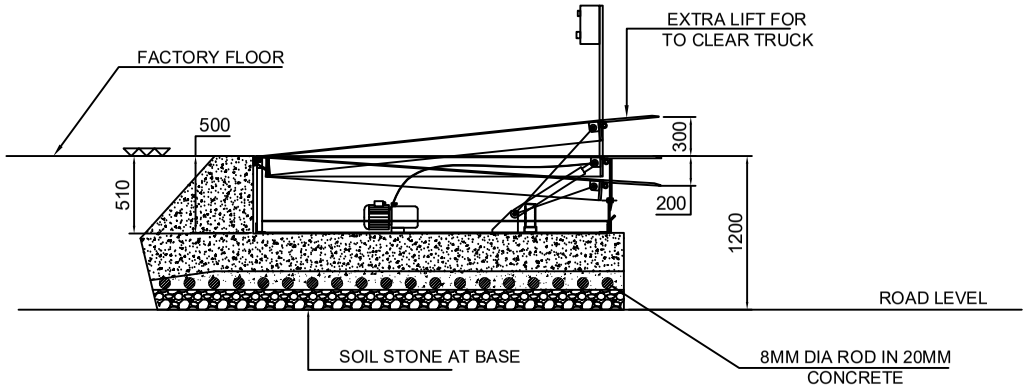

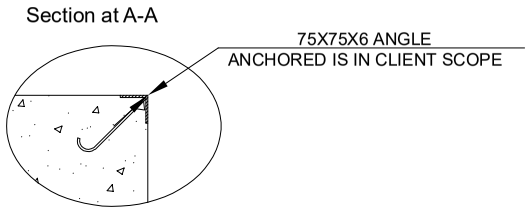

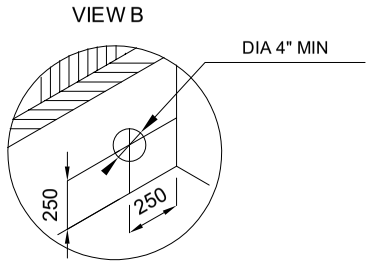

Capacity:- 10TON

DOCK LEVELER SIZE	WIDTH (W)	LENGTH (L)	HEIGHT (H)	LIP (C) LENGTH
	2000	2500	500	400
PIT DIMENSION	WIDTH (W 1)	LENGTH (L 1)	DEPTH (D)	
DL	2050	2510	5010	

NOTE:-

1. GIVEN GA DRAWING IS ONLY FOR THE QUOATION/CLIENT UNDERSTANDING PURPOSE, DIMENSION MAY VARY AS PER CONVENIENT
2. PROPER DRAINAGE SHOULD BE DONE
3. TRENCH AS SHOWN SHOULD BE MADE BY DECIDING THE POWER PACK POSITION.
4. LEVEL OF THE PIT SHOULD BE PLAIN AND SHOULD TAKE AT LEAST 18000 KG FLOOR LOADING
5. INSTALLLATION AND FABRICATION TOLERANCE FOR PLATFROM SIZE WILL BE ± 20 MM.
6. PIT,DUCT FOR HOSES & ALL CIVIL WORK IN CLIENT SCOPE
7. SURFACE FINISH: APPROVED RAL CODE.

Rev No.	Revision	Date	Revised By

This drawing & design is the property of NIHVA TECHNOLOGIES. Not to be sold or copied to any other concern.

TITLE:- DOCK LEVELER GA DRAWING

NIHVA TECHNOLOGIES PVT. LTD.

	NAME	DATE	SIGN
DRAWN	SUJATA	31/10/2022	
CHECK			
APPRD.			

PRODUCT - DOCK LEVELER

If any queries contact : design@nihva.com

DWG NO:-NIHVA/22-23/CLT/0152 REV- 0

ALL DIMENSION ARE IN mm

SCALE: NTS SCALE:-- 1:1 SHEET: 01 OF 01