


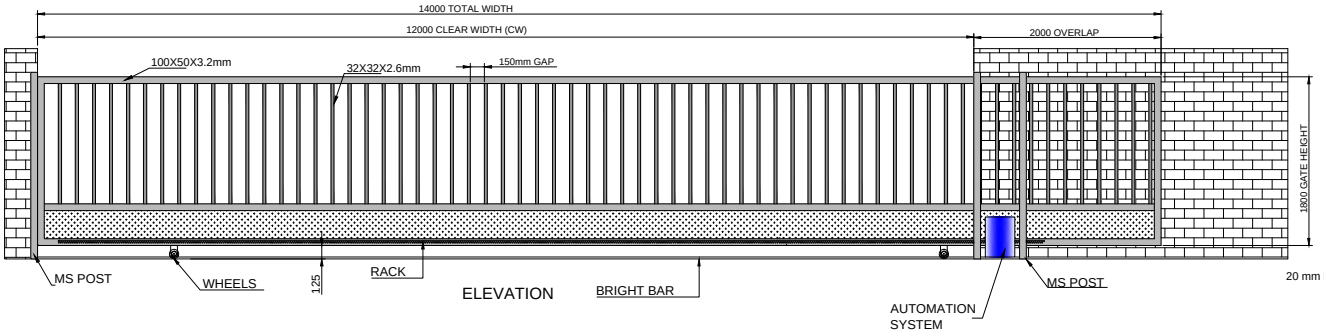


ELEVATION

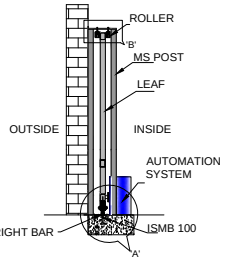


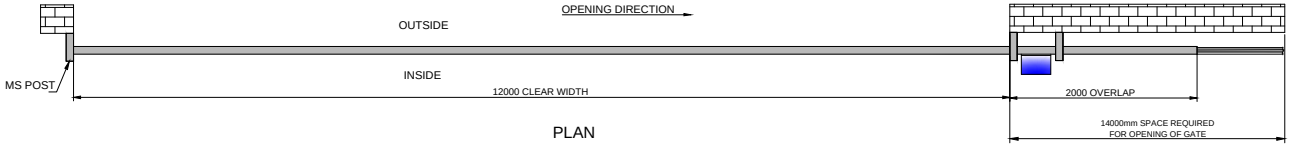

PLAN

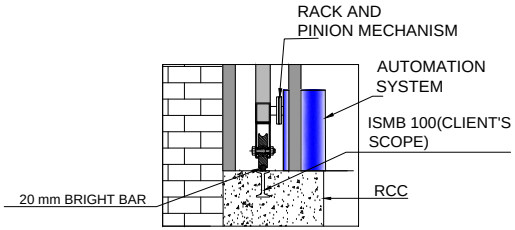

DETAIL VIEW OF A

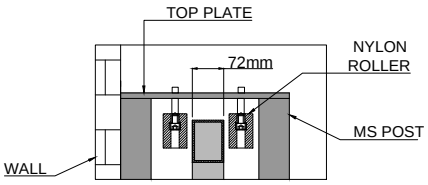

DETAIL VIEW OF B

SR NO	TUBE SPECIFICATION	
1	72X72X3.2mm MS TUBE	OUTER FRAME
2	32X32X2mm MS TUBE	INNER PATTERN
3	GAP BETWEEN TUBES	150mm
4	MS SHEET	MS SHEET
5	72X72X3.2mm MS TUBE	FOR POST

04	RAL 7035	LIGHT GREY
03	RAL 5002	ULTRAMARINE BLUE
02	RAL 9002	GREY WHITE
01	RAL 1004	GOLDEN YELLOW
SR.NO	RAL CODE	RAL COLOR

TOLERANCE:- ± 10mm

CLEAR WIDTH (CW)	CLEAR HEIGHT (CH)	QUANTITY
12000mm	1800mm	1 NOS

REV. NO	NAME	DATE	DESCRIPTION
R01	SURAJ	08-10-18	1.ADDED RAL CODE & NOTE

DIMENSION :

CLEAR WIDTH	CLEAR HEIGHT	QUANTITY
12000mm	1800mm	1 NOS

MATERIAL: MS

THICKNESS :

NOTE-
1. ALL REQUIRED CIVIL WORK WILL BE IN CLIENTS SCOPE.
2. ONE COAT OF RED OXIDE & TWO COAT OF APPROVED RAL SHADE WILL BE GIVEN TO THE GATE.
3.IF NECESSARY GATE LEAF WILL BE IN TWO PARTS FOR TRANSPORTATION & WILL BE WELD TOGETHER ON SITE.

NIHVA
NIHVA TECHNOLOGIES PVT. LTD.
Website:- www.nihva.com
NIHVA TECHNOLOGIES PVT. LTD. PUNE
Email:- info@nihva.com
TEL :020 66304033

TITLE:

AUTOMATIC SINGLE LEAF SLIDING GATE

CLIENT'S APPROVAL :

CLIENT - INOX

PROJECT -

SITE LOCATION -CHENNAI

DWG. NO. : NIHVA/18-19/0141/R01 REV. :-R01

SCALE: NTS WT: SHEET:1 OF 1

DRAWN	SURAJ		DATE: 06-10-18
CHECK	PRADEEP		DATE: 06-10-18
APPROVED	R.D		DATE: 06-10-18

IF ANY QUERIES CONTACT:- design@nihva.com

NOTE: ALL DIMENSIONS ARE IN mm

THIS DRAWING & DESIGN IS THE PROPERTY OF NIHVA TECHNOLOGIES. NOT TO BE SOLD OR COPIED TO ANY OTHER CONCERN.