


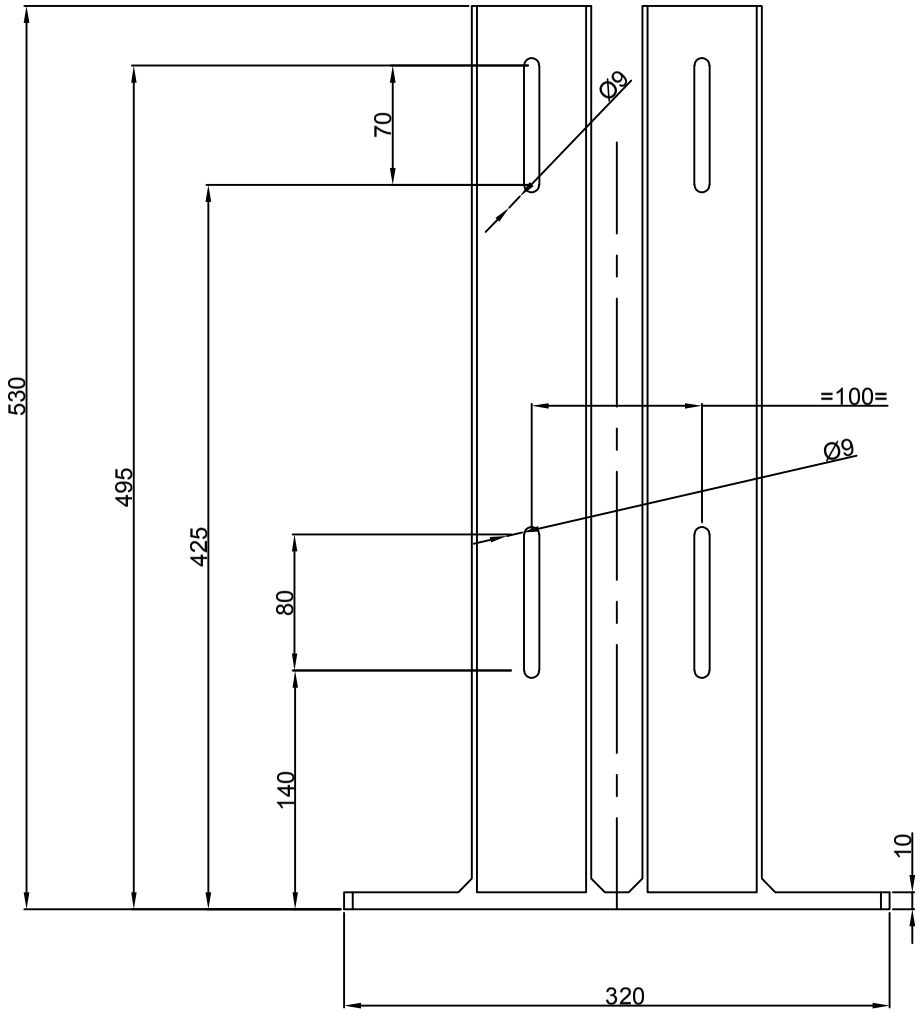

C CHANNEL FRAME-03
MATL-MS
QTY-01
DRG NO-01-03

SR NO.	REV NO.	Date	Revised By

TITLE:- C CHANNEL FRAME -03				NIHVA TECHNOLOGIES PVT. LTD. PUNE Tel : 020 66304033 Email:- info@nihva.com Website:- www.nihva.com	
	NAME	DATE	SIGN		
DRAWN	KISHAN	20/07/22		CLIENT - NIHVA TECHNOLOGIES PVT.LTD	
CHECK	G. JAIN	20/07/22		LOCATION -	
APPRD.	V. TARAK			PRODUCT - RETRACTABLE ROOF	
If any queries contact : design@nihva.com				DWG NO:-NIHVA/22-23/MFG/0036	REV- 0
ALL DIMENSION ARE IN mm				SCALE: NTS	SCALE:-- 1:1 | SHEET: 01 OF 01