


# PROPOSED PLAN LAYOUT

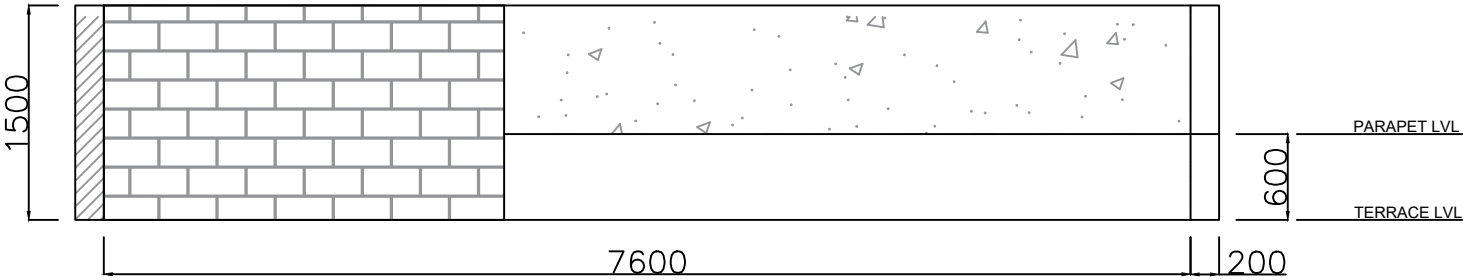


VIEW B

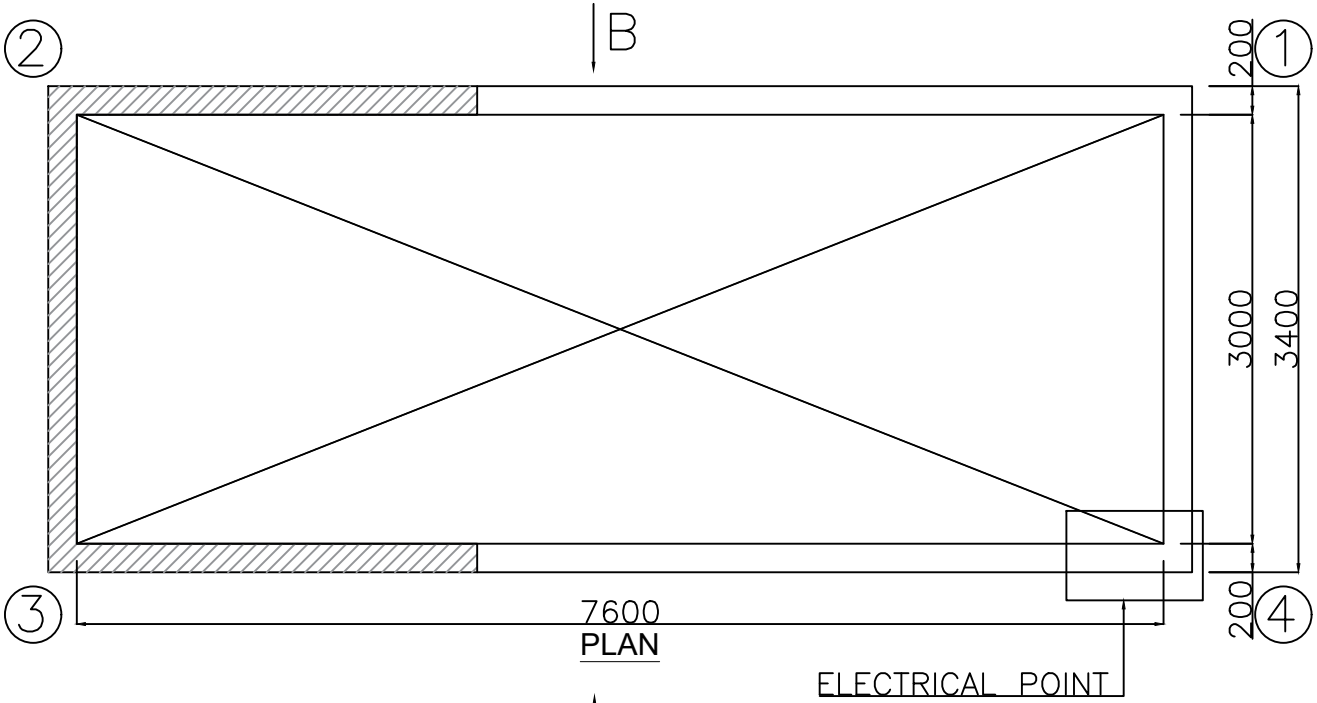



PLAN

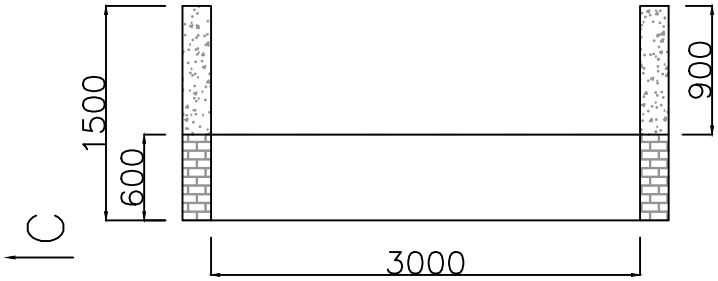


VIEW C

1. THE STRUCTURAL WALL ON BOTH SIDE 1-2 & 3-4 SHOULD BE RAISED TO THE HEIGHT OF 800 MM AROUND THE CUT OUT OF CONCRETE FOR PROPER FASTENING OF THE ROOF.
2. VERTICAL SURFACE 1-2, 2-3, 3-4, 4-1 SHOULD MAINTAIN SAME LEVEL ON BOTH THE ENDS SO TO MAINTAIN THE ALIGNMENT OF SYSTEM PROPERLY.
3. ELECTRICAL REQUIREMENT - 220V 5AMP SINGLE PHASE CONNECTION.
4. ALL DIMENSION IN MM.

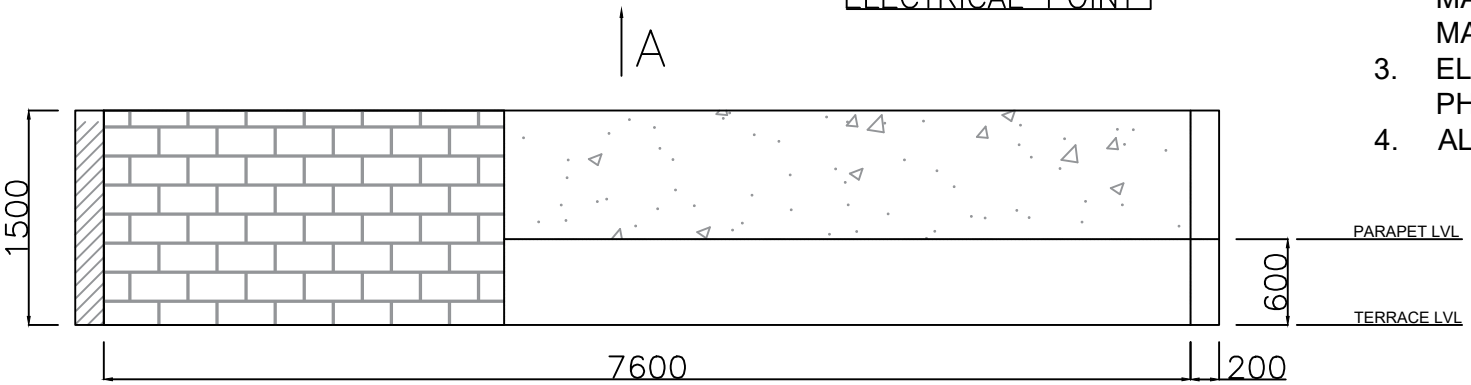


VIEW A

This drawing & design is the property of NIHVA TECHNOLOGIES. Not to be sold or copied to any other concern.

| TITLE | | | |
|---|---|---|---|
| PROPOSED LAYOUT PLAN | | | |
| | NAME | SIGN | DATE |
| DRAWN | G.J. | | 11.05.22 |
| CHECK | A.K. | | 11.05.22 |
| APPRD. | V.T. | | 11.05.22 |
| If any queries contact : projectsautomation@nihva.com | | | |
| ALL DIMENSION ARE IN mm | | | |

NIHVA TECHNOLOGIES PVT. LTD.
NIHVA TECHNOLOGIES PVT. LTD. PUNE
Tel : 020 66304033
Email:- info@nihva.com
Website:- www.nihva.com

| | | |
|---|---|---|
| CLIENT - VADILAL INDUSTRIES LTD. | | |
| LOCATION - NEW DELHI_IN | | |
| PRODUCT - RETRACTABLE ROOF | | |
| NIHVA\21-22\0006 | | REV- 0 |
| SCALE: NTS | | SHEET: 01 OF 01 |