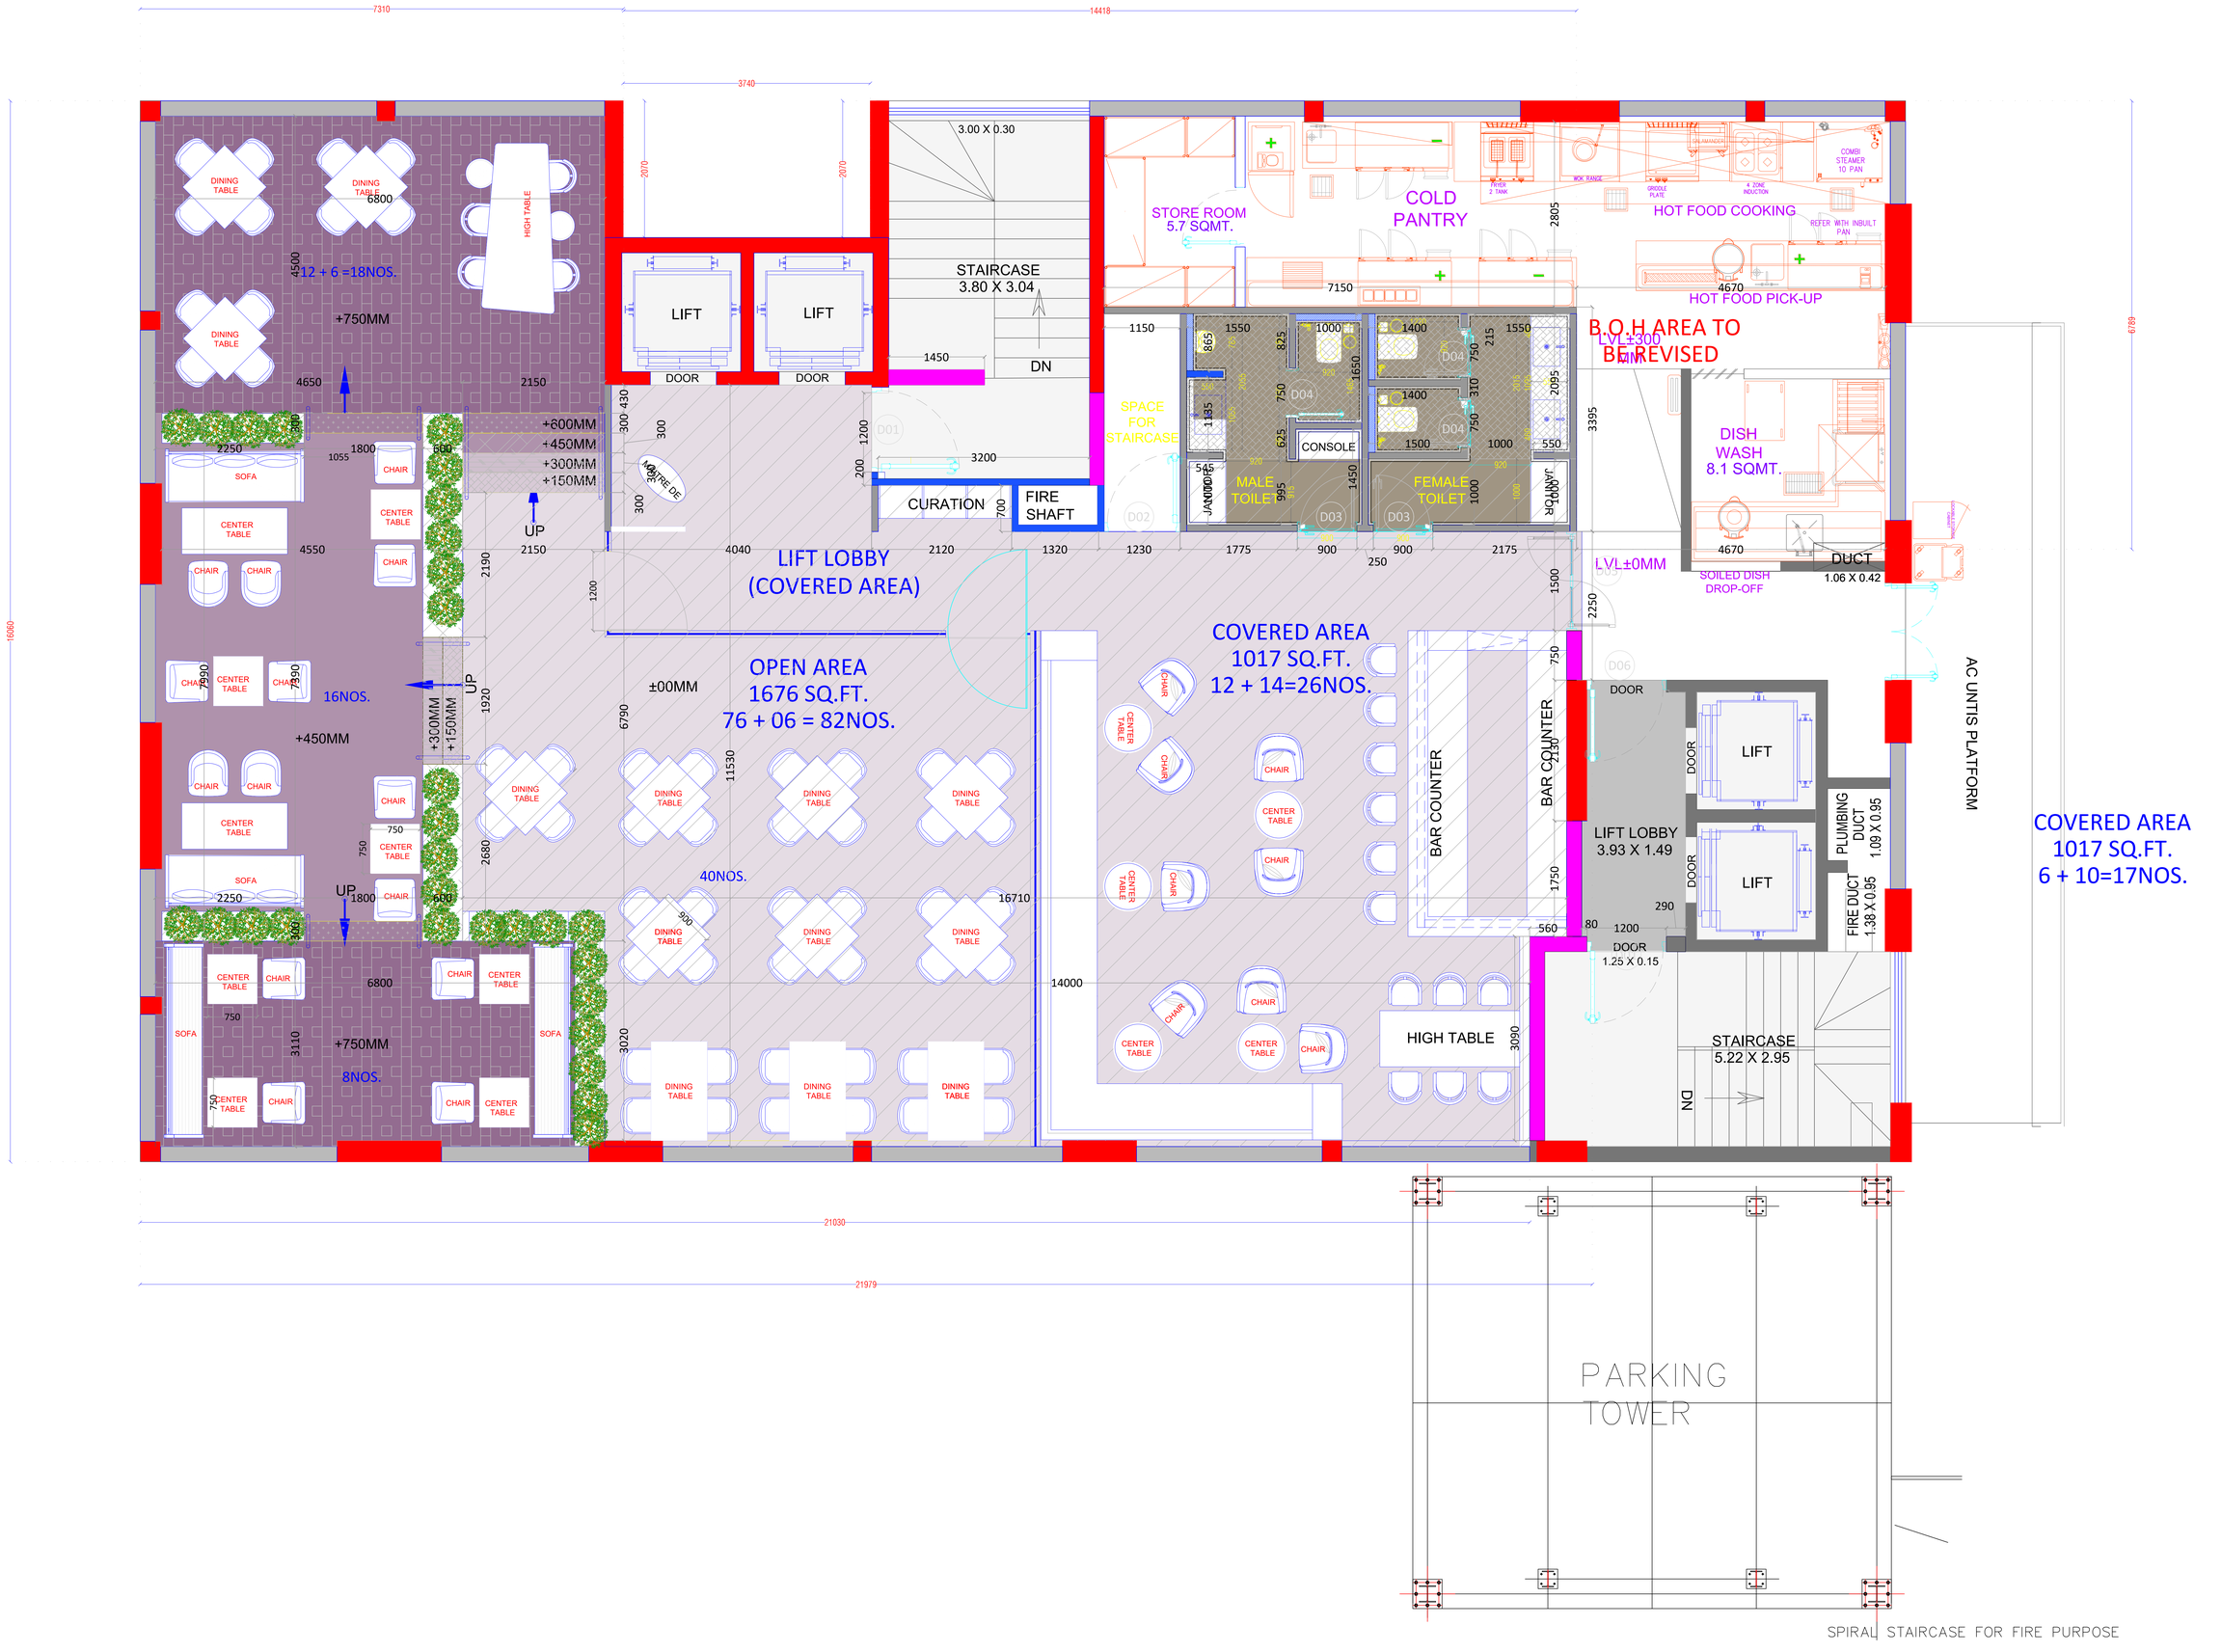

7310
14418
3740
16600
6789
DINING TABLE
6800
HIGH TABLE
12 + 6 =18NOS.
4500
+750MM
4650
2150
LIFT
LIFT
DOOR
DOOR
2070
2070
3.00 X 0.30
STAIRCASE
3.80 X 3.04
DN
1450
STORE ROOM
5.7 SQMT.
COLD
PANTRY
HOT FOOD COOKING
HOT FOOD PICK-UP
B.O.H AREA TO
BE REVISED
LVL±300
MIN
SPACE
FOR
STAIRCASE
CONSOLE
MALE
TOILET
FEMALE
TOILET
DISH
WASH
8.1 SQMT.
SOILED DISH
DROP-OFF
DUCT
1.06 X 0.42
LVL±0MM
+600MM
+450MM
+300MM
+150MM
UP
SOFA
CHAIR
CENTER TABLE
CURATION
FIRE
SHAFT
3200
LIFT LOBBY
(COVERED AREA)
OPEN AREA
1676 SQ.FT.
76 + 06 = 82NOS.
±00MM
COVERED AREA
1017 SQ.FT.
12 + 14=26NOS.
16NOS.
+450MM
+300MM
+150MM
40NOS.
8NOS.
+750MM
BAR COUNTER
LIFT LOBBY
3.93 X 1.49
DOOR
LIFT
LIFT
PLUMBING
DUCT
1.09 X 0.95
FIRE DUCT
1.38 X 0.95
DOOR
1.25 X 0.15
STAIRCASE
5.22 X 2.95
DN
AC UNTIS PLATFORM
COVERED AREA
1017 SQ.FT.
6 + 10=17NOS.
16710
14000
21030
21979
PARKING
TOWER
SPIRAL STAIRCASE FOR FIRE PURPOSE