

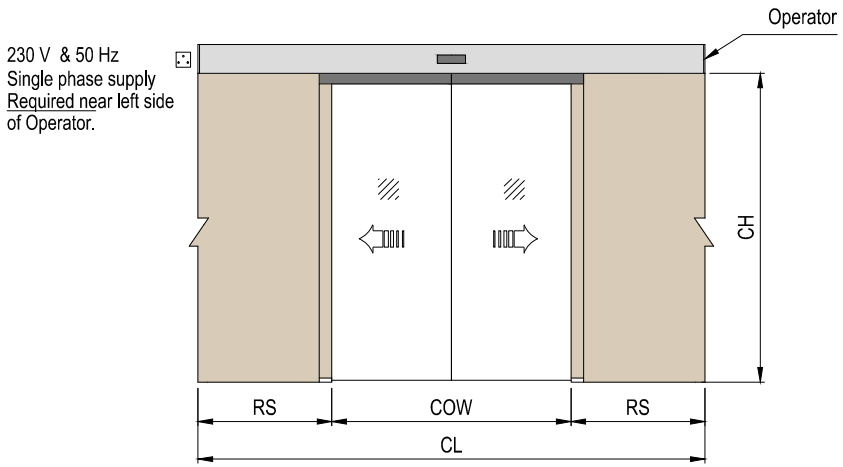



Inside Elevation

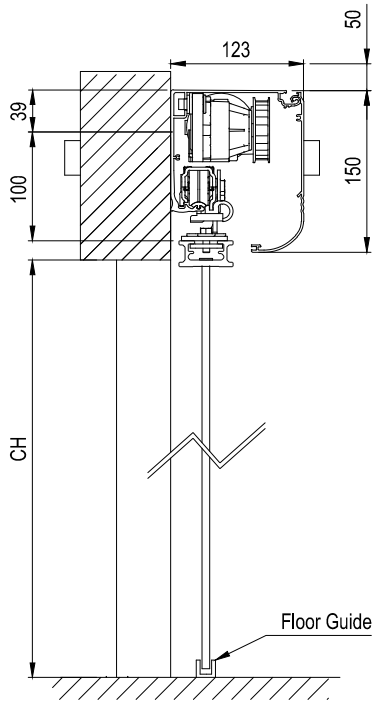

Fixing Plan

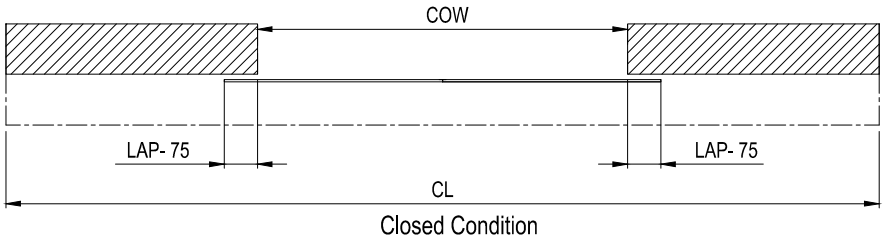

Closed Condition

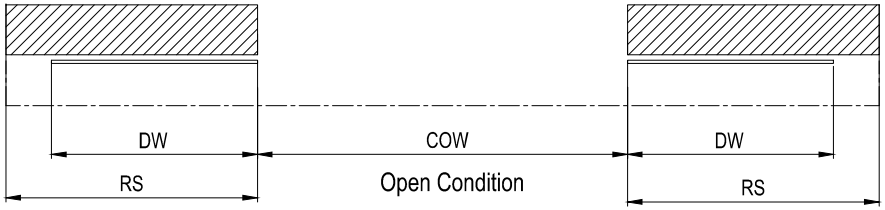

Open Condition

Plan

Sr. No.	(COW) CLEAR OPEN WIDTH	(CH) CLEAR HEIGHT	(CL) CLEAR LENGTH	(DW) DOOR WIDTH	(RS) REQ. SPACE	QTY
1	3000	3000	6350	1575	1675	1
2	2000	3000	4350	1075	1175	1

NOTE : Glass Type- 12mm Toughened

This drawing & designing is the property of NIHVA TECHNOLOGIES. Not to be sold or copied to any other concern.

TITLE: AUTOMATIC GLASS SLIDING DOOR SL 500

NIHVA TECHNOLOGIES PVT. LTD.
NIHVA TECHNOLOGIES PVT. LTD. PUNE
Tel : 020 66304033
Email:- info@nihva.com
Website:- www.nihva.com

	NAME	SIGN	DATE
DRAWN	PRADEEP		21.08.2018
CHECK	VIKRANT		21.08.2018
APPROVAL	R.D		21.08.2018
REV.	00		

CLIENT - DEVI CONSTRUCTION
PROJECT -
SITE - PUNE
DWG. NO. : NIHVA/18-19/0104
If any queries contact : design@nihva.com
SCALE: NTS | WT: | SHEET: 01 OF 01
ALL DIMENSION ARE IN mm