
PROPOSED PLAN LAYOUT

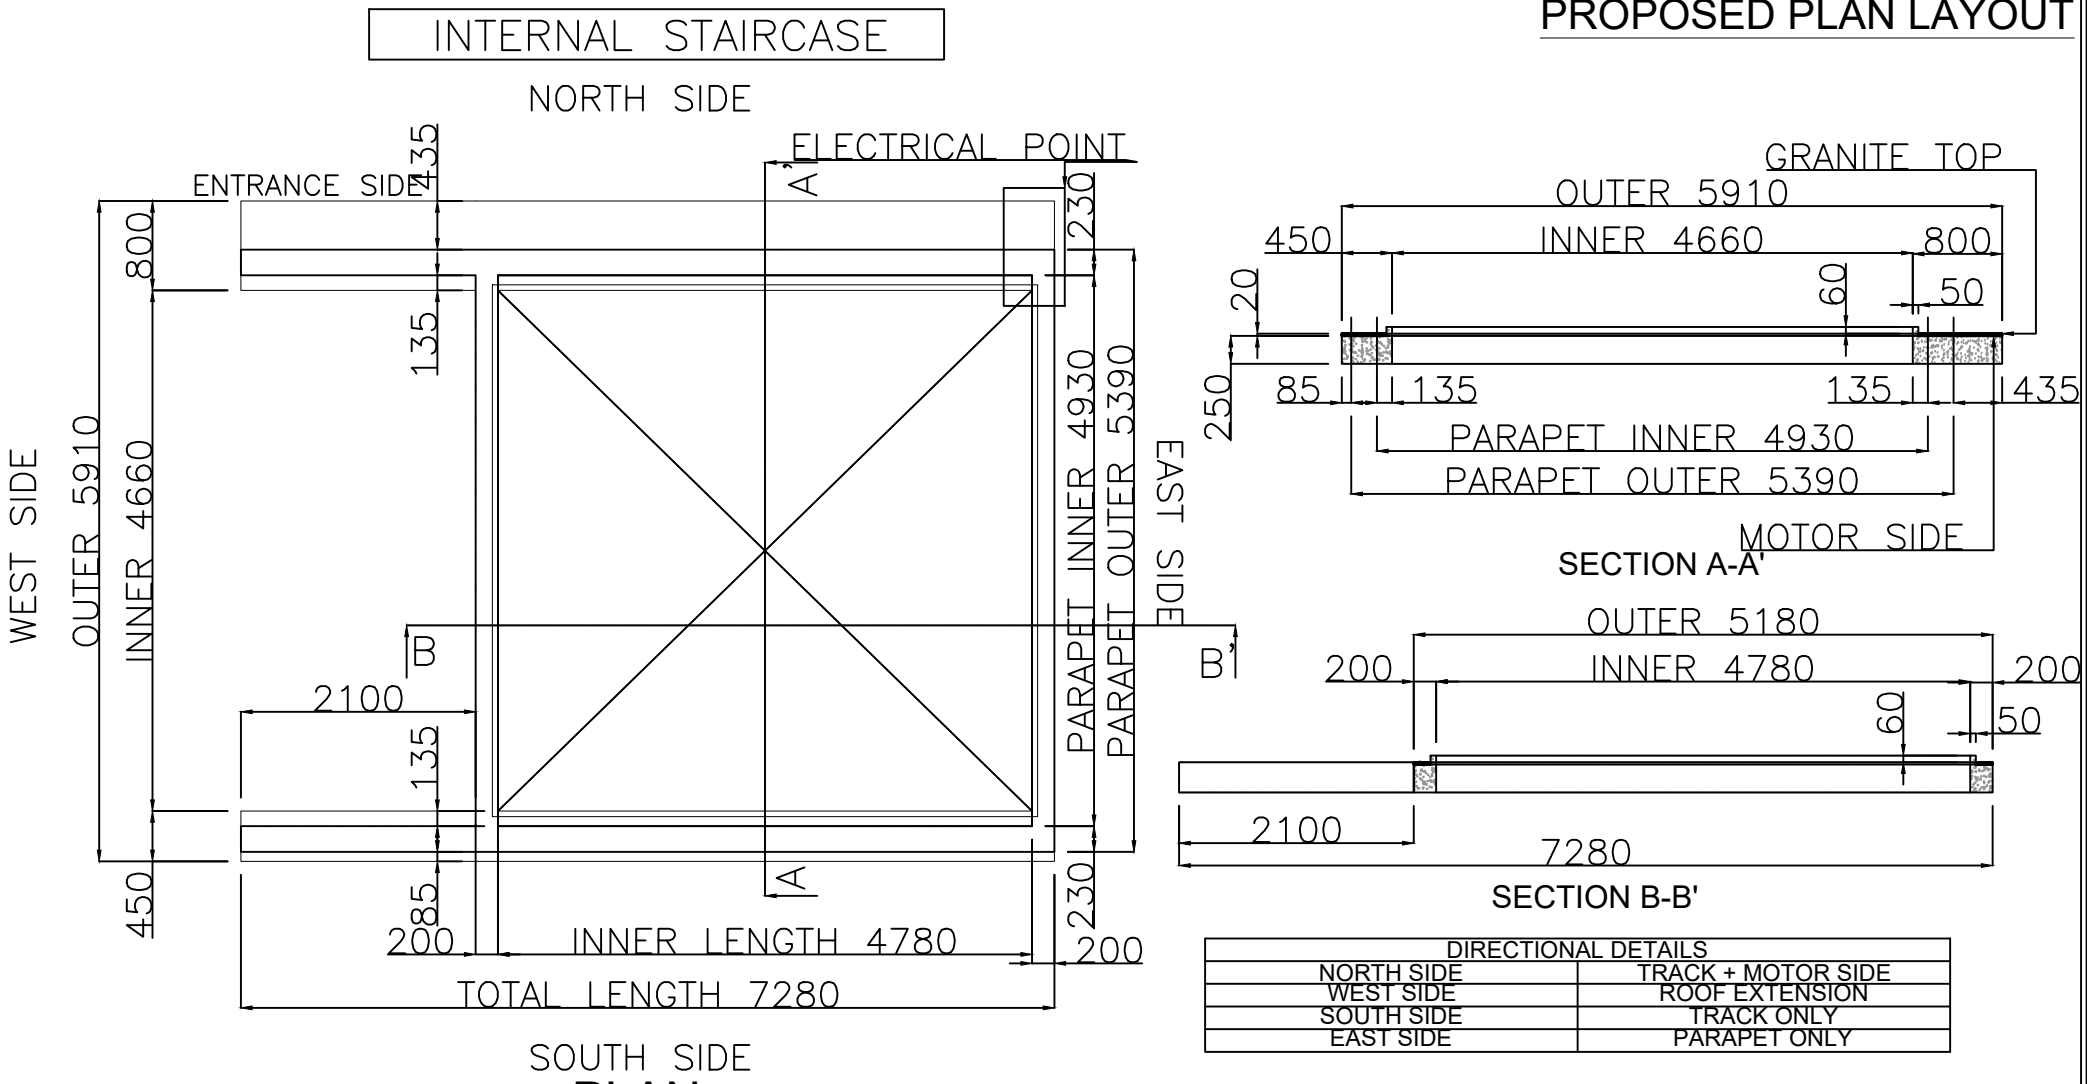

DIRECTIONAL DETAILS	
NORTH SIDE	TRACK + MOTOR SIDE
WEST SIDE	ROOF EXTENSION
SOUTH SIDE	TRACK ONLY
EAST SIDE	PARAPET ONLY

1. THE STRUCTURE AROUND THE CUT OUT SHOULD BE OF CONCRETE FOR PROPER FASTENING OF SLIDING ROOF.
2. INNER PROJECTION OF 50X60MM REQUIRED AS A SINGLE STRUCTURE WITHOUT ANY JOINT TO AVOID WATER SEEPAGE INSIDE.
3. TOP SURFACE SHOULD BE OF GRANITE 20MM FOR SMOOTH FUNCTIONING OF ROOF.
4. GRADIENT OF 50MM NEED TO BE PROVIDED ALONG THE OUTER LENGTH TO AVOID WATER STAGNANCY IN GUIDE RAIL.
5. WE REQUIRE 250 MM HIGH CONCRETE FOR ANCHORING THE ROOF FROM THE BASE.
6. ROOF EXTENSION OF 2100 MM REQUIRED FOR COMPLETE STACKING OF PANELS.
7. ELECTRICAL CONNECTION - 5 AMP, 220V SINGLE PHASE.
8. ALL DIMENSION ARE IN MM.