


Gate Open Position

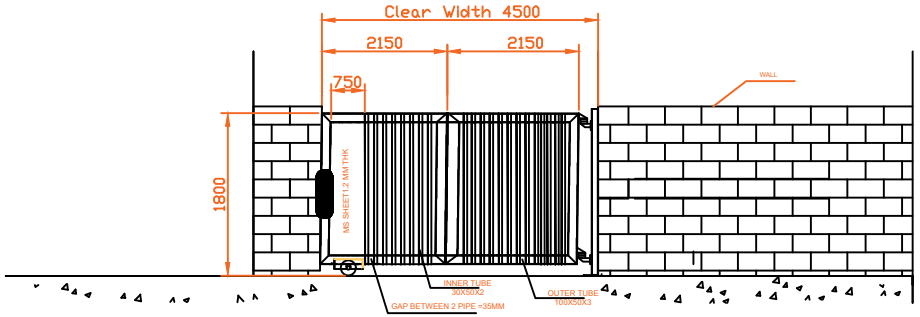

Gate Close Position

Opening Direction(View from inside)

CW =4500 MM
CH =1800 MM

Note:-

1.All Dimension are in MM

2.Required All civil work will be in Client scope

3.Installlation and Fabrication tolerance will be ±20mm

4. Required Parking will be 700 mm

This drawing & design is the property of NIHVA TECHNOLOGIES. Not to be sold or copied to any other concern.

TITLE:- Sliding Folding Gate			NIHVA TECHNOLOGIES PVT. LTD. PUNE Tel : 020 66304033 Email:- info@nihva.com Website:- www.nihva.com
	NAME	DATE	SIGN
DRAWN	Jayesh	22/11/23	CLIENT - Yashraj Infra Pvt.Ltd.
CHECK	A.K.	22/11/23	LOCATION - Baramati
APPRD.	V.T.	22/11/23	PRODUCT - Sliding Folding Gate QTY-01
If any queries contact : design@nihva.com			DWG NO:- NIHVA23-24 REV-00
ALL DIMENSION ARE IN mm			SCALE:NTS SCALE:-- 1:1 SHEET: 01 OF 01