

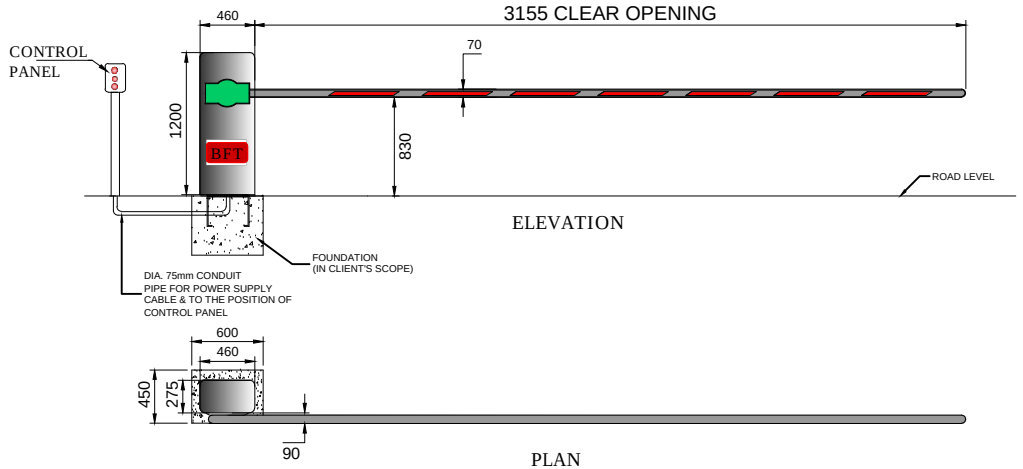


ELEVATION

PLAN

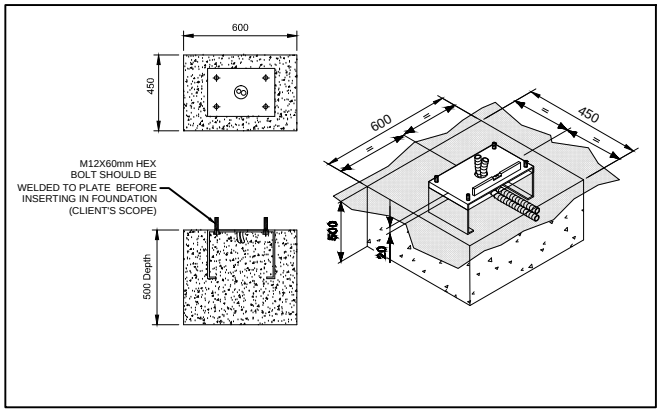

FOUNDATION DETAILS (IN CLIENT'S SCOPE)

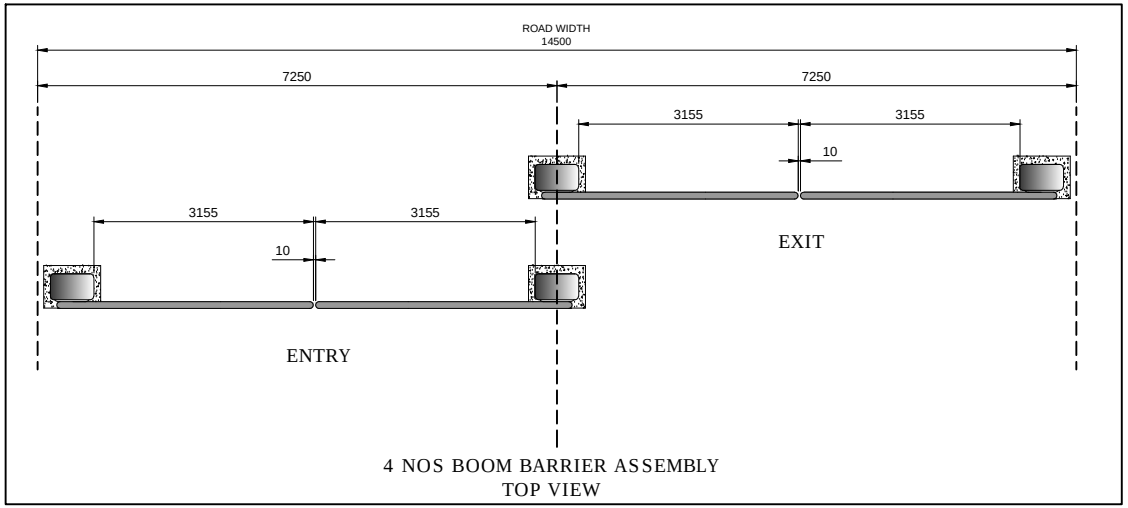

4 NOS BOOM BARRIER ASSEMBLY
TOP VIEW

REV NO	DATE	DRAWN	REMARK
R02	09.06.20	P.A	1. DIMENSION CHANGE
R01	03.06.20	P.A	1. DETAIL VIEW ADDED

TOLERANCE - ±10mm

This drawing & design is the property of NIHVA TECHNOLOGIES. Not to be sold or copied to any other concern.

TITLE
BOOM BARRIER

	NAME	SIGN	DATE
DRAWN	P.A		14.04.2020
CHECK	G.J		14.04.2020
APPROVAL			

If any queries contact : projects@nihva.com

ALL DIMENSION ARE IN mm

NIHVA TECHNOLOGIES PVT. LTD. PUNE
Tel : 020 66304033
Email:- info@nihva.com
Website:- www.nihva.com

CLIENT - SEZ BIOTECH SERVICES PVT LTD

PROJECT -

SITE LOCATION - MANJARI BK, PUNE

DWG. NO. : NIHVA/ 20-21/0002/R02 | REV-R02

SCALE: NTS | WT: | SHEET: 01 OF 01