


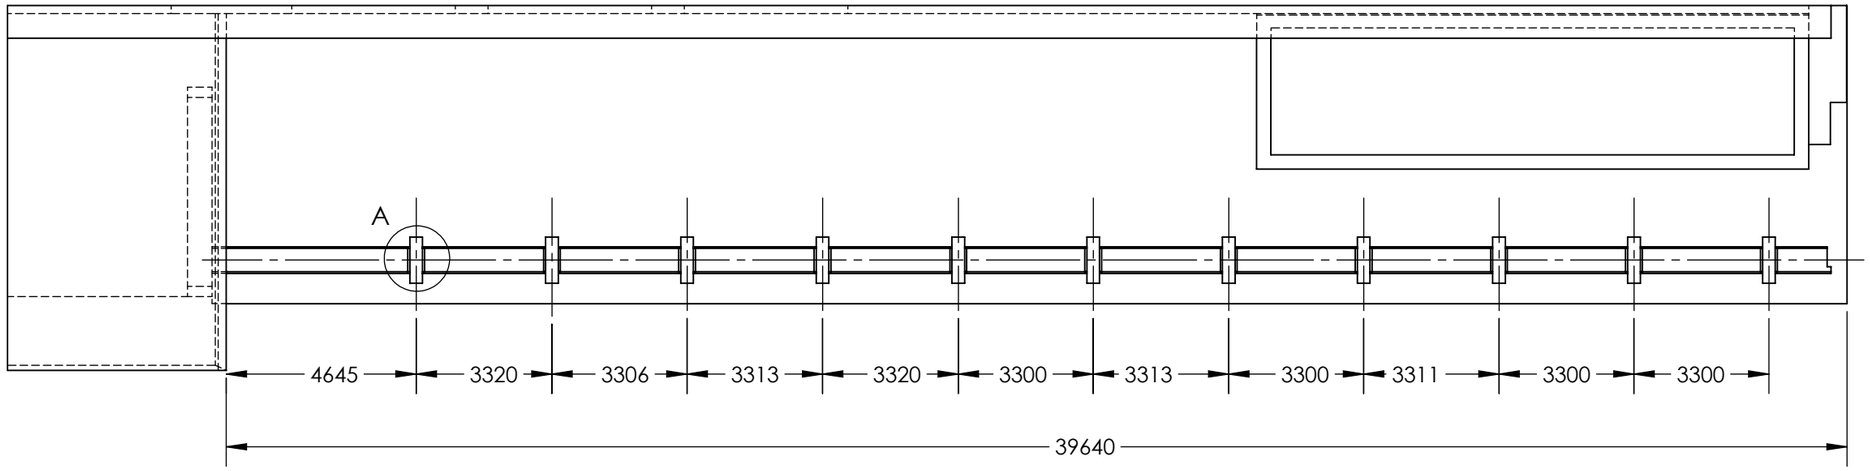


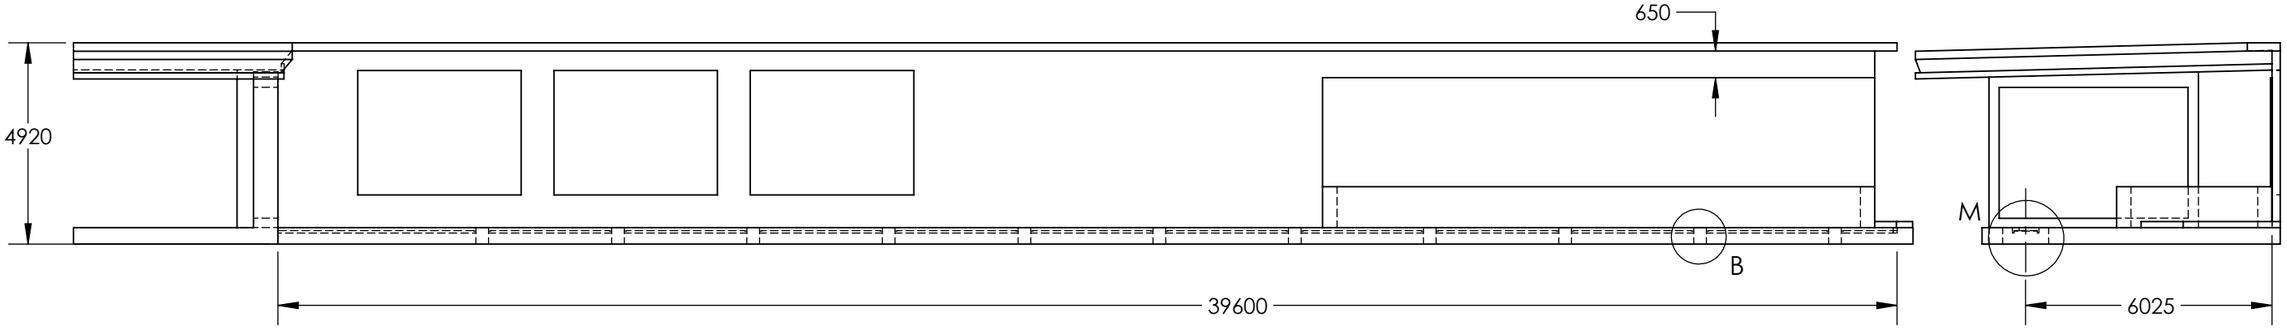


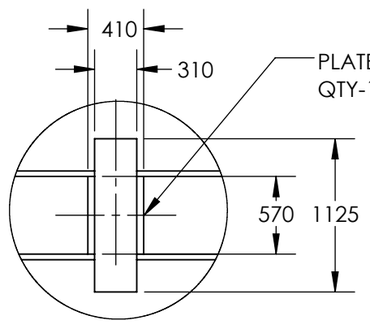

DETAIL A

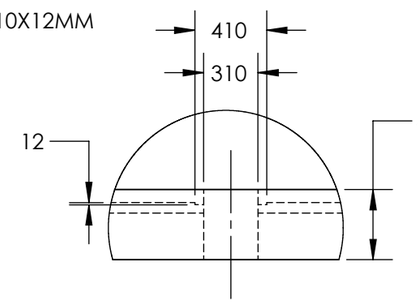

DETAIL B

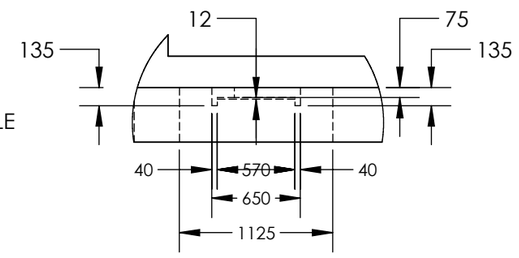

DETAIL M

TITLE - CIVIL WORK				NIHVA TECHNOLOGIES PVT.LTD.PUNE Website - www.nihva.com
	NAME	SIGNATURE	DATE	CLIENT - RSGL
DRAWN	D.V.		18.05.2023	PRODUCT - BALCONY ENCLOSER
CHK'D	P.M.		18.05.2023	SITE LOCATION -
APPV'D	V.T.		18.05.2023	
if any queries contact - supportautomation@nihva.com				DWG NO - NIHVA/22-23/00XX / REVISION -
ALL DIMENSION ARE IN mm			A3	SCALE - / SHEET 1 OF 2