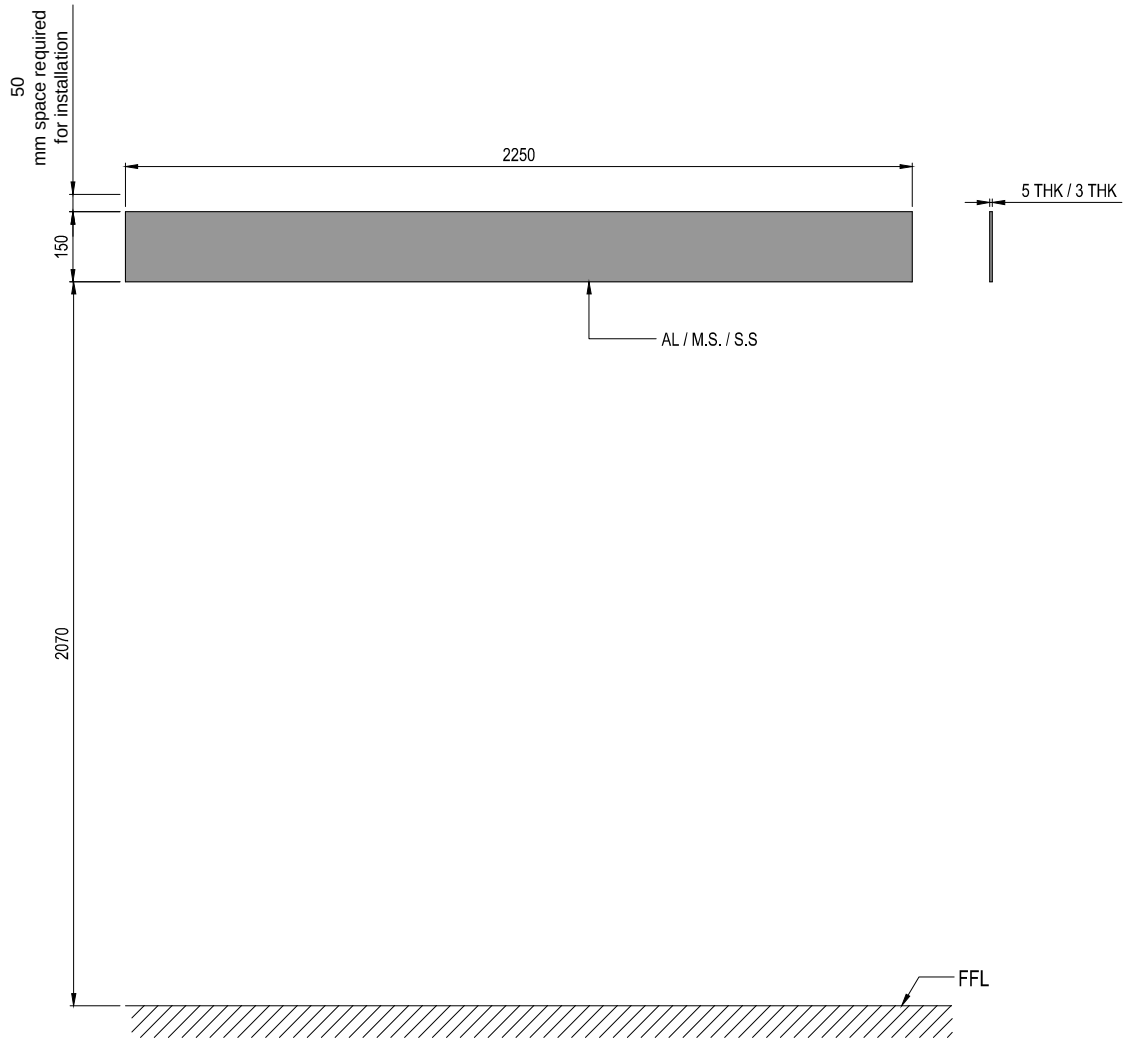


DIMENSION :		
CLEAR WIDTH	CLEAR HEIGHT	QUANTITY
2250	150	5

MATERIAL :

THICKNESS :

NOTE:
1.REQUIRED STRUCTURE WILL BE CLIENT SCOPE.
2.SINGLE PHASE.3CORE 1.5 SQ. CABLE REQUIRED AT SITE(CLIENT SCOPE).

NIHVA
NIHVA TECHNOLOGIES PVT. LTD.
NIHVA TECHNOLOGIES PVT. LTD. PUNE
Email:- info@nihva.com
Website:- www.nihva.com

TITLE:

STRUCTURE FOR BESAM SL-500
AUTOMATIC SLINDING DOOR

CLIENT'S APPROVAL :

CLIENT -FERRERO INDIA PVT. LTD

PROJECT -

SITE LOCATION - BARAMATI.

DWG. NO. : NIHVA/17-18/0231

SCALE: NTS	WT:	SHEET:1 OF 1

DRAWN BY: SURAJ	DATE: 07-10-2017
CHECK BY: SHEKHAR	DATE: 07-10-2017
APPROVED BY :SHEKHAR	DATE: 07-10-2017

If any queries contact : projects@nihva.com

NOTE: ALL DIMENSIONS ARE IN mm

THIS DRAWING & DESIGNING IS THE PROPERTY OF NIHVA TECHNOLOGIES. NOT TO BE SOLD OR COPIED TO ANY OTHER CONCERN.

NOTE FOR STRUCTURE MATERIAL: IF ALUMINUM TUBE /PLATE IS TO BE USED, THE THICKNESS WILL BE 5 MM.
IF M.S./S.S./ TUBE TO BE USED, THE THICKNESS WILL BE 3 MM

CLEAR WIDTH	CLEAR HEIGHT	QUANTITY
2250	150	05