

REV.	DWG NO		TITLE
XX	XXXX	1 / 1	TITLE


DECK CYLINDER
02 NOS

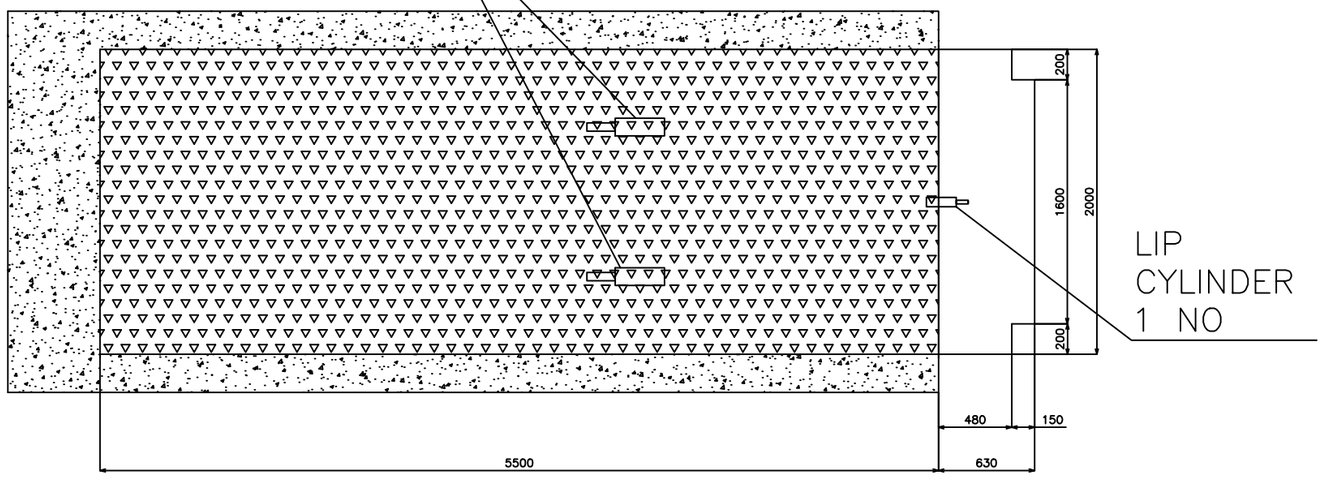

LIP
CYLINDER
1 NO

EXTRA LIFT PROVIDE TO
CLEAR TRUCK

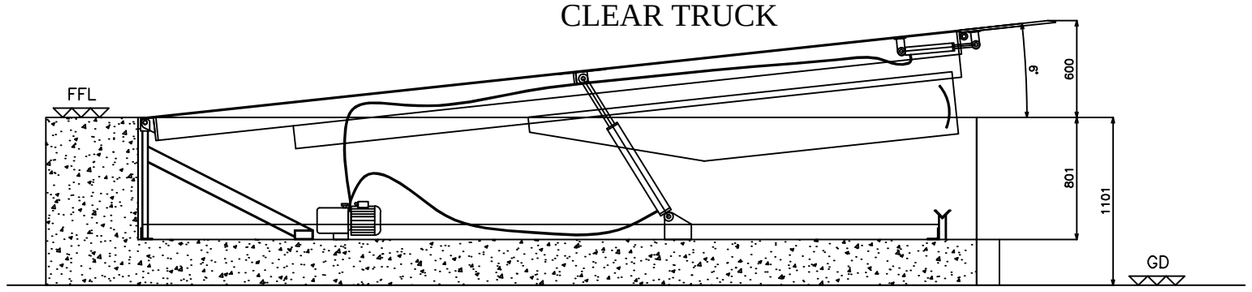

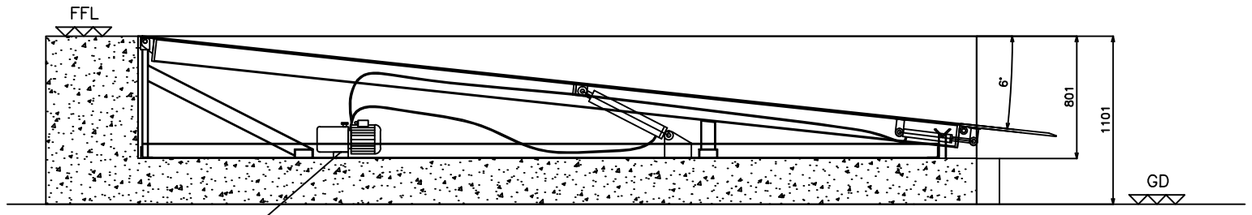

1 HP,3 Phase HYDRAULIC
POWER PACK
(ANCHORED ON PCC FLOOR)

NOTE: –

1. PROPER DRAINAGE SHOULD BE DONE.
2. FABRICATION TOLERANCE FOR PLATFORM SIZE WILL BE + 10 MM.
3. PLEASE NOTE THAT THE CAPACITY OF DOCK LEVELER (6 TON) CONSIDERED IS THE CAPACITY AFTER THE LIP IS RESTED ON THE VEHICLE.
4. CYLINDERS PROVIDED ARE INDENTED TO BE USED ONLY FOR LIFTING OF BARE DOCK & CAN NOT LIFT OTHER LOADS.

Drawing/ Document Category (Submission Purpose)	Drawing/Document Review Status (BY OWNER/PMC)		
	APPROVAL CODE	STATUS	ACTION REQUIRED
☑ For Approval	1	Rejected	Revise and resubmit
☐ For Review	2	Commented as noted	Work may proceed subject to acceptance and incorporation of comments.
☐ For Information	3	Acceptable with minor comments	Incorporate comments, if any. Resubmit as certified final.Work may proceed.
	4	Approved with No comments–FINAL	Work may proceed.
	5	Information Only	Accepted for information only.Work may proceed.

Date: __/__/____ Name : _____

This approval does not absolve the CONTRACTOR from meeting their contractual obligations of delivering a complete safe and efficiently operating unit facilities meeting all requirements of the contract.

					/ /
					/ /
					/ /
A1	ISSUED FOR APPROVAL	PRADEEP	GAURAV	AMIT	19/02/2020
REV	PURPOSE	PREPARE	CHKD	APPROVAL	DATE dd/mm/yy

L&T - CHIYODA LIMITED

- ☐ REVIEW CODE 1 – REJECTED
  REVISE & RESUBMIT.
- ☐ REVIEW CODE 2 – COMMENTED AS NOTED. WORK MAY PROCEED SUBJECT TO ACCEPTANCE AND INCORPORATION OF COMMENTS.
- ☐ REVIEW CODE 3 – ACCEPTABLE WITH MINOR COMMENTS
  INCORPORATE COMMENTS, IF ANY. RESUBMIT AS CERTIFIED FINAL. WORK MAY PROCEED.
- ☐ REVIEW CODE 4 – APPROVED WITH NO COMMENTS – FINAL
  WORK MAY PROCEED.
- ☐ REVIEW CODE 5 – INFORMATION ONLY
  ACCEPTED FOR INFORMATION ONLY. WORK MAY PROCEED.

COMMENTED BY	REVIEWED BY	APPROVED BY	DATE

THIS REVIEW / APPROVAL DOES NOT RELIEVE THE VENDOR / MANUFACTURER OF THE FULL RESPONSIBILITY AS TO DESIGN CORRECTNESS OF DIMENSIONS & COMPLIANCE WITHALL APPLICABLE REGULATIONS AND WITH THE REQUIREMENTS MADE IN PURCHASER SPECIFICATIONS.

PROJECT
ETHYLENE GLYCOL PROJECT
PARADIP REFINERY, ODISHA-INDIA.

OWNER
INDIAN OIL CORPORATION LIMITED
PARADIP REFINERY, ODISHA, INDIA

This Drawing is the Property of INDIAN OIL CORPORATION LTD and is lent without consideration other than the Borrower's agreement that it shall not be reproduced, copied lent or disposed of directly or indirectly, nor used for any purpose other than that for which it is specifically furnished. The apparatus shown in the drawing is covered by patents information contained in this drawing may be proprietary to Indian Oil Corporation Ltd and/or licensors, and is subject to obligations of confidentiality.

PMC
Toyo Engineering India Private Limited
Mumbai, India

TEPL's Job No. 6389 WORK ORDER No. 25574423

LSTK–2
L&T Hydrocarbon Engineering

LSTK–2 Job No. IOCL–O&U WORK ORDER No. LATER

DETAILED ENGINEERING CENTER: L&T - CHIYODA LIMITED

TITLE UNIT NO–207D

DATA SHEET WITH GAD FOR
DOCK LEVELER

SCALE 1:1 | DWG. NO. IPEG–6389–NTPL(1)–8470–DS–2070–0001 | REV. 1/1 | A1

CAD FILE REF: CFR