
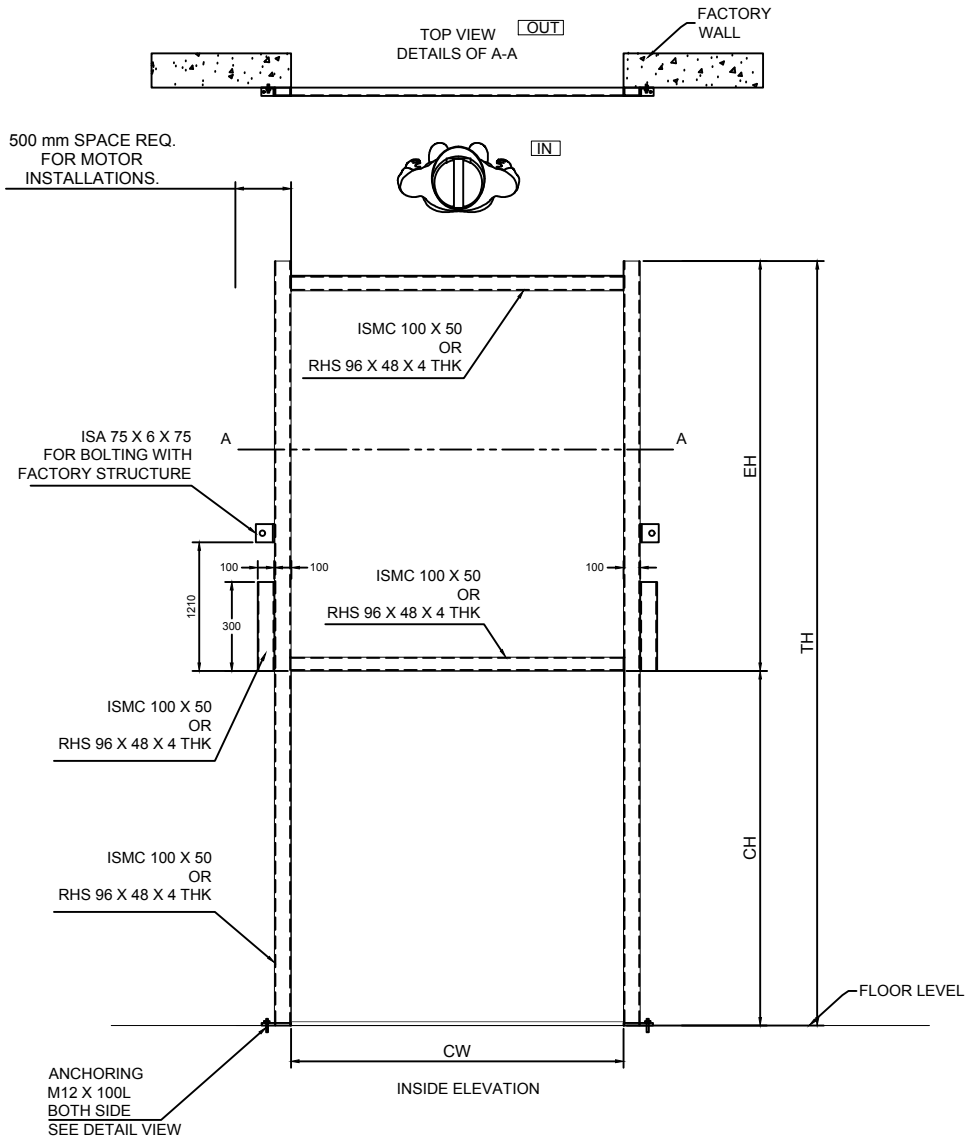


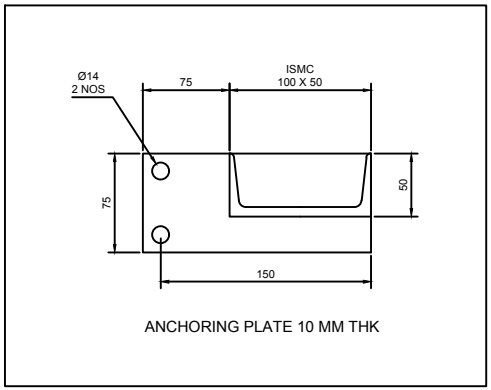

ANCHORING PLATE 10 MM THK

SR NO	CLEAR WIDTH	CLEAR HEIGHT	QTY	TH	EH
01	2400mm	3000mm	1	6350	3350

This drawing & design is the property of NIHVA TECHNOLOGIES. Not to be sold or copied to any other concern.

TITLE: SECTIONAL DOOR (VL) STRUCTURE

NIHVA TECHNOLOGIES PVT. LTD.
NIHVA TECHNOLOGIES PVT. LTD. PUNE
Tel : 020 66304033
Email:- info@nihva.com
Website:- www.nihva.com

	NAME	SIGN	DATE
DRAWN	P.A		27.05.20
CHECK	G.J		27.05.20
APPROVAL			

CLIENT - HIRANANDANI
PROJECT - KSH
SITE -

If any queries contact : design@nihva.com
DWG. NO. : NIHVA/20-21/0012 REV: 0
ALL DIMENSION ARE IN mm
SCALE: NTS WT: SHEET: 01 OF 01

TOLERANCE: 10mm