

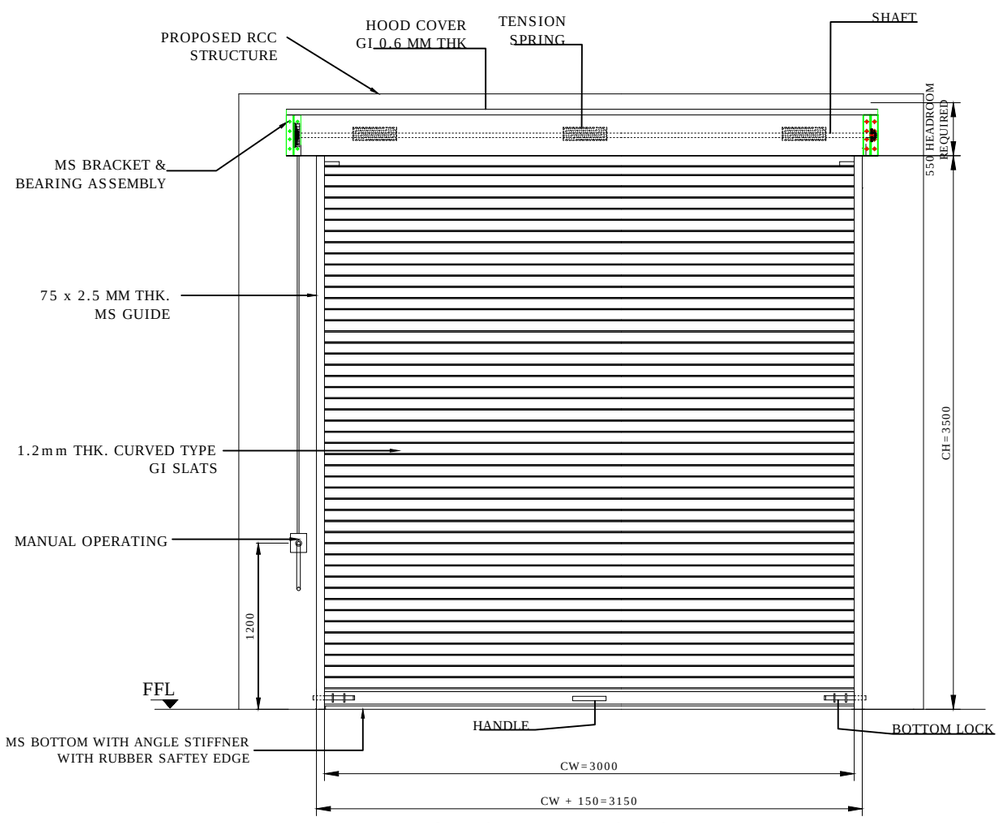



OUTSIDE ELEVATION

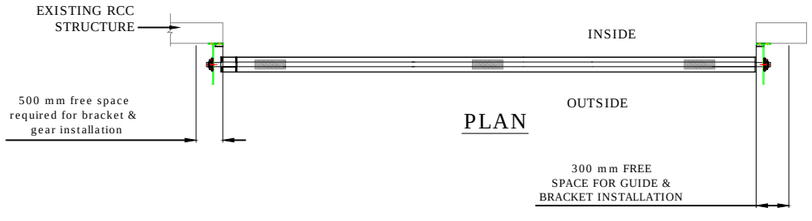


PLAN

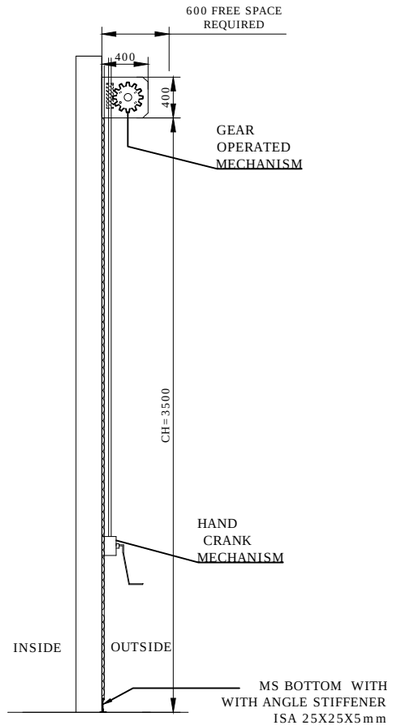

SIDE VIEW

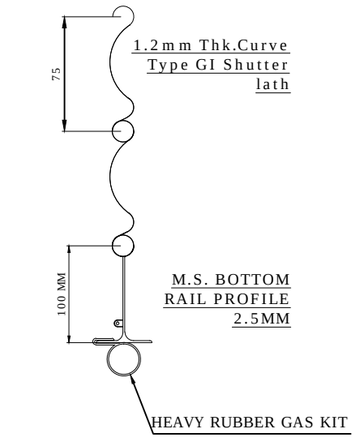

M.S. BOTTOM RAIL PROFILE 2.5MM

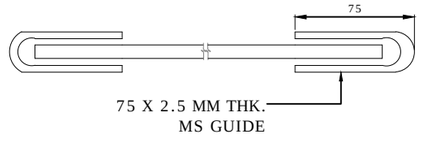

RAL CODE	RAL COLOR	APPROVAL
RAL 7040	WINDOW GREY	APPROVED

SR NO	(CW) CLEAR WIDTH	(CH) CLEAR HEIGHT	QUANTITY
1	3000	3500	05 NO

NOTE-
1. ALL DIMENSIONS ARE IN MM.
2. SURFACE FINISH: POWDER COATING OF APPROVED RAL CODE.
3. MOUNTING ON OUTSIDE CONCRETE STRUCTURE.
4. MOUNTING OF LEVER WILL BE ON LEFT SIDE.

REV 01 (05-03-2022)
1. CHANGED THE QUANTITY OF SHUTTERS TO 5 NOS.

TOLERANCE - ±10mm

This drawing & design is the property of NIHVA TECHNOLOGIES. Not to be sold or copied to any other concern.

TITLE
GEAR OPERATED ROLLING SHUTTER

	NAME	SIGN	DATE
DRAWN	G.I.P		23.02.2022
CHECK	A.K.		23.02.2022
APPRD.	V.T.		23.02.2022

NIHVA TECHNOLOGIES PVT. LTD.
Website:- www.nihva.com
NIHVA TECHNOLOGIES PVT. LTD. PUNE
Tel : 020 66304033
Email:- info@nihva.com

CLIENT -
PROJECT -GEAR OPERATED ROLLING SHUTTER
SITE LOCATION -
If any queries contact : design@nihva.com
DWG. NO. : NIHVA/21-22/VDR/035
REV- R1
ALL DIMENSION ARE IN mm
SCALE: NTS
WT:
SHEET: 01 OF 01