

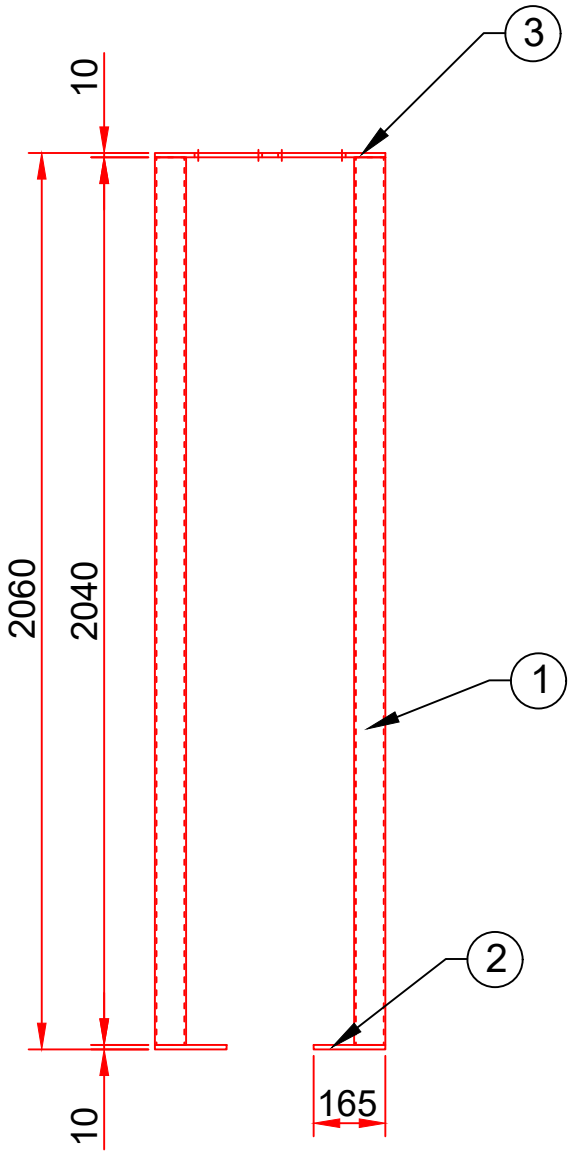


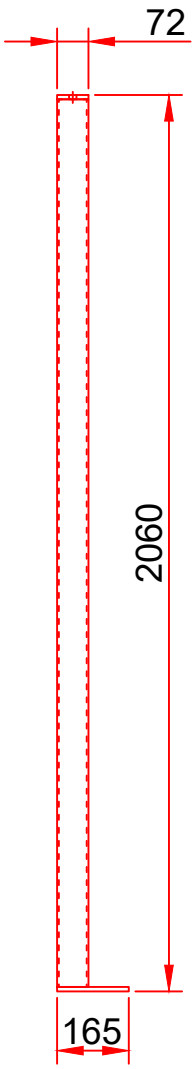

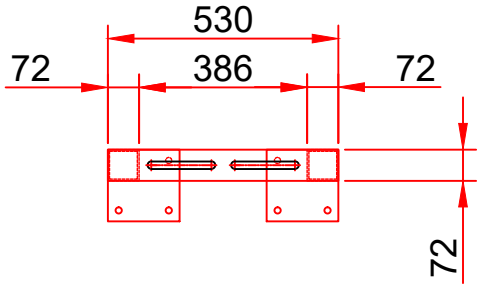

BOM FOR POST			
SL NO.	DESCRIPTION	SPECIFICATION	QTY
1	MS SQ. TUBE	72X72X3.2X2040L	2NOS
2	POST SUPPORT PLATE	165X165X10THK	2NOS
3	ROLLER SUPPORT PLATE	530X72X10THK	1NO

This drawing & design is the property of NIHVA TECHNOLOGIES. Not to be sold or copied to any other concern.

TITLE:- END POST

NIHVA TECHNOLOGIES PVT. LTD. PUNE
Tel : 020 66304033
Email:- info@nihva.com
Website:- www.nihva.com

	NAME	DATE	SIGN
DRAWN	NIRMALA	10/06/2023	
CHECK	M.S	10/06/2023	
APPRD.	A.K	10/06/2023	

CLIENT - EIRICH

LOCATION - PUNE

PRODUCT -TELESCOPIC SLIDING GATE | QTY:-1 NO

If any queries contact : design@nihva.com | DWG NO:-NIHVA/23-24/MFG/ | REV- 0

ALL DIMENSION ARE IN mm | SCALE: NTS | SCALE:-- 1:1 | SHEET: 01 OF 01

Rev No.	Revision	Date	Revised By