


GA DRAWING

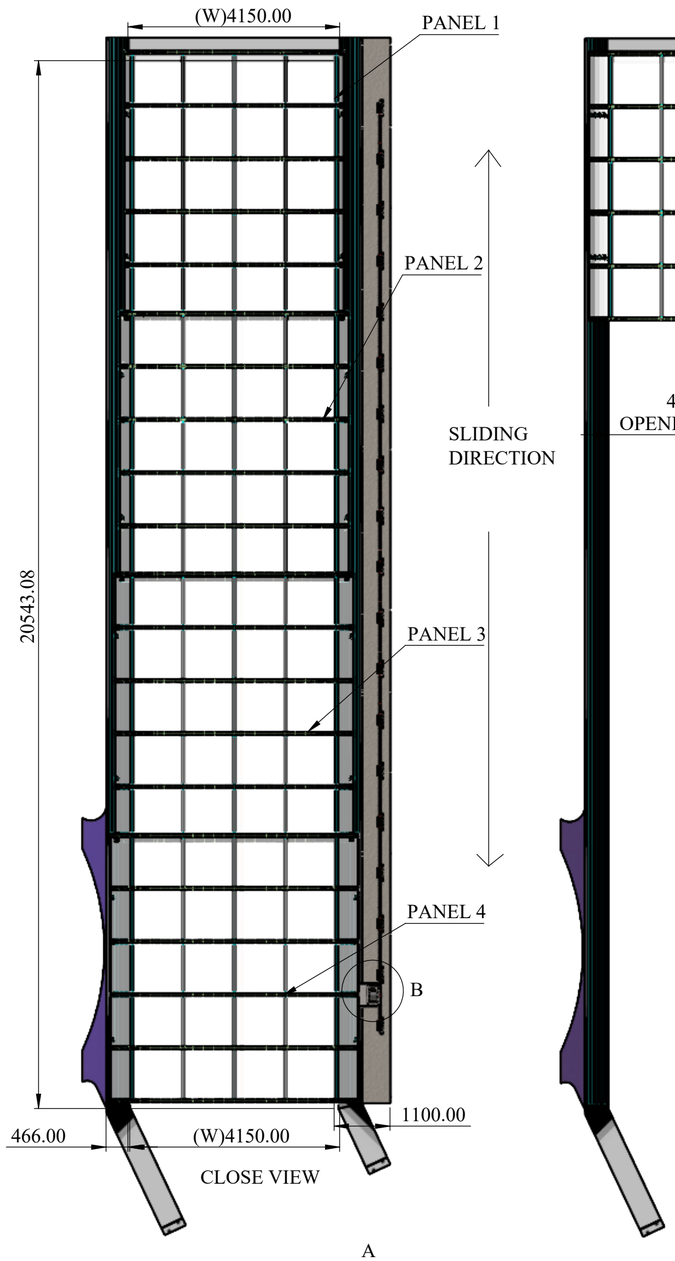


CLOSE VIEW

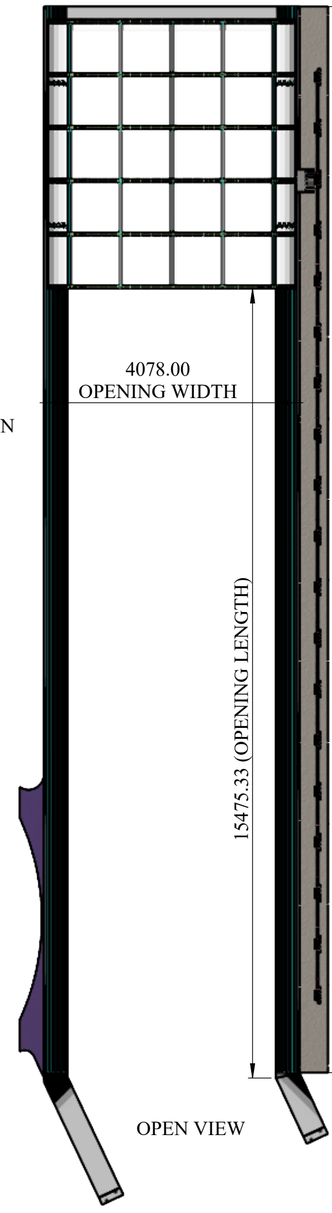



OPEN VIEW

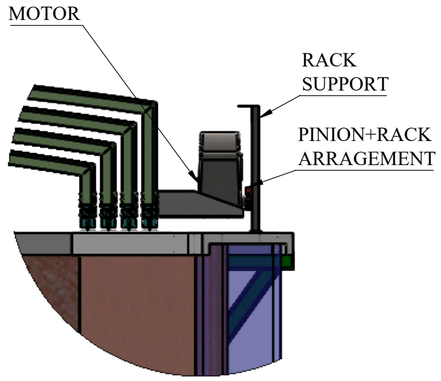



DETAIL A
SCALE 1 : 20


TRACK+MOTOR ARRAGEMENT

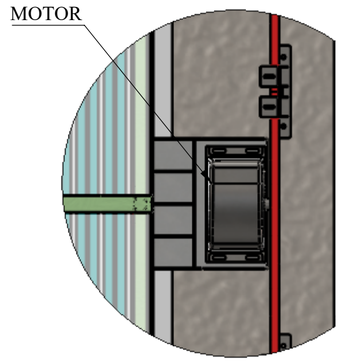


DETAIL B
SCALE 1 : 15

MOTOR ARRAGEMENT

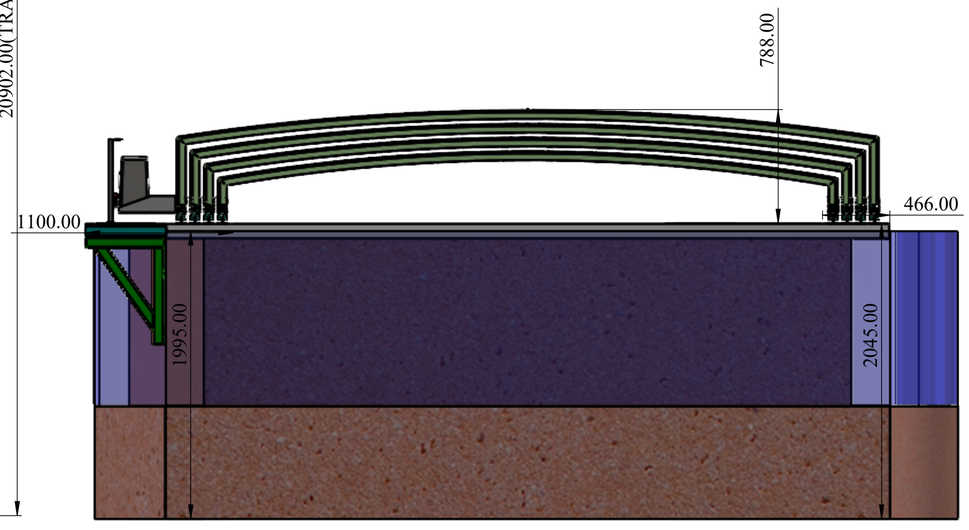

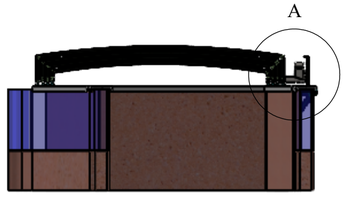
| REV DESCRIPTION | DATE | REV NO |
|---|---|---|
| | 17-07-2026 | REV 00 |
| 1. | | |

NOTE :
GA DRAWING
THIS DRAWING IS FOR CLIENT APPROVAL.

SPECIAL INSTRUCTION'S :

This drawing & design is the property of NIHVA TECHONOLOGIES PVT. LTD. Not to be sold or copied to any other concern

TITLE - RETRACTABLE ROOF


DWG NO - NTPL


NIHVA TECHNOLOGIES PVT.LTD.PUNE
Website - www.nihva.com

| | NAME | SIGNATURE | DATE |
|---|---|---|---|
| DRAWN | V.W. | | 17-07-2026 |
| CHK'D | S.P. | | 19-07-2026 |
| APPV'D | V.T. | | 19-07-2026 |


PRODUCT - RETRACTABLE ROOF
CLIENT NAME - YASHWANT
SITE LOCATION - CHENNAI
MATRIAL -
QTY - 1
If any queries contact - info@nihva.com
PROJECTION METHOD:
SCALE :
ALL DIMENSION ARE IN mm
A2
SHEET 1 OF 2

CIVIL DRAWING

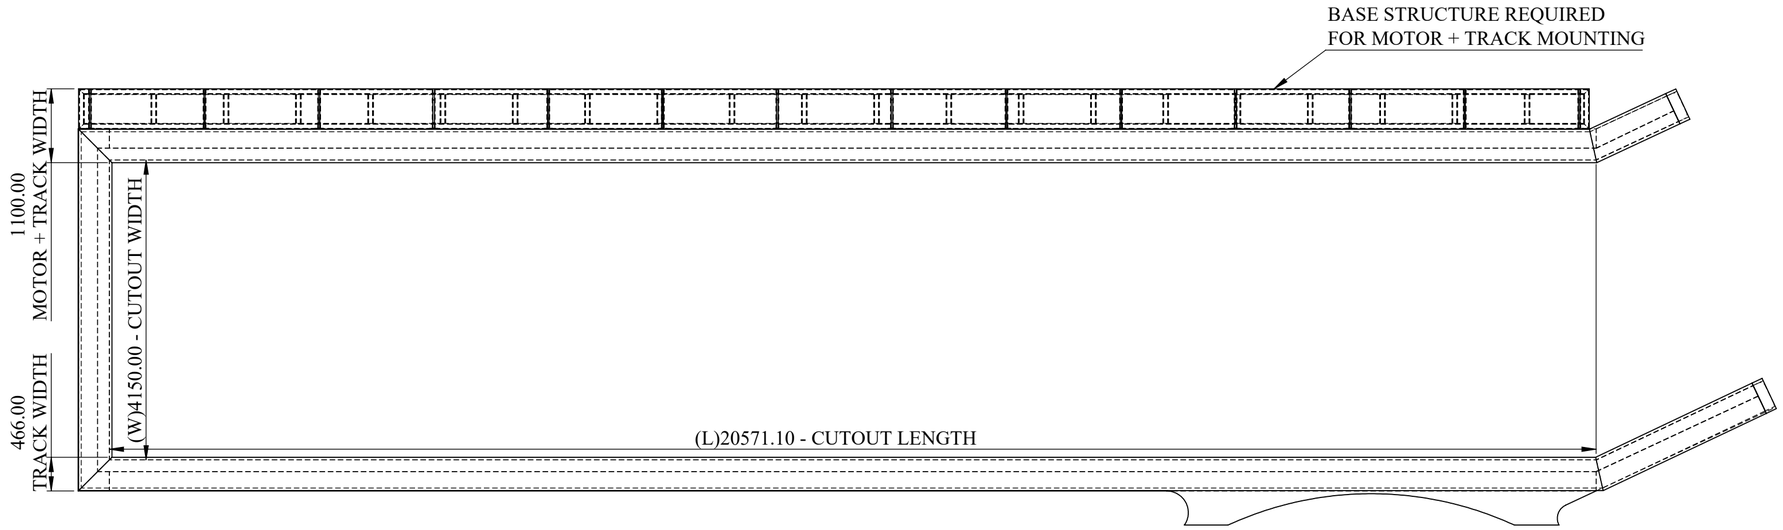

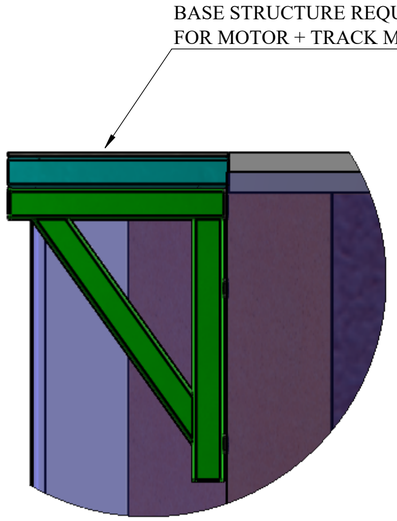
DETAIL C
SCALE 1 : 11

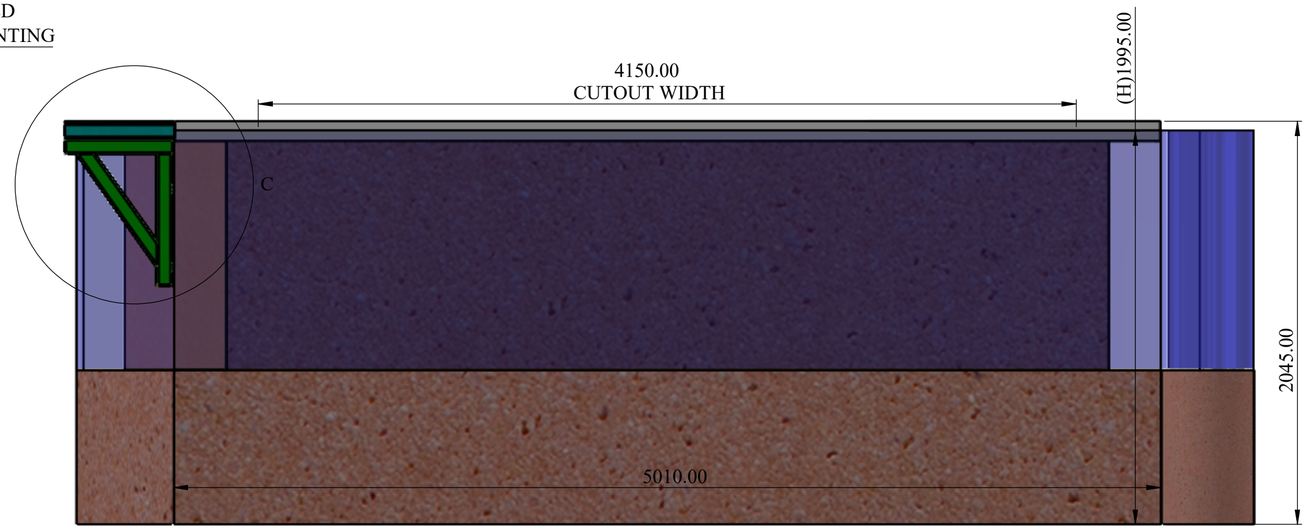


| REV DESCRIPTION | DATE | REV NO |
|---|---|---|
| | 17-07-2026 | REV 00 |
| 1. | | |

NOTE :
CIVIL DRAWING
BASE STRUCTURE IN CLIENT SCOPE.

SPECIAL INSTRUCTION'S :

This drawing & design is the property of NIHVA TECHONOLOGIES PVT. LTD. Not to be sold or copied to any other concern

TITLE - RETRACTABLE ROOF
DWG NO - NTPL

NIHVA TECHNOLOGIES PVT.LTD.PUNE
Website - www.nihva.com

| | NAME | SIGNATURE | DATE |
|---|---|---|---|
| DRAWN | V.W. | | 17-07-2026 |
| CHK'D | S.P. | | 20-07-2026 |
| APPV'D | V.T. | | 20-07-2026 |

PRODUCT - RETRACTABLE ROOF
CLIENT NAME - YASHWANT
SITE LOCATION - CHENNAI
MATRIAL -
QTY - 1
If any queries contact - info@nihva.com
ALL DIMENSION ARE IN mm
A2
PROJECTION METHOD:
SCALE :
SHEET 2 OF 2