


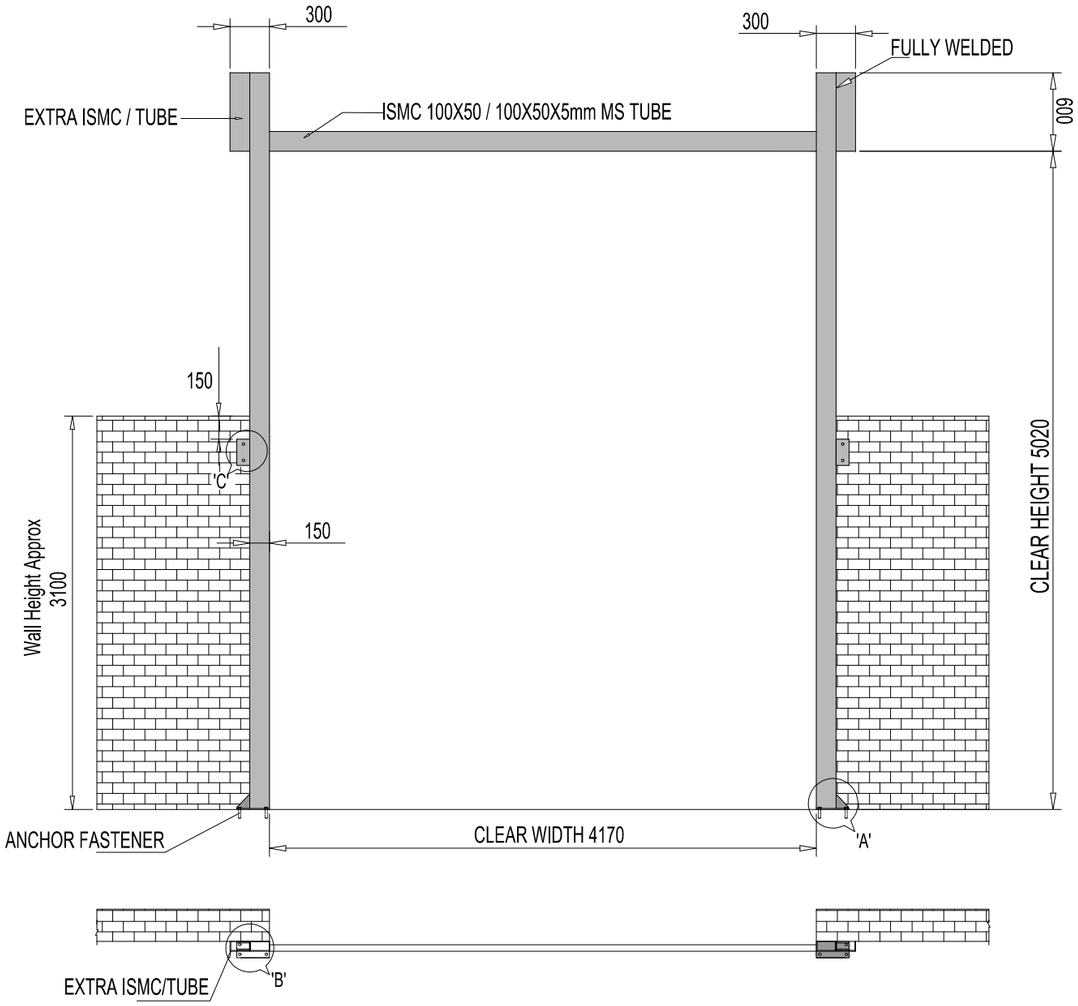


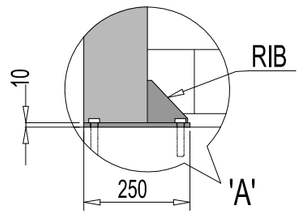

DETAIL VIEW 'A'

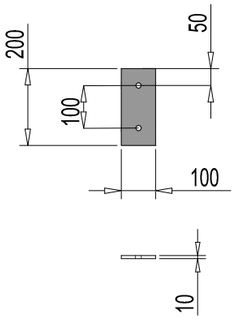

DETAIL VIEW 'C'

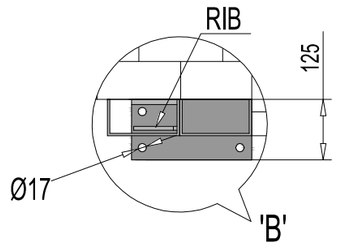

DETAIL VIEW 'B'

SURAJ		R01	04/08/2018.	1.STRUCTURE DETAILS ADD
DRAWN NAME	SIGN	REVISION	DATE	REVISION DETAILS

CLEAR WIDTH	CLEAR HEIGHT	QUANTITY
4170	5020	02

NOTE :

1. MATERIAL FOR ALL STRUCTURE = M.S

TOLERANCE - ±10mm & 15 kgs

This drawing & design is the property of NIHVA TECHNOLOGIES. Not to be sold or copied to any other concern.

TITLE

STRUCTURE FOR GEAR OPERATED ROLLING SHUTTER

NIHVA TECHNOLOGIES PVT. LTD.

NIHVA TECHNOLOGIES PVT. LTD. PUNE
Tel : 020 66304033
Email:- info@nihva.com
Website:- www.nihva.com

	NAME	SIGN	DATE
DRAWN	SURAJ		04-08-2018
CHECK	PRADEEP		04-08-2018
APPRD.	R.D		04-08-2018

CLIENT -

PROJECT-

SITE LOCATION -

If any queries contact : design@nihva.com

DWG. NO. : NIHVA/17-18/VDR/068

REV- 01

ALL DIMENSION ARE IN mm

SCALE: NTS

WT:

SHEET: 01 OF 01