

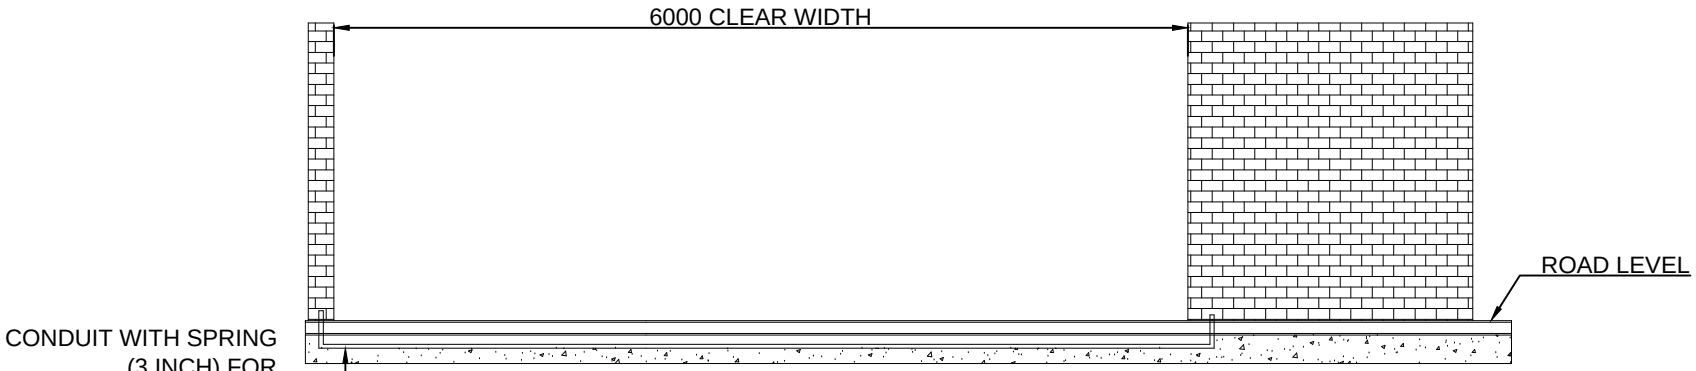


INSIDE ELEVATION

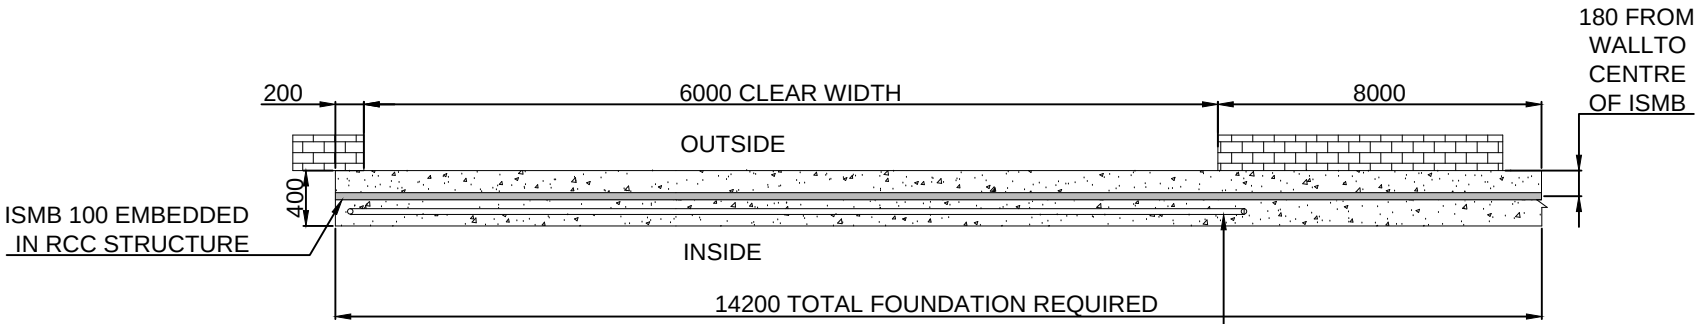

PLAN

CONDUIT WITH SPRING
(3 INCH) FOR
PHOTOCELL WIRE

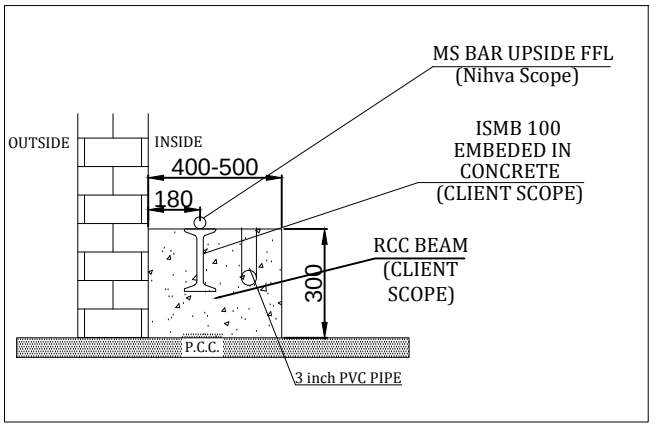

6.0m SLIDING GATE FOUNDATION

This drawing & design is the property of NIHVA TECHNOLOGIES. Not to be sold or copied to any other concern.

TITLE: FOUNDATION FOR 6M SLIDING GATE

	SIGN	DATE
DRAWN	OMKAR	31/08/17
CHECK	SHEKHAR	31/08/17
REV.		
APPROVAL	SHEKHAR	31/08/17

If any queries contact : projects@nihva.com

ALL DIMENSION ARE IN mm

NIHVA TECHNOLOGIES PVT. LTD.
NIHVA TECHNOLOGIES PVT. LTD. PUNE
Tel : 020 66304033
Email:- info@nihva.com
Website:- www.nihva.com

CLIENT - SHILCHAR TECHNOLOGIES LTD.

PROJECT -

SITE - VADODARA

DWG. NO. : NIHVA/17-18/0190

SCALE: NTS | WT: | SHEET: 01 OF 01