

Abbrevation's:
WOW-Wall Opening Width
WOH-Wall Opening Height
FFL-Finished Floor Level

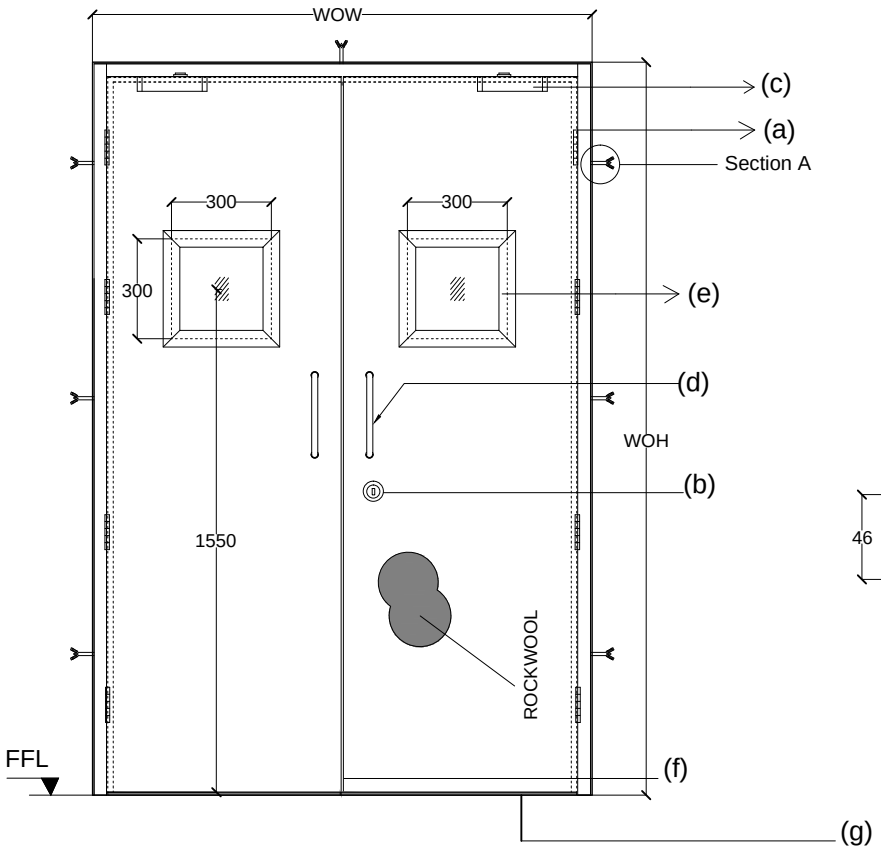

ELEVATION

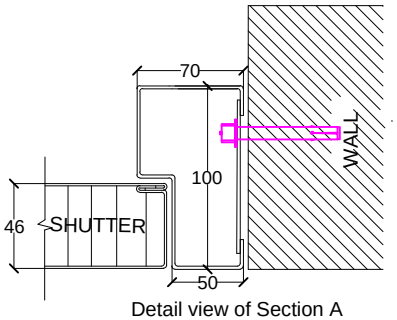

Detail view of Section A

ASSESORIES DETALES

(a) HINGES: SS Hinges 100x75x3mm

(b) LOCK : Mortise Dead lock with double Cylinder(Both side key) with Escutcheon

(c) DOOR CLOSER - TS68

(d) HANDLE : D Handle(300X22)Pair

(e) VISION PANEL- 5mm THK. GLASS OF SIZE 300X300mm.

(f) CONCEALED FLUSH BOLT

(g) RUBBER SEAL

Shutter thickness : 46 mm
Frame Sheet thick : 1.2mm
Shutter sheet thick :0.8mm
Fixing : On Soliid Brick plasterd wall with Anchors

NOTE:- *All Dimensions are in mm.
*Tolerance:-All Linear Dimensions ±3mm,Others ±0.5mm.
*The Drawing Is For Location of Hardware only. Drawing Does Not Represent The Hardware For More Clarity, Please Go Through Hardware Broucher.



PLAN

COLOR:- 1.PURE WHITE (RAL9010)

DOOR SIZE / TYPE

WOW	WOH	TYPE 5	TYPE 6	TYPE 7	TYPE 8	LOCATION	QUANTITY
1500	2200					Mold Washing Room	01
1500	2200					Mold Washing Room	01
1500	2200					Intec Area	01
1500	2200					Intec Area	01

This drawing & designing is the property of NIHVA TECHNOLOGIES. Not be sold or copy to any other concern.

STEEL DOOR
(DOUBLE LEAF)

	NAME	DATE	SIGN.
DRAWN	SURAJ	28/10/17	
CHECK	SAGAR	28/10/17	
APPRD.	SHEKHAR	28/10/17	
MFG			

ALL DIMENSION ARE IN mm

NIHVA TECHNOLOGIES PVT. LTD.
NIHVA TECHNOLOGY PVT. LTD. PUNE
Tel : 020 66304033
Email:- info@nihva.com
Website:-www.nihva.com

CLIENT - FERRERO INDIA PVT. LTD
PROJECT -
SITE - BARAMATI.
DWG. NO. - NIHVA/17-18/0255 | REV. - 0
SCALE:NTS | WT: | SHEET: 01 OF 01
If any queries contact : projects@nihva.com

Note:
1.Client has to select door handling type from attached door handling sheet.