
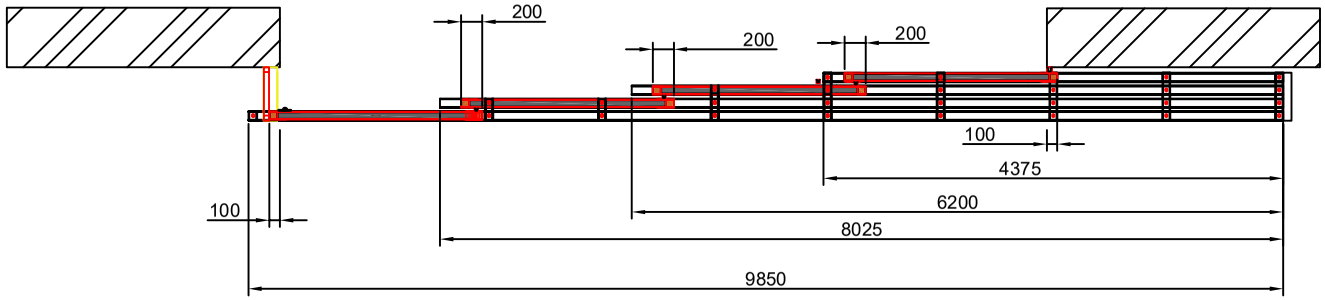


Client scope

*Civil foundation need to be done for tracks approx.500mm
*Bollards need to shift forward
*Roof need to be shift at top approx.300mm

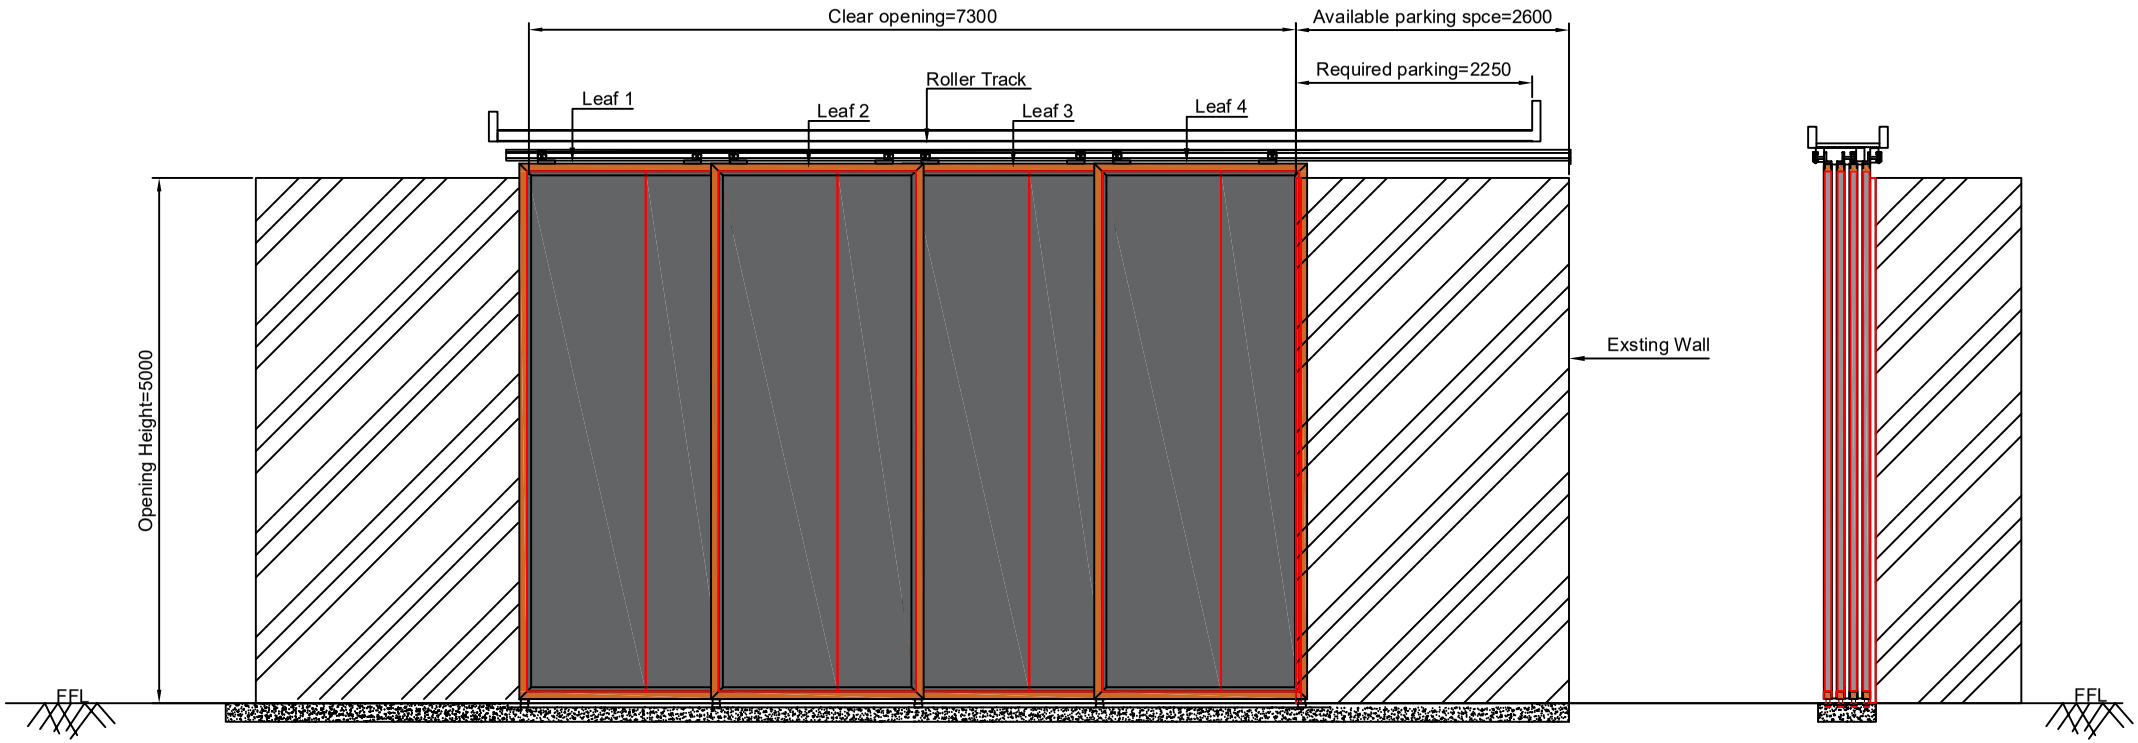

Note:--
1.All dimension are in MM
2.All Civil work will be in client scope

This drawing & design is the property of NIHVA TECHNOLOGIES. Not to be sold or copied to any other concern.

TITLE:- 4 LEAF RIGHT SIDE CRM DOOR 01

	NAME	DATE	SIGN
DRAWN	SUJATA	20/04/2022	
CHECK	M.SUTAR	20/04/2022	
APPRD.	V.TARAK	20/04/2022	

If any queries contact : design@nihva.com

ALL DIMENSION ARE IN mm

NIHVA TECHNOLOGIES PVT. LTD.
NIHVA TECHNOLOGIES PVT. LTD. PUNE
Tel : 020 66304033
Email:- info@nihva.com
Website:- www.nihva.com

CLIENT - LESTECH
LOCATION - POSCO MANGAON
PRODUCT - SLIDING DOOR
DWG NO:-NIHVA/22-23/CLT/0014 | REV- 0
SCALE: NTS | SCALE:-- 1:1 | SHEET: 01 OF 01

Rev No.	Revision	Date	Revised By