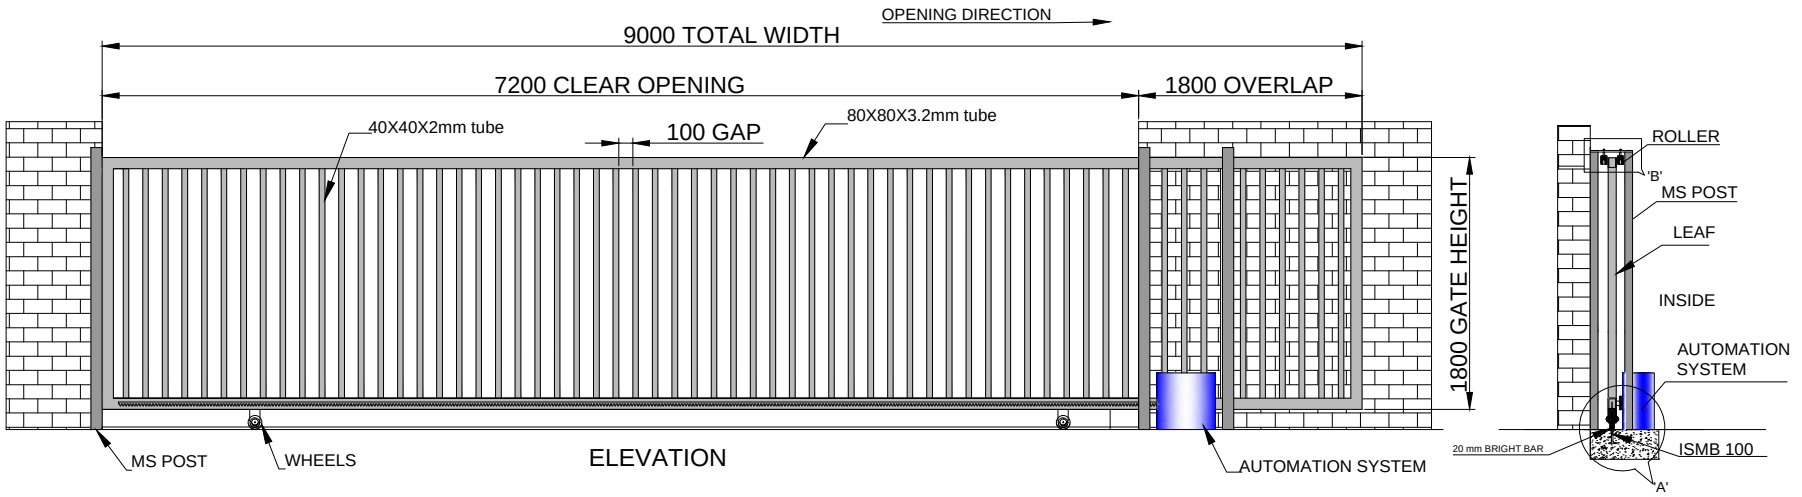
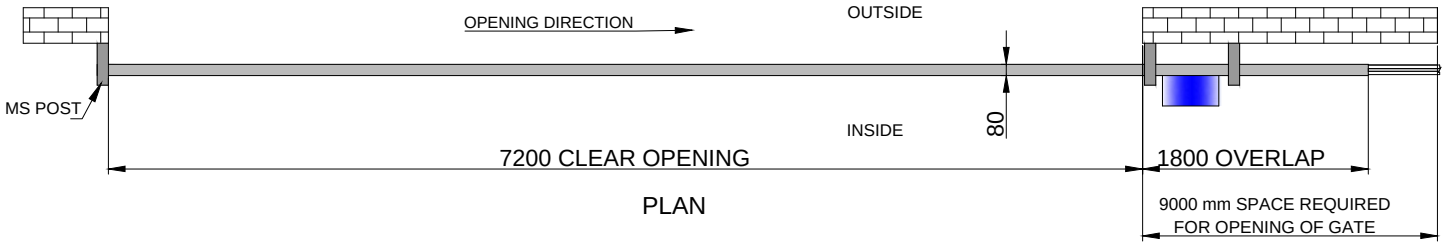
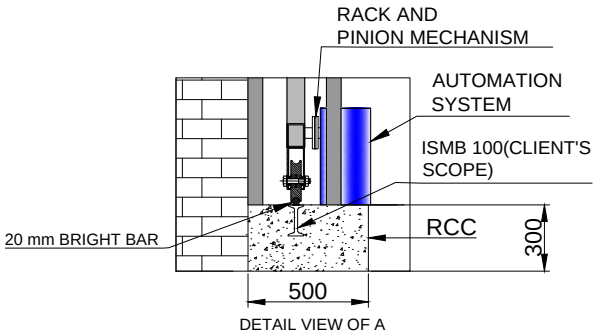
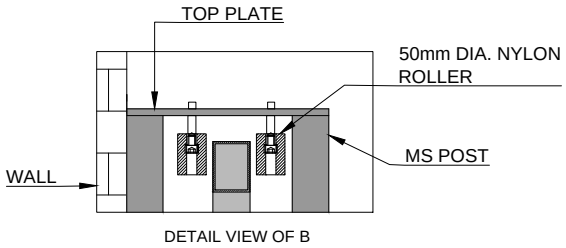



| SR NO | TUBE SPECIFICATION | |
|---|---|---|
| 1 | 80X80X3.2mm | OUTER FRAME |
| 2 | 40X40X2mm | INNER PATTERN |
| 3 | 80X80X3.2mm | FOR MS POST |

TOTAL NO OF POST ARE 4.

NOTE-
1. ALL REQUIRED CIVIL WORK WILL BE IN CLIENTS SCOPE.
2. ONE COAT OF RED OXIDE & TWO COAT OF APPROVED RAL SHADE WILL BE GIVEN TO THE GATE.
3.GATE LEAF WILL BE IN TWO PARTS FOR TRANSPORTATION & WILL BE WELD TOGETHER ON SITE.

TOLERANCE- ±10mm

| CLEAR WIDTH | CLEAR HEIGHT | QUANTITY | LOCATION |
|---|---|---|---|
| 7200mm | 1800mm | 1 NOS | MAIN ENTRANCE TO COMMERCIAL & BUSINESS CENTER. |

This drawing & designing is the property of NIHVA TECHNOLOGIES. Not to be sold or copied to any other concern.

TITLE
AUTOMATIC SINGLE LEAF SLIDING GATE

| | SIGN | DATE |
|---|---|---|
| DRAWN | SURAJ | 20/05/17 |
| CHECK | SAGAR P. | 20/05/17 |
| REV. | | |
| APPROVAL | S.S | 20/05/17 |

If any queries contact : projects@nihva.com

ALL DIMENSION ARE IN mm

NIHVA TECHNOLOGIES PVT. LTD. PUNE
Tel : 020 66304033
Email:- info@nihva.com
Website:- www.nihva.com

CLIENT -

PROJECT -

SITE LOCATION -

DWG. NO. : NIHVA/17-18/VDR/0050

SCALE: NTS | WT: | SHEET: 01 OF 01