


DWG.NO: SALT_1729_STR_01_R0

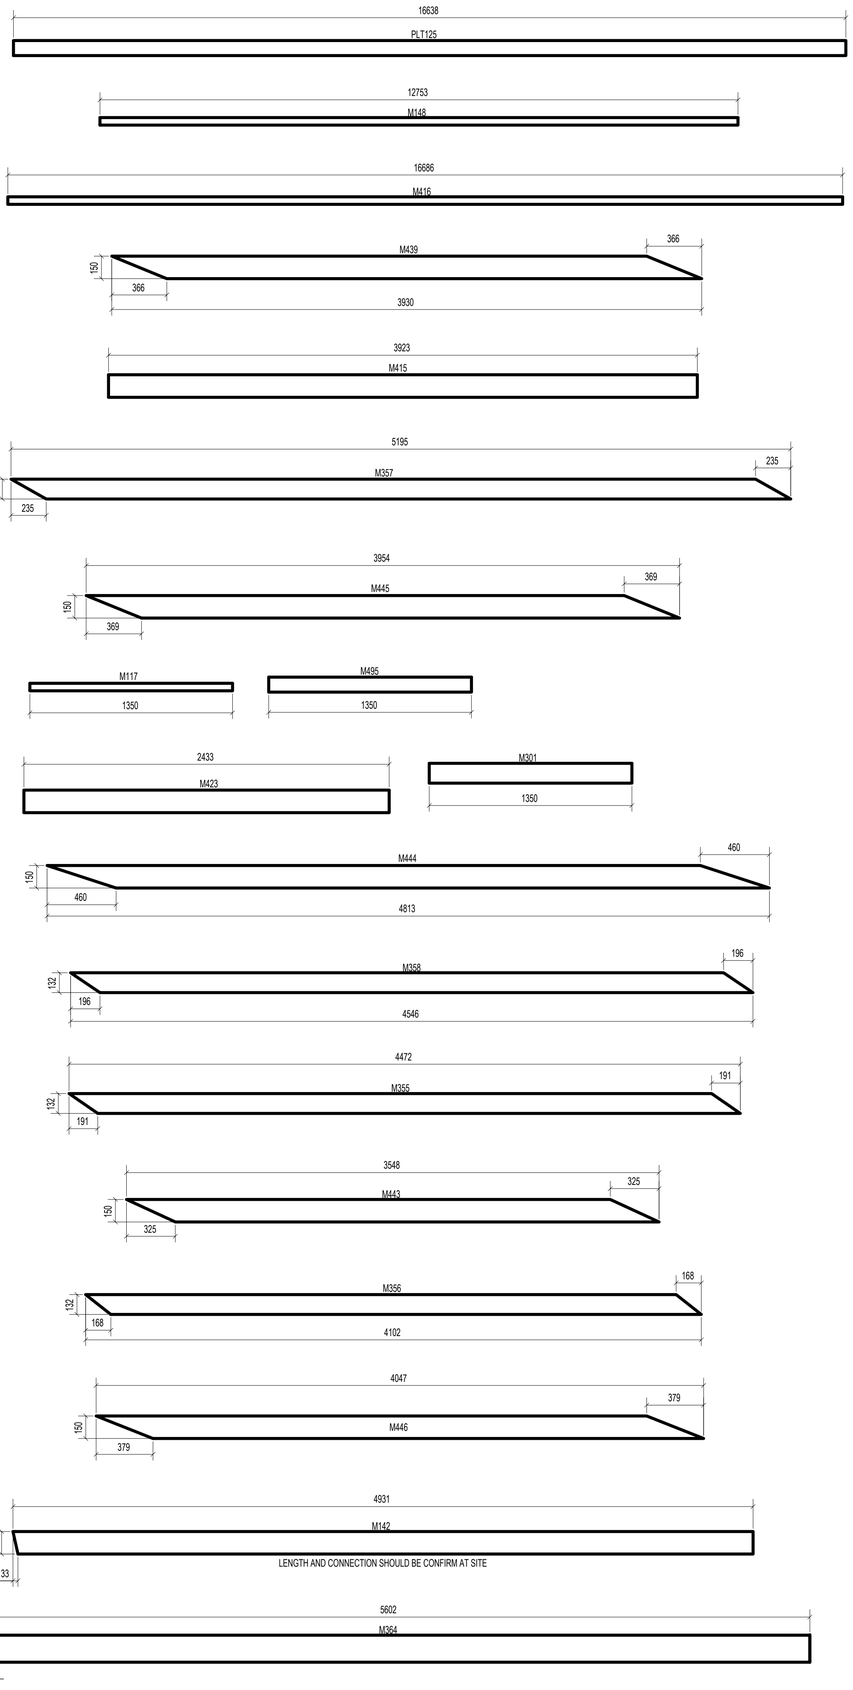


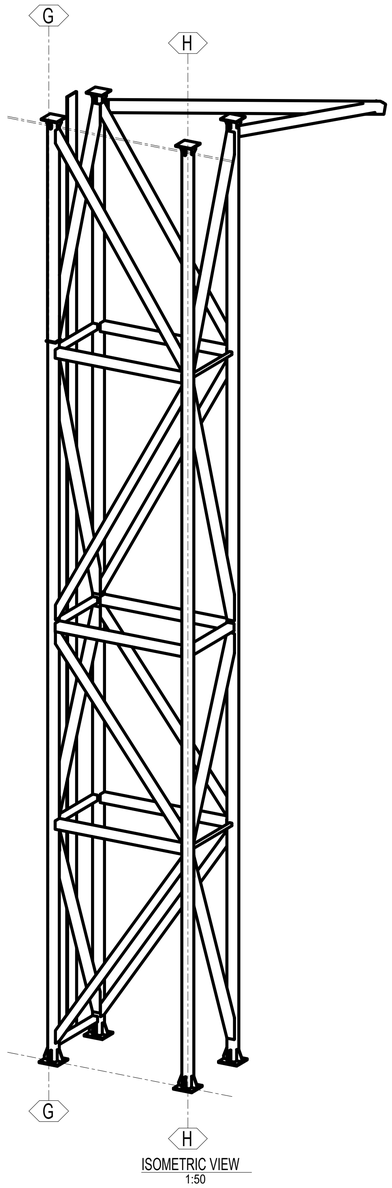



ISOMETRIC VIEW
1:50


CUTTING DETAIL BETWEEN GRID G & GRID H						
PartPos	Profile	No.	Material	Length	Net Weight(kg	Gross Weight(kg
M117	SHS50*3.6	2	IS2062	1350	7.08	14.16
M142	SHS150*8	1	IS2062	4931	175.32	175.32
M148	SHS150*8	1	IS2062	12753	454.9	454.9
M301	SHS132.0X132.0X4.8	1	IS2062	1350	25.25	25.25
M355	SHS132.0X132.0X4.8	2	IS2062	4472	79.99	159.98
M356	SHS132.0X132.0X4.8	2	IS2062	4102	73.51	147.02
M357	SHS132.0X132.0X4.8	2	IS2062	5195	92.69	185.38
M358	SHS132.0X132.0X4.8	2	IS2062	4546	81.29	162.58
M364	SHS180.0X180.0X8.0	1	IS2062	5602	234.97	234.97
M415	SHS150.0X150.0X5.0	1	IS2062	3923	87.34	87.34
M416	SHS150.0X150.0X5.0	3	IS2062	16686	371.47	1114.41
M423	SHS150.0X150.0X5.0	6	IS2062	2433	54.17	325.02
M439	SHS150.0X150.0X5.0	2	IS2062	3930	79.16	158.32
M443	SHS150.0X150.0X5.0	2	IS2062	3548	71.59	143.18
M444	SHS150.0X150.0X5.0	2	IS2062	4813	96.67	193.34
M445	SHS150.0X150.0X5.0	1	IS2062	3954	79.62	79.62
M446	SHS150.0X150.0X5.0	1	IS2062	4047	81.48	81.48
M495	SHS100.0X100.0X6.0	4	IS2062	1350	22.92	91.68
PLT11	PL16*300	4	IS2062	300	11.3	45.2
PLT17	PL20*350	4	IS2062	350	19.23	76.92
PLT25	PL10*180	1	IS2062	180	2.54	2.54
PLT118	PL10*223	1	IS2062	250	4.38	4.38
PLT121	PL10*100	16	IS2062	200	1.21	19.36
PLT122	PL10*75	16	IS2062	150	0.66	10.56
PLT125	PLT16*300	1	IS2062	16638	626.92	626.92
	TOTAL					**4619.83**

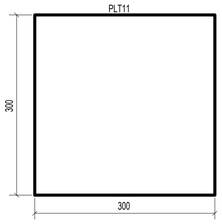


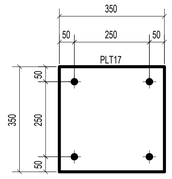

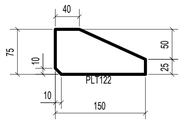

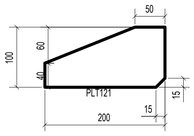

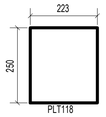

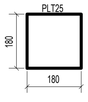

NOTES :–

1. ALL DIMENSIONS ARE IN MM & LEVEL ARE IN METER.
2. ALL STRUCTURAL STEEL AS PER IS:2062.
3. PROVIDE WELDING AS PER IS:816.
4. PROVIDE MIN. 6MM WELD WITH MIN. WELD LENGTH OF 150MM.
5. USE ELECTRODS AS PER IS:814 (PT.–I).
6. FILLET/ BUTT WELD SHALL BE OF 6MM SIZE AND SHALL BE CONTINUOUS.
7. FABRICATION AND ERECTION SHALL BE AS PER IS:800 AND IS:803.
8. WELD SHALL BE GROUND SMOOTH.
9. ALL GUSSET PLATES SHALL BE MIN. 10 THK.
10. ALL M.S. BLACK BOLTS AND NUTS SHALL CONFORM TO IS:1363(PT. 1 TO 3).
11. STRUCTURE SHALL BE APPLIED WITH ONE COAT OF RED OXIDE ZINC CROMATE PRIMER AFTER FABRICATION FOLLOWED ONE MORE COAT BEFORE ERECTION. FINALLY APPLY 2 COATS OF SYNTHETIC ENAMAL OF APPROVED QUALITY.

REV.NO.	DESCRIPTION.	REV.DATE	DRAWN.	CHKD.	APPD.
0	DRAWING FOR APPROVAL	27.12.22	AAK	HAB	HAB

DWG.TITLE :- CUTTING DETAIL BETWEEN GRID G & H
DRAWING FOR DOOR FRAME

PROJECT: MEGADOOR INSTALLATION AT HYDRABAD AIRPORT

CLIENT: GMR

SALT Design Services
NIHVA TECHNOLOGIES PVT. LTD.

SALT DESIGN SERVICES
NIHVA TECHNOLOGIES PVT. LTD. PUNE
Tel : 020 66304033
Email:- info@nihva.com
Website:- www.nihva.com

DRAWN :AAK	CHECKED : HAB	SCALE: 1:100
APPROVED : HAB	JOB CODE. : 1729	DATE: 27.12.2022

DWG.NO: SALT_1729_STR_01_R0 (SH-1OF1) REV. - R0 SIZE. - A1

A1 [841 x 594]