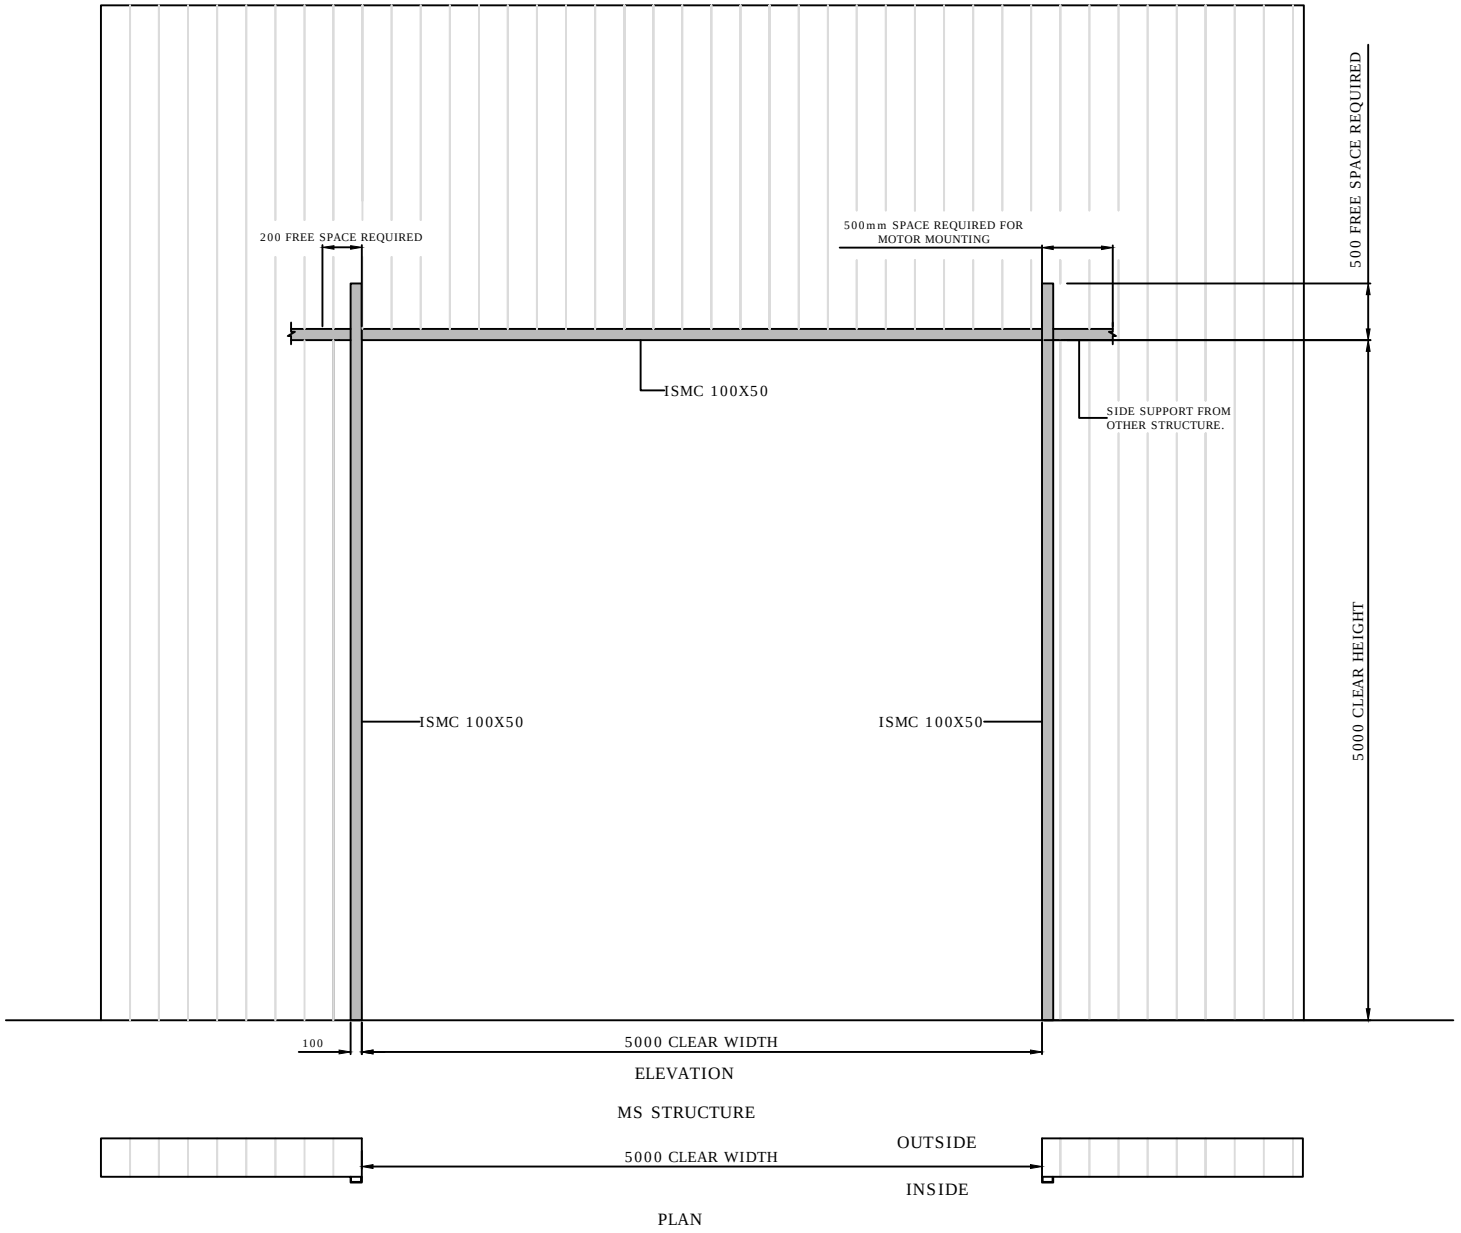

DIMENSION :

CLEAR WIDTH	CLEAR HEIGHT	QUANTITY
5000 mm	5000 mm	1 NOS.

MATERIAL :

THICKNESS :

NOTE: REQUIRED STRUCTURE FOR HIGH SPEED DOOR IS IN NIHVA SCOPE.

NIHVA TECHNOLOGIES PVT. LTD.

NIHVA TECHNOLOGY PVT. LTD. PUNE
Email:- info@nihva.com
Website:- www.nihva.com

TITLE:

STRUCTURE & CUTOUT DETAIL FOR HIGH SPEED DOOR

CLIENT'S APPROVAL :

CLIENT - GE INDIA INDUSTRIAL PVT. LTD

PROJECT -

SITE LOCATION - CHAKAN, PHASE-3

DWG. NO. : NIHVA/16-17/106

SCALE: NTS	WT:	SHEET:1 OF 1

DRAWN BY: OMKAR	DATE: 29-11-2016
CHECK : SAGAR P.	DATE: 29-11-2016

If any queries contact : projects@nihva.com

NOTE: ALL DIMENSION ARE IN mm

THIS DRAWING & DESIGNING IS THE PROPERTY OF NIHVA TECHNOLOGIES. NOT BE SOLD OR COPY TO ANY OTHER CONCERN.