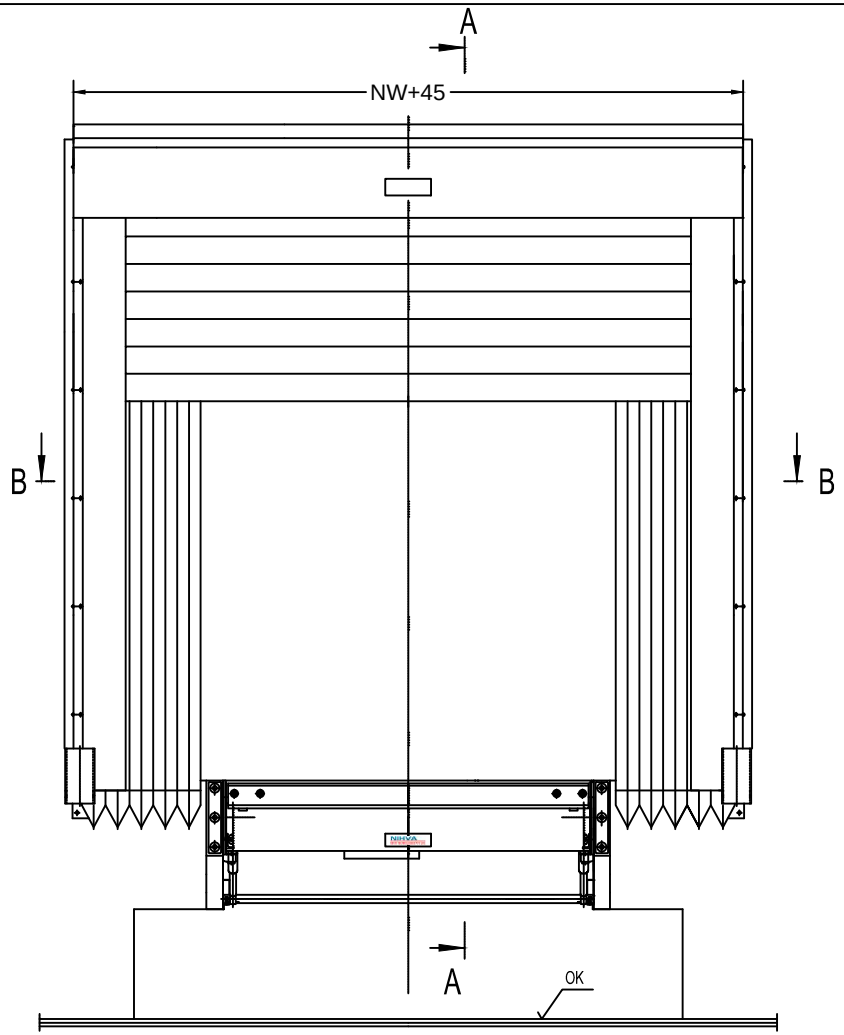
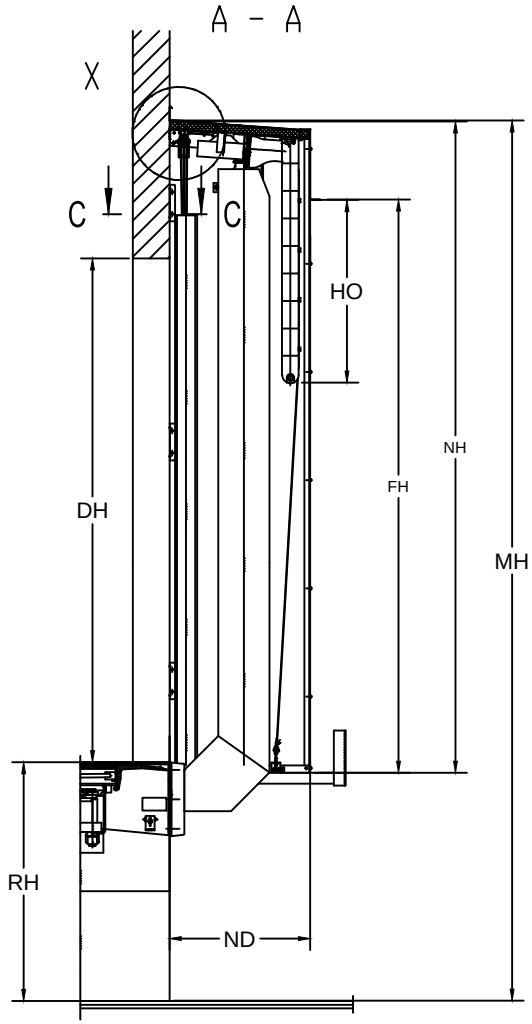
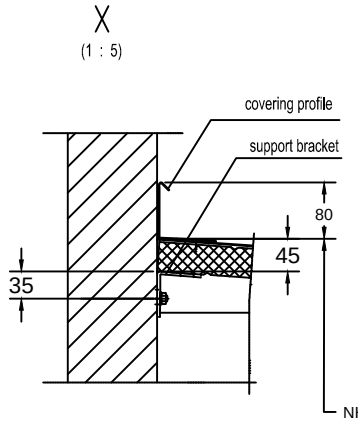
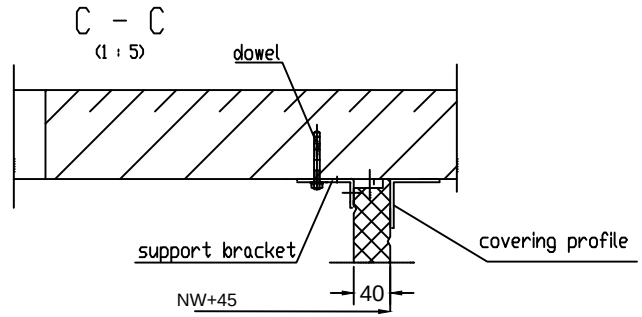
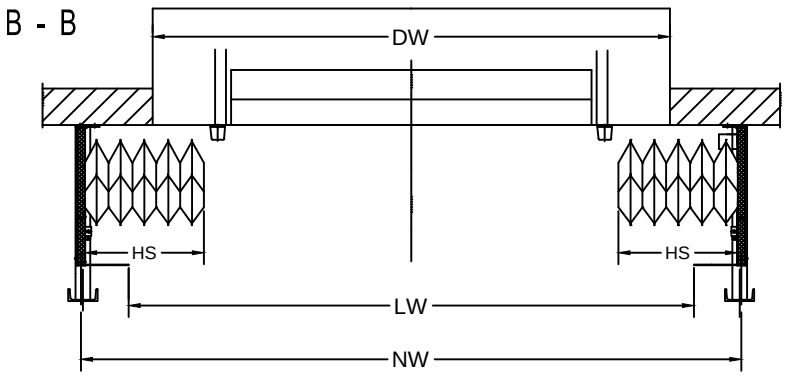



| Abb. | Dimension | Value(mm) |
|---|---|---|
| NW | Nominal width | 3600 |
| NH | Nominal height | 4055 |
| HS | Side bag extension | 650 |
| FH | Free height above level | 4055 |
| HO | Top bag extension | 1000 |
| ND | Nominal depth | 770 |
| MH | Installation height | VH+500 |
| LW | Clear width(max) | |

This drawing & designing is the property of NIHVA TECHNOLOGIES. Not to be sold or copied to any other concern.

TITLE

**DOCK SHELTER**

NIHVA TECHNOLOGIES PVT. LTD.

NIHVA TECHNOLOGIES PVT. LTD. PUNE
Tel : 020 66304033
Email:- info@nihva.com
Website:- www.nihva.com

| | SIGN | DATE |
|---|---|---|
| DRAWN | SURAJ | 08/04/17 |
| CHECK | SAGAR P. | 08/04/17 |
| REV. | | |
| APPROVAL | | |

If any queries contact : projects@nihva.com

ALL DIMENSION ARE IN mm

CLIENT - ITC

PROJECT -

SITE - GUNTUR,A.P

DWG. NO. : NIHVA/17-18/0005

SCALE: NTS | WT: | SHEET: 01 OF 01