
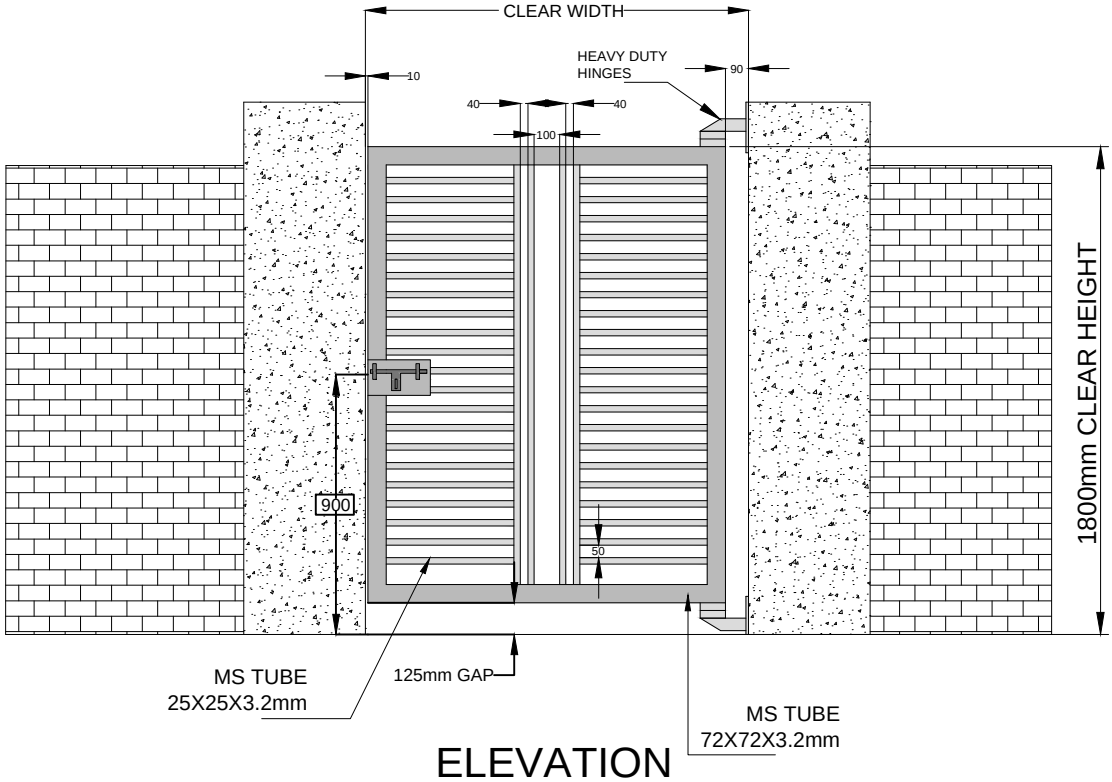


ELEVATION

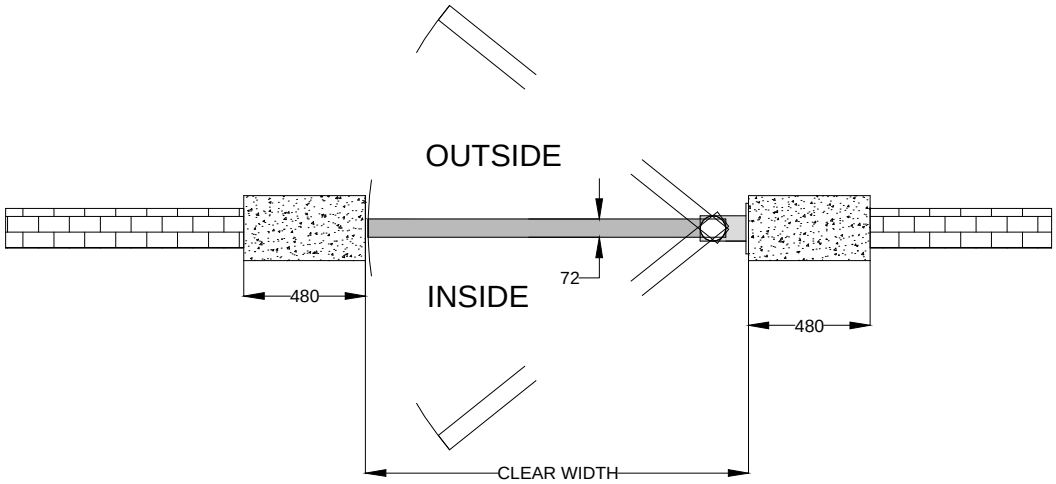

PLAN

SR NO	CLEAR WIDTH.	CLEAR HEIGHT	QTY.
1	1500mm	1800mm	01NOS
2	1200mm	1800mm	01NOS

REV:-01.(02-04-2018)
(A).DRAWING IS UPDATED AS PER PREVIOUS.
(B). ADDED WICKET GATE.

TOLERANCE - ±10mm

This drawing & design is the property of NIHVA TECHNOLOGIES. Not to be sold or copied to any other concern.

TITLE

WICKET GATE

	NAME	SIGN	DATE
DRAWN	SURAJ		16-03-2018
CHECK	OMKAR		16-03-2018
APPRD.	SHEKHAR		16-03-2018

NIHVA TECHNOLOGIES PVT. LTD.
NIHVA TECHNOLOGIES PVT. LTD. PUNE
Tel : 020 66304033
Email:- info@nihva.com
Website:- www.nihva.com

CLIENT - SCON PROJECT

PROJECT - ARI ARMATUREN STEAMLINE LLP

SITE LOCATION -PUNE

If any queries contact : design@nihva.com

DWG. NO. : NIHVA/17-18/0400/R01. REV- 01.

ALL DIMENSION ARE IN mm

SCALE: NTS WT: SHEET: 01 OF 01

A3